

tekeningen CONSTRUCTIE, ELEKTRA & INSTALLATIES

schaal 1:100

principe details BOUWKUNDIG

schaal 1:5

Examenadviesburo 2112.8428



Overzicht Palen

Alle houten palen; paalpunt diameter ø150 + oplanger

PALENRENVOOI								
merk	paalno	diameter		bovenkant opzetter t.o.v. PEIL	paallengte in m	paalbelas-ting in kN opzetter Fr.fund:mac.d.t.o.v. PEIL	afkaphoogte t.o.v. PEIL	onderkant paal t.o.v. NAP
	1 t/m 25	ø150		290-		127	620-	13,0m-

Gegevens betreffende de grond + funderingsadvies volgens grondrapport (Opdrachtnr.: 1016-0537-000) van Fugro Geosevices b.v. Edisonlaan 31B 6003 DB Weert

Uitvoering heiwerk volgens ditzelfde rapport

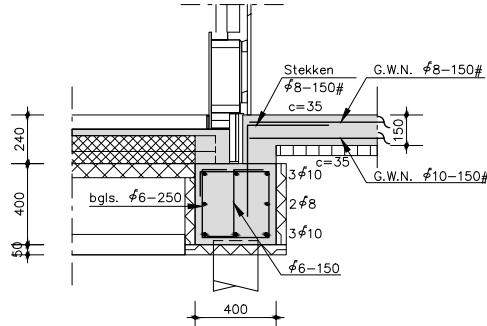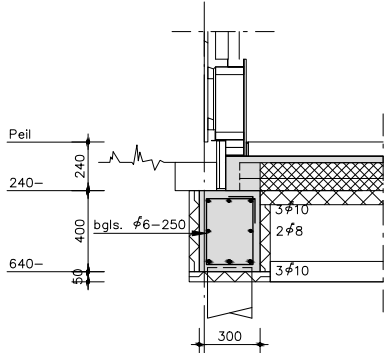



Balk A/B1/B3
Balk C/D1/E
Balk F/G/H
Balk I¹/I²/I³
Balk J/K/M/N¹/O

Balk-D1 extra bgls.+
bovenwap. zie overzicht

Balk-J+K extra
bgls. zie overzicht

Balk B2¹/B2²
Balk D2¹/D2²
Balk N2¹/N2²
Balk L

met extra bgls.
zie overzicht

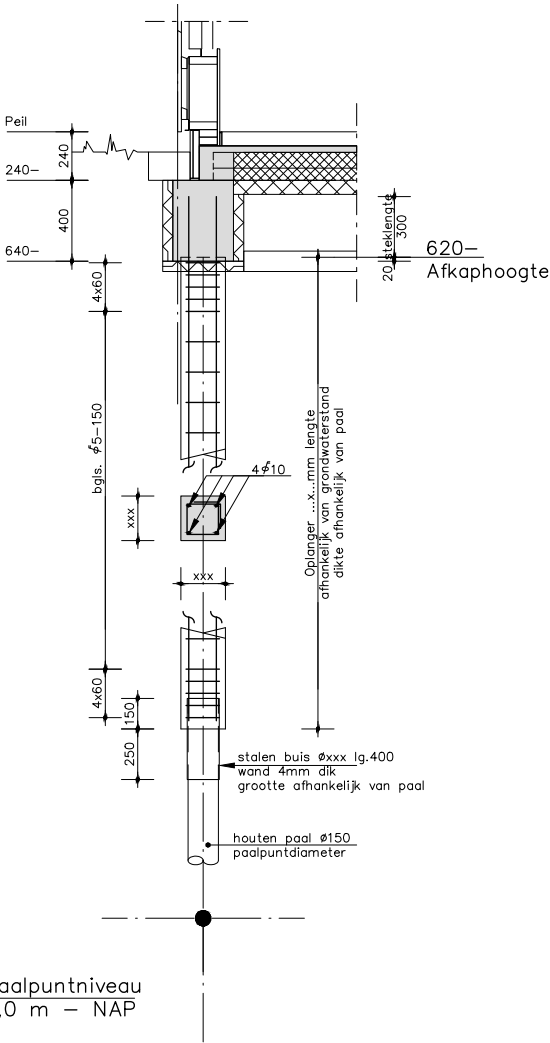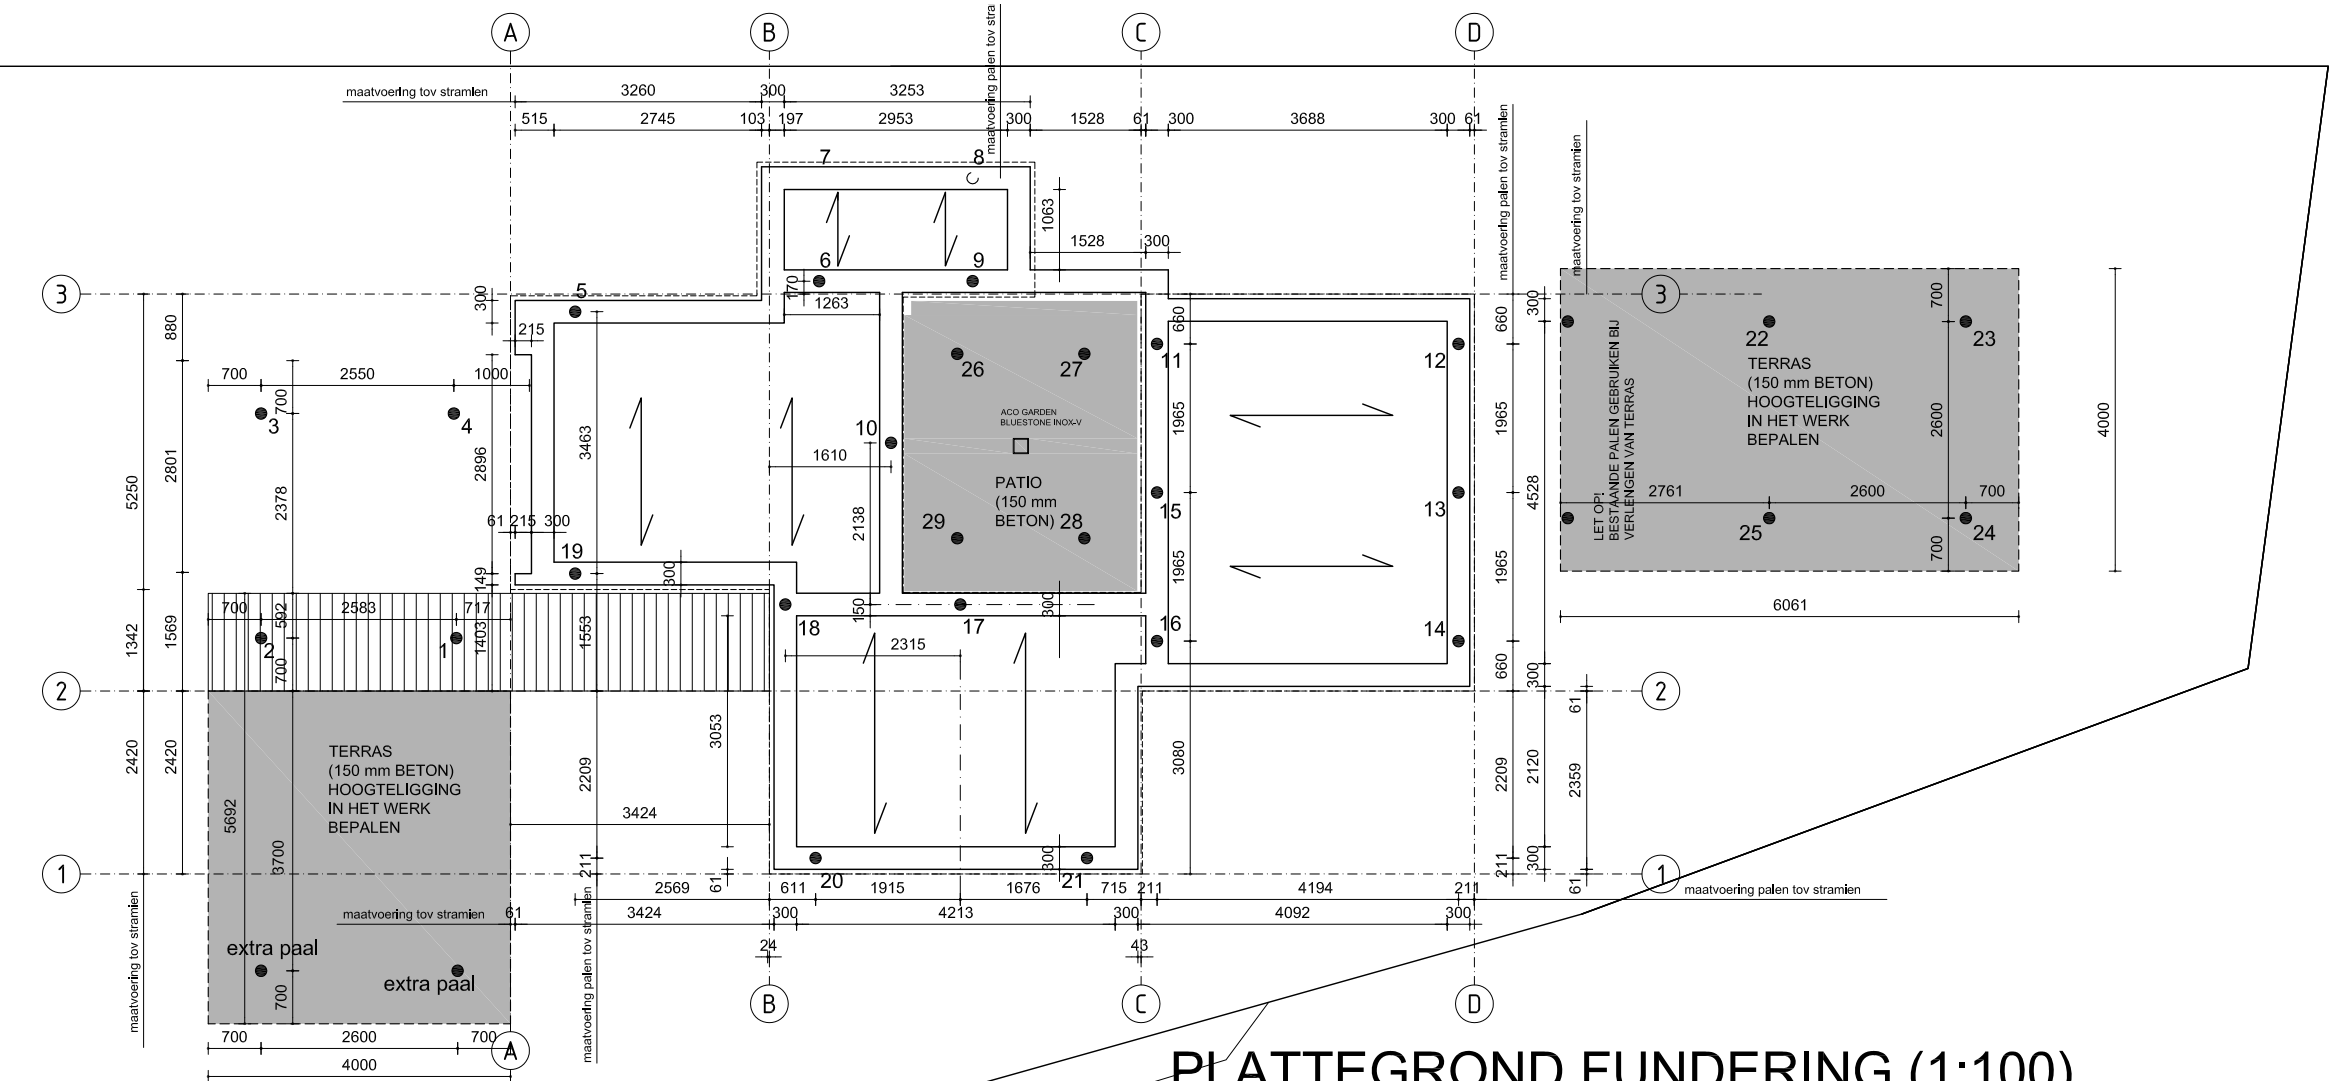


o.k. paalpuntniveau
op 13,0 m - NAP



Constructieve plattegrond
fundering en bg
schaal 1:100

BLAD 2

Examenadviesburo 2112.8428

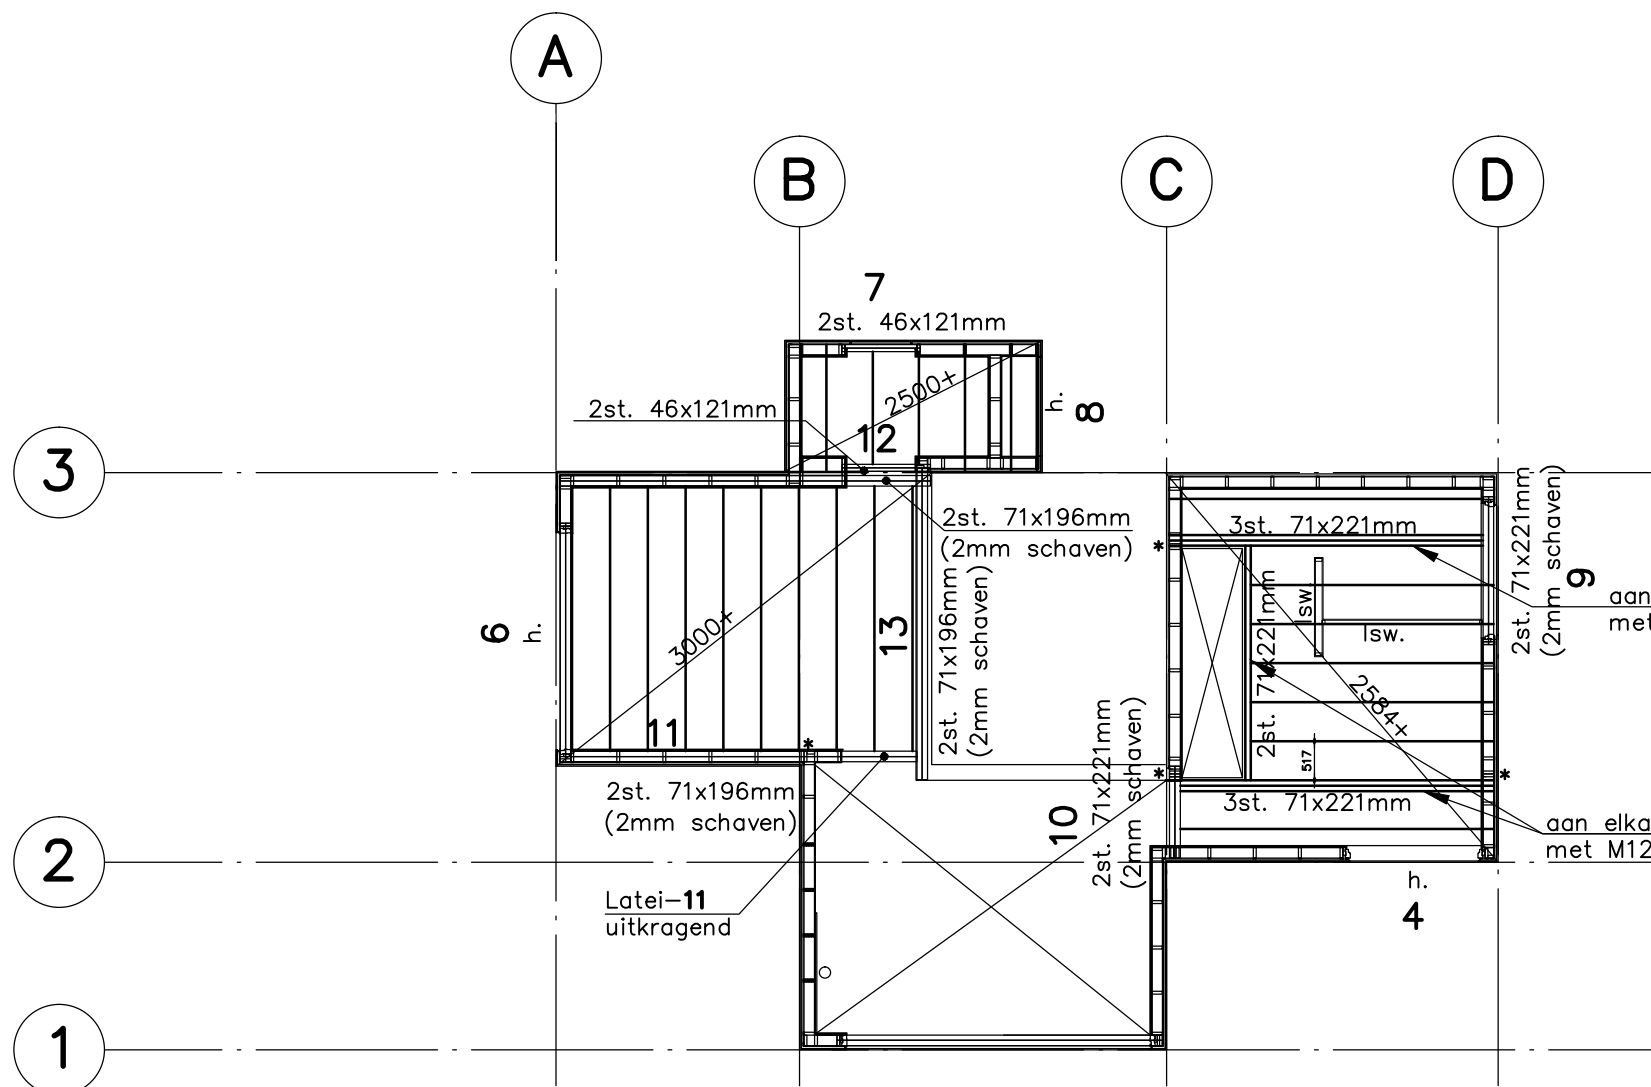

houtdr.b. M6x110mm
h.o.h. 192mm
verspringend aanbrengen

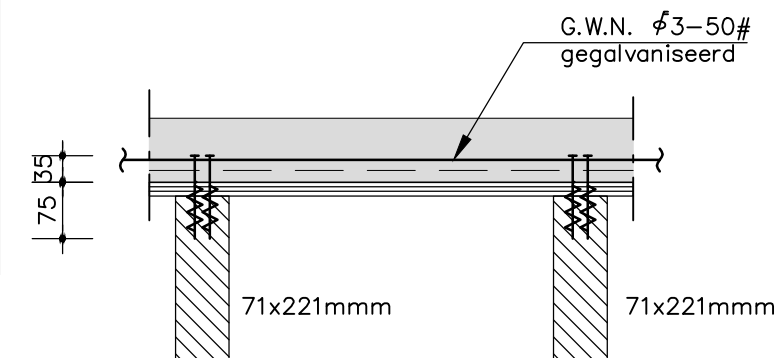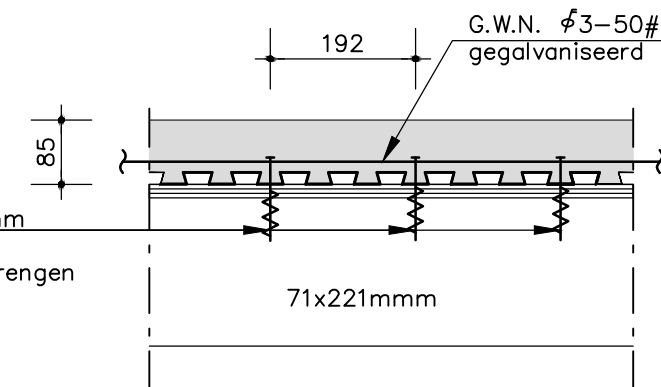

Aansluiting Lewis-plaat

Betonvloer aan de bovenzijde vlak afwerken

BELASTINGEN : Dak op 3 000+/2 500+
blijvende belasting balklaag e.d. = $0,90 \text{ kN/m}^2$
mos-sedum = $1,00 \text{ kN/m}^2$
variabele belasting 2 600+ = $1,00 \text{ kN/m}^2$ (max. 10 m^2)
variabele belasting 3 000+ = $2,50 \text{ kN/m}^2$ (op verzoek opdrachtgever)
sneeuwbelasting vlg. NEN-EN 1991-1-3

BELASTINGEN : Verdiepingsvloer op 2 584+
Lewis betonvloer = $1,58 \text{ kN/m}^2$ ($d=85 \text{ mm}$)
afwerking = $0,60 \text{ kN/m}^2$
blijvende belasting balklaag e.d. = $0,18 \text{ kN/m}^2$
plafondafwerking = $0,15 \text{ kN/m}^2$
variabele belasting = $1,75 \text{ kN/m}^2$
lichte scheidingswanden = $0,50 \text{ kN/m}^2$

Overzicht verdiepingsvloer/dakvloer op 2 500+ /3 000+

Latei-**9+10+11+12+13** aan elkaar koppelen met ankers M12-600

lsw. = lichte scheidingswand (hout) op vloer

Dakbalklaag op 3 000+: 71x196mm; h.o.h. 500mm

Dakbalklaag op 2 500+: 46x121mm; h.o.h. 610mm

Balklaag verdieping: 71x221mm; h.o.h. 517mm


Wandstijlen: 38x140mm; h.o.h. 610mm (CLS/SLS C18)

* Dubbele stijlen 38x140mm

**Constructieve plattegrond
verdiepingsvloer
schaal 1:100**

BLAD 3

Examenadviesburo 2112.8428

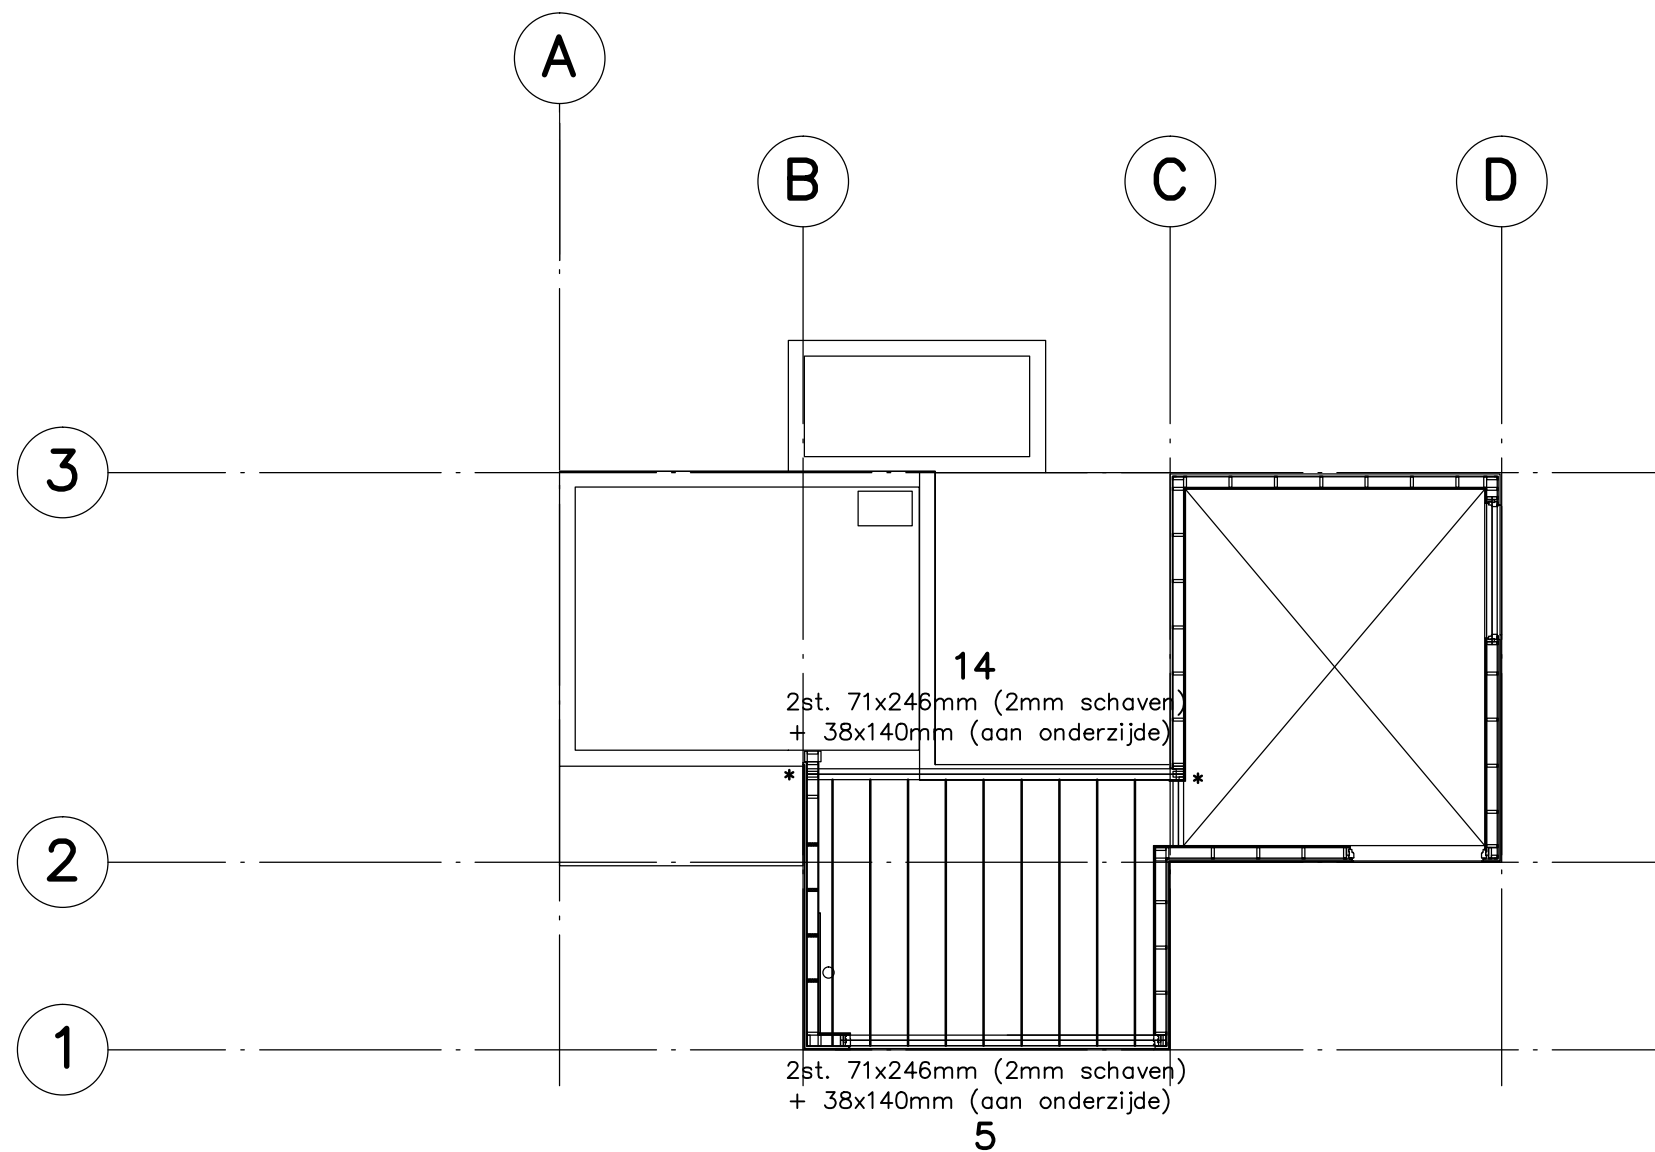

BELASTINGEN : **Dak op 3 800+**
 blijvende belasting balklaag e.d. = $0,90 \text{ kN/m}^2$
 mos-sedum = $1,00 \text{ kN/m}^2$
 variabele belasting = $1,00 \text{ kN/m}^2$ (max. 10m^2)
 sneeuwbelasting vlg. NEN-EN 1991-1-3


Overzicht dak op 3 800+

Dakbalklaag: 71x196mm; h.o.h. 500mm

Latei-**5**+**-14** aan elkaar koppelen/verlijmen met ankers M12-600

* Dubbele stijlen 38x140mm

- HOUTSKELETBOUW :
- OSB d=12mm (binnen), tenzij anders aangegeven
- Stijlen : 38x140mm, h.o.h. 610mm (CLS/SLS)
- Horizontale regels : 38x140mm, tenzij anders aangegeven
- Dubbele stijlen naast elke opening, tenzij anders aangegeven + dubbele stijlen t.p.v *
- Vernagelen m.b.v. lijmnagels $2,8 \times 50$
- Onder gebruikelijke nageling dient te worden verstaan : nagels op afstanden van 100mm op regels, randstijlen en ter weerszijden van verticalen naden en op afstanden van 200mm op tussenstijlen.
- Bij horizontale naden waarachter geen klos wordt aangebracht, moeten bij elke stijl drie nagels ter weerszijden van de naad worden toegepast.
- Verankering HSB-wand met M10-400 lg.190, gaten $\varnothing 12 \times 115$, boven in de vloer, vastlijmen met Hilti Hit-HY 200-A mortel (2 stuks) bij verticale naad HSB-wand)

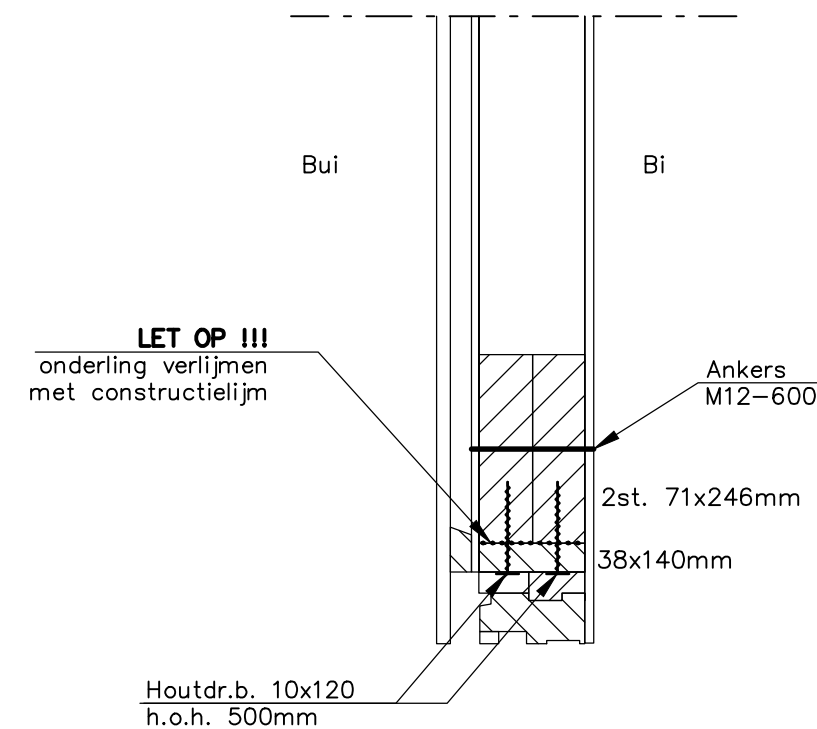


Latei 5+11+14

**Constructieve plattegrond
dakvloer
schaal 1:100**

BLAD 4

Examenadviesburo 2112.8428

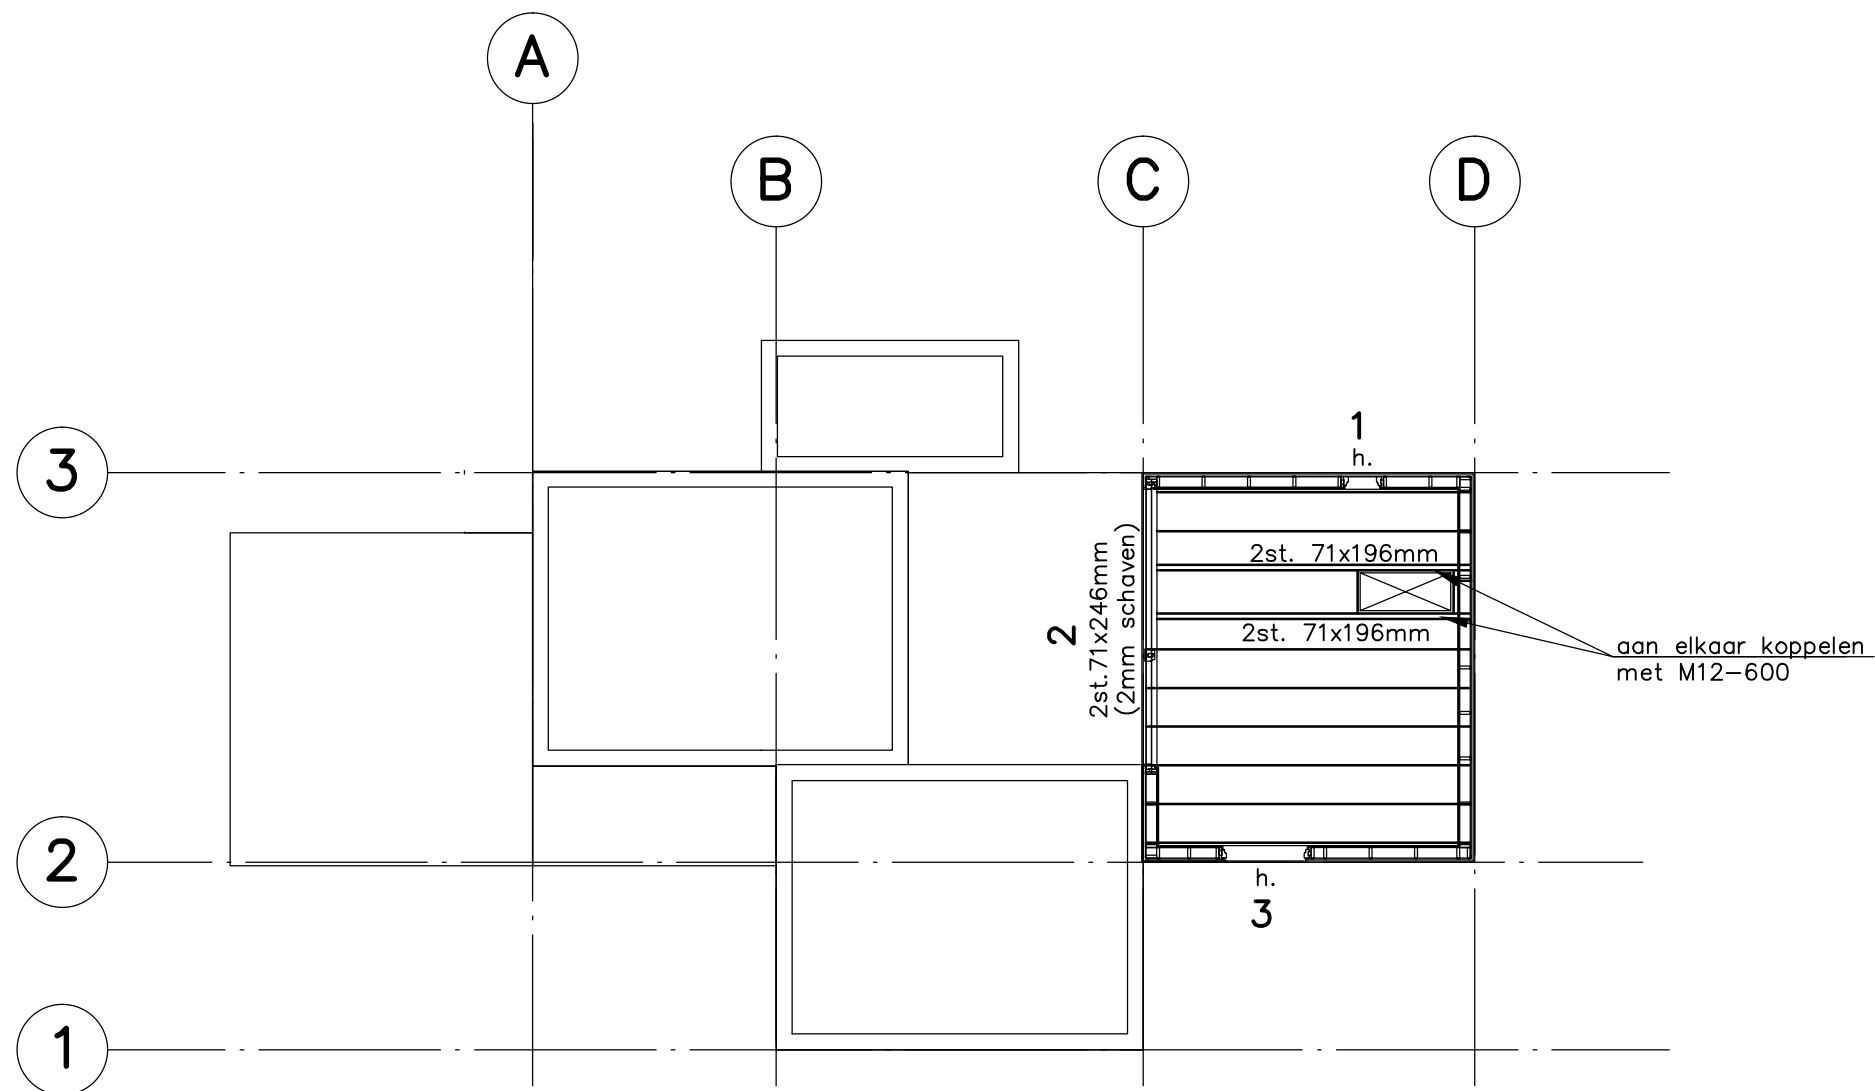


BELASTINGEN : **Dak op 5 400+**
 blijvende belasting balklaag e.d. = $0,90 \text{ kN/m}^2$
 mos-sedum = $1,00 \text{ kN/m}^2$
 variabele belasting = $1,00 \text{ kN/m}^2$ (max. 10m^2)
 sneeuwbelasting vlg. NEN-EN 1991-1-3

Overzicht dak op 5 400+

Dakbalklaag: $71 \times 196\text{mm}$; h.o.h. $\pm 517\text{mm}$

h. = houten afwerking

Latei-2 aan elkaar bevestigen met ankers M12-600

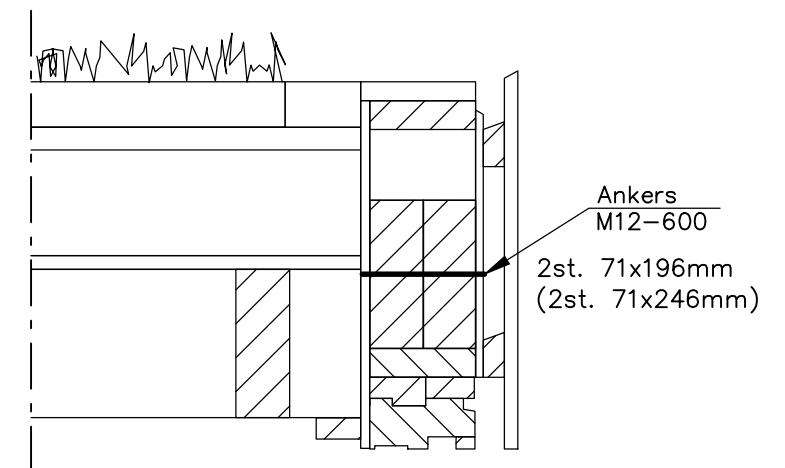

Principe


Latei 9+10+13

Latei 2 met 2st. $71 \times 246\text{mm}$

Constructieve dakvloer
schaal 1:100

BLAD 5


Examenadviesburo 2112.8428

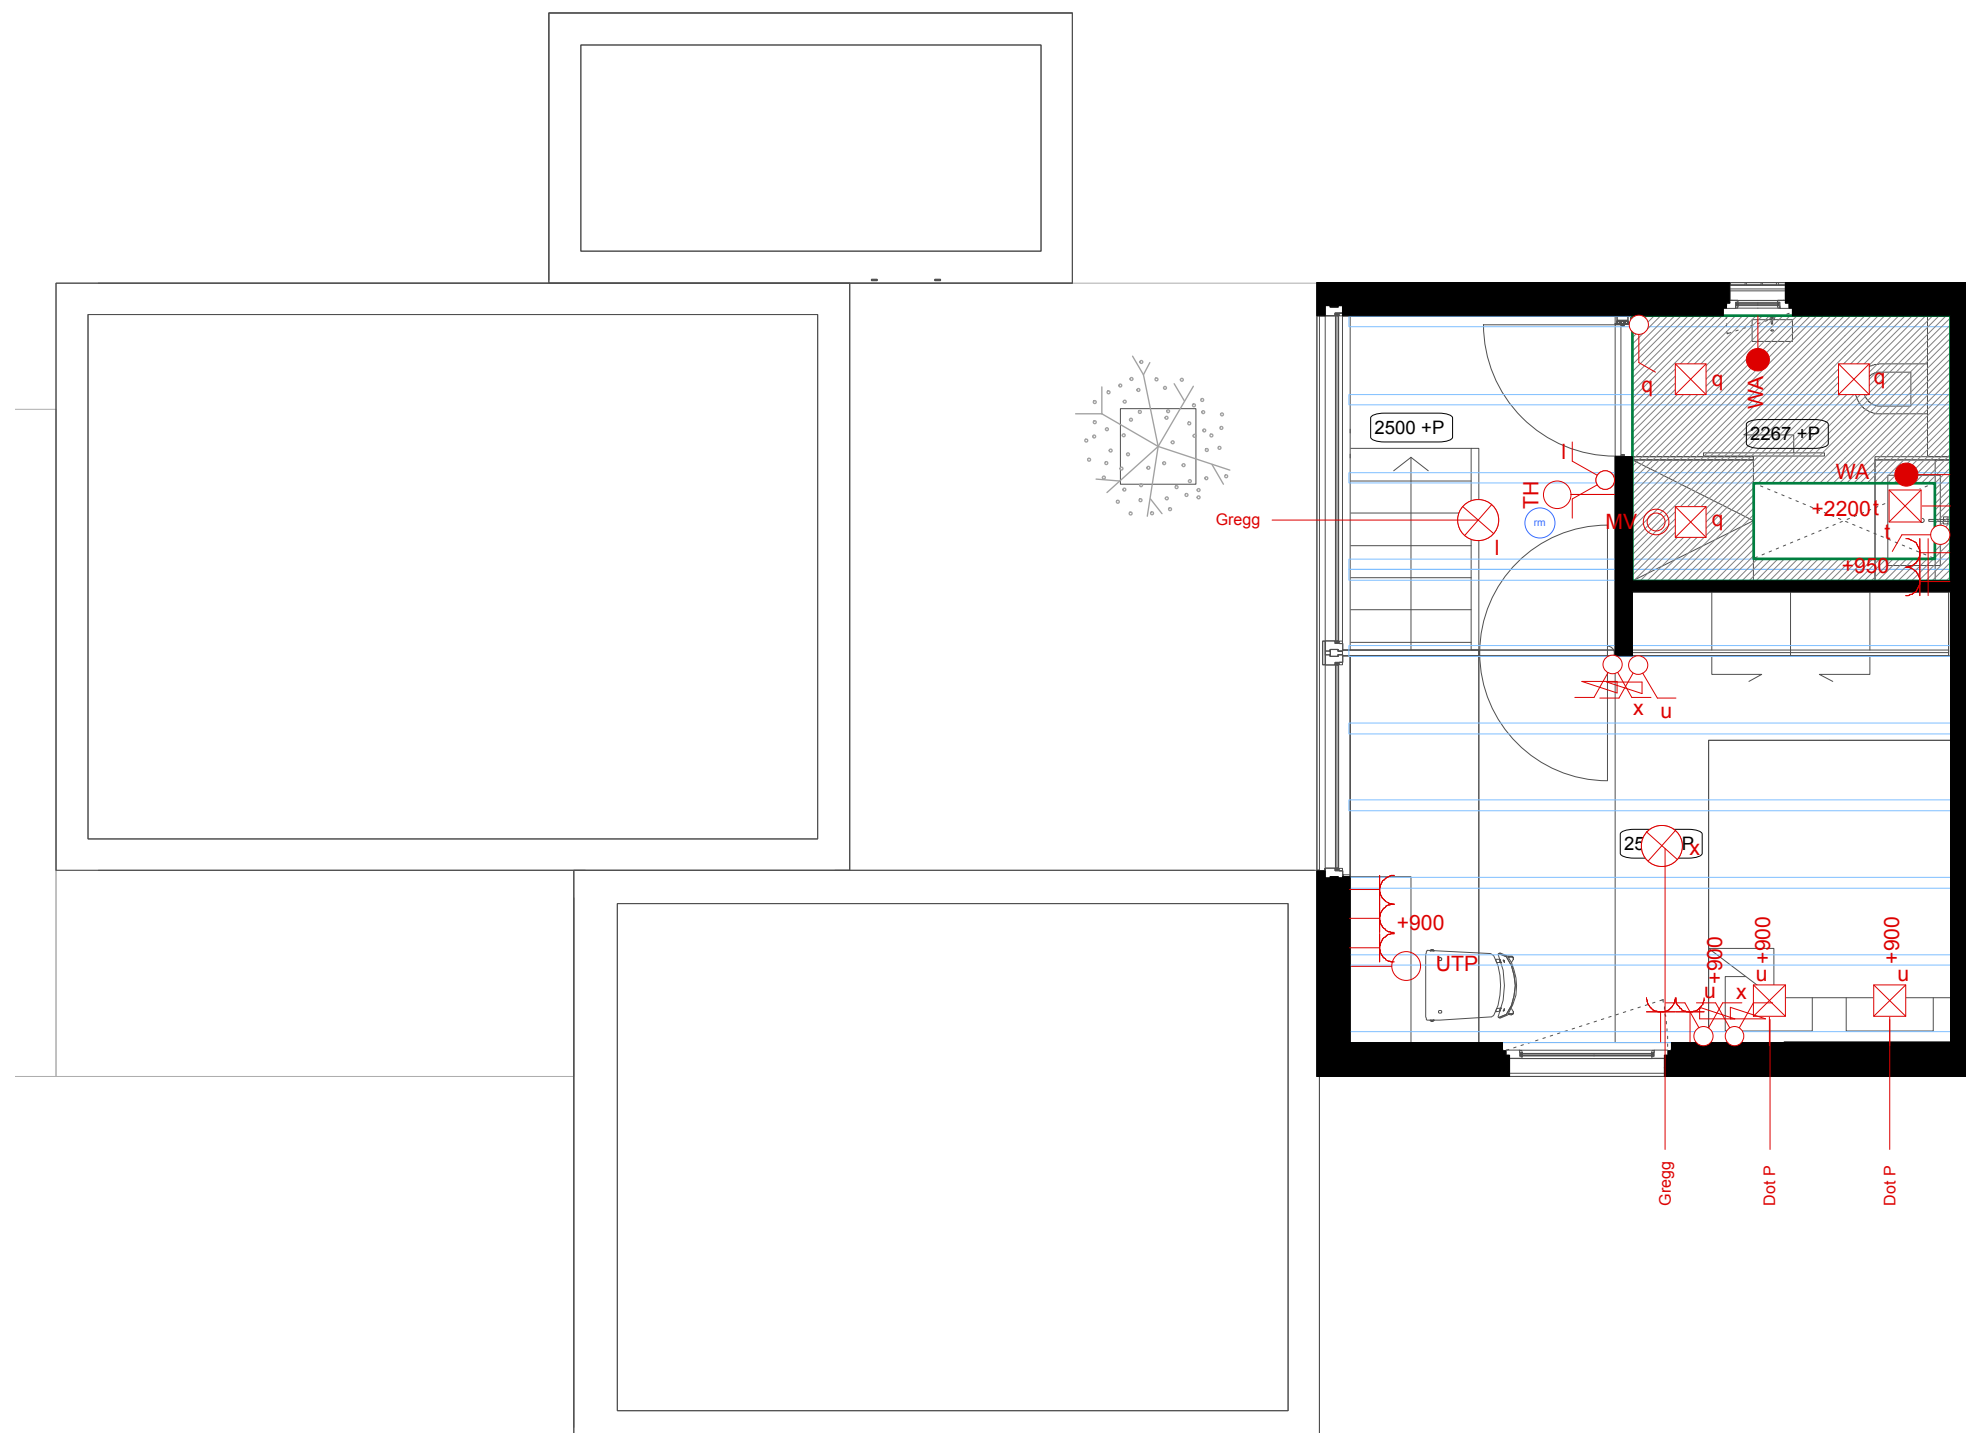



- rookmelder
- lichtpunt hanglamp
- inbouw spot
- lichtpunt wand
- contactdoos geaard enkel
- contactdoos spatwater dicht
- schakelaar enkelvoudig
- hotel schakelaar
- hotel schakelaar gedimd
- dimmer
- schakelaar remote
- bewegingsensor
- staande lamp
- (inbouw) speaker
- telefoon/contactdoos
- televisie/contactdoos
- intercom/deuropener/camera
- netwerk/UTP/internet
- thermostaat
- mechanisch ventilatie
- aan/afvoer warm/koud water
- WC aan/afvoer koudwater
- CV gas, electra, aan/afvoer water
- kookplaat inductie
- wasmachine elektra, aan/afvoer water
- condensdroger elektra, afvoer water
- vaatwasmachine elektra, aan/afvoer water
- combi stoom oven water/ elektra
- koel/vrieskast elektra
- balken
- verlaagd plafond


alle schakelaars +950
alle stopcontacten +250
tenzij anders vermeld

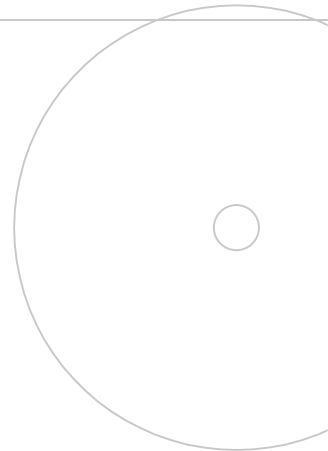


**Examenadviesburo 2112.8428**

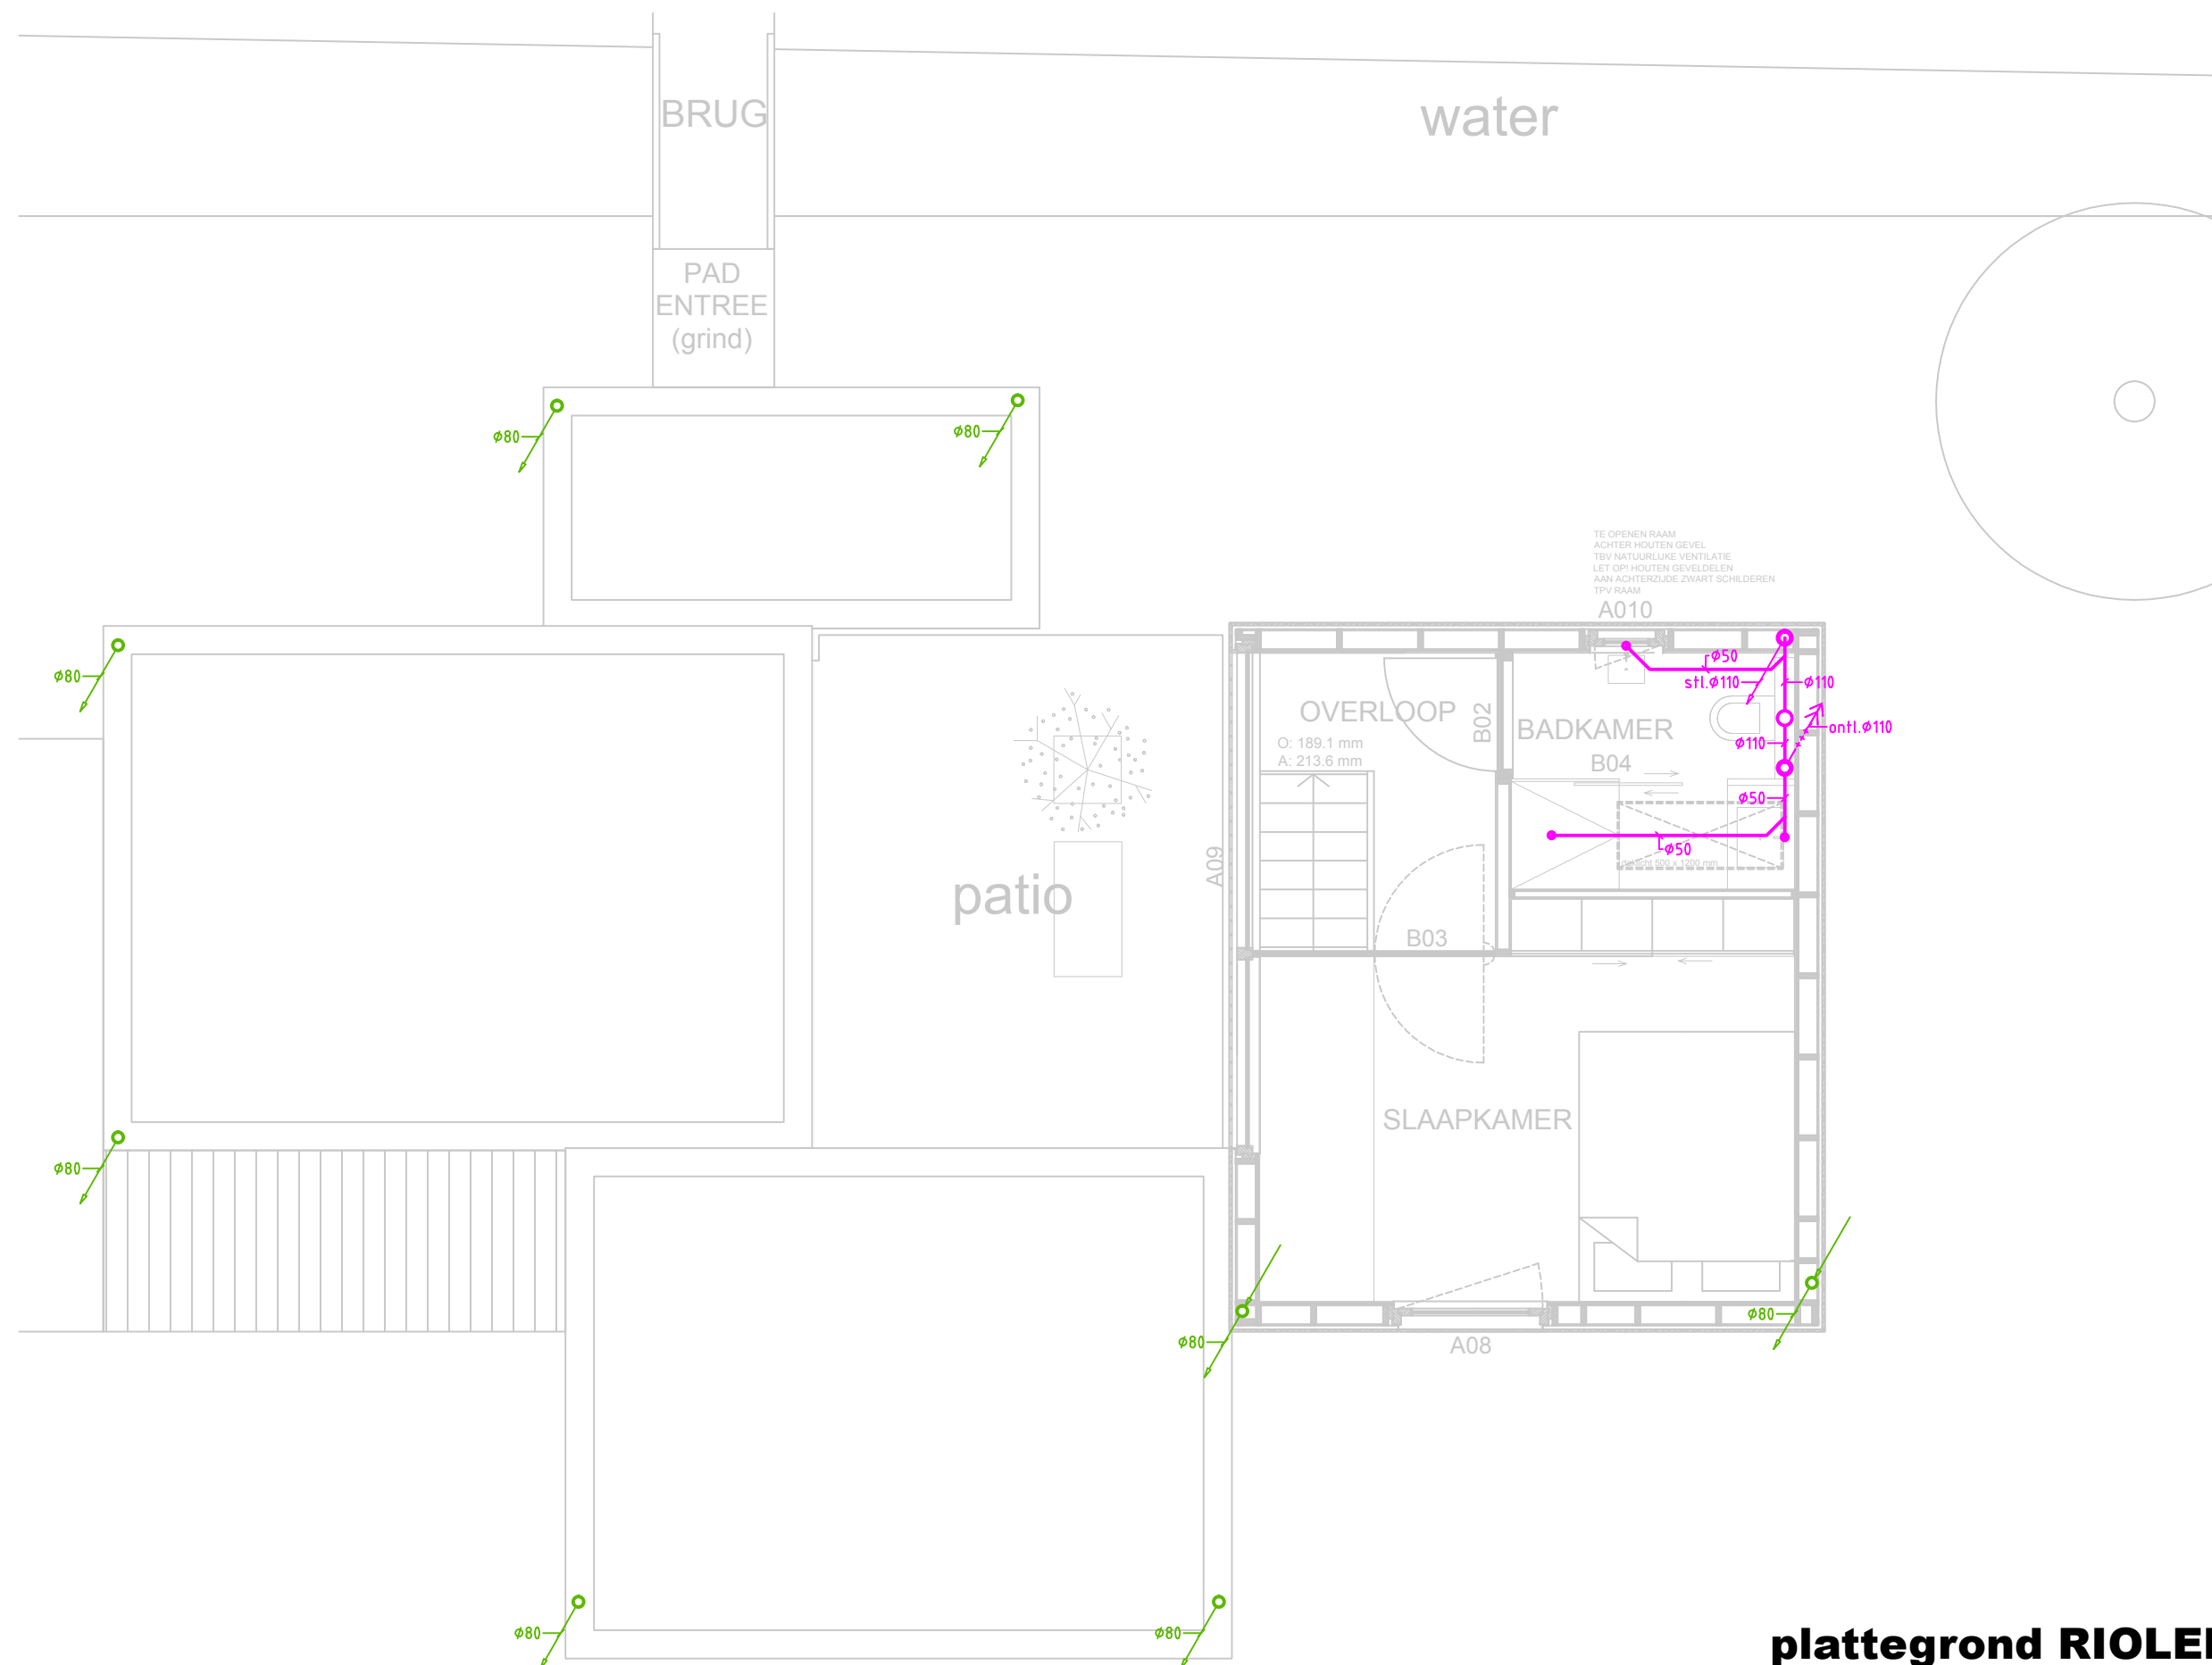


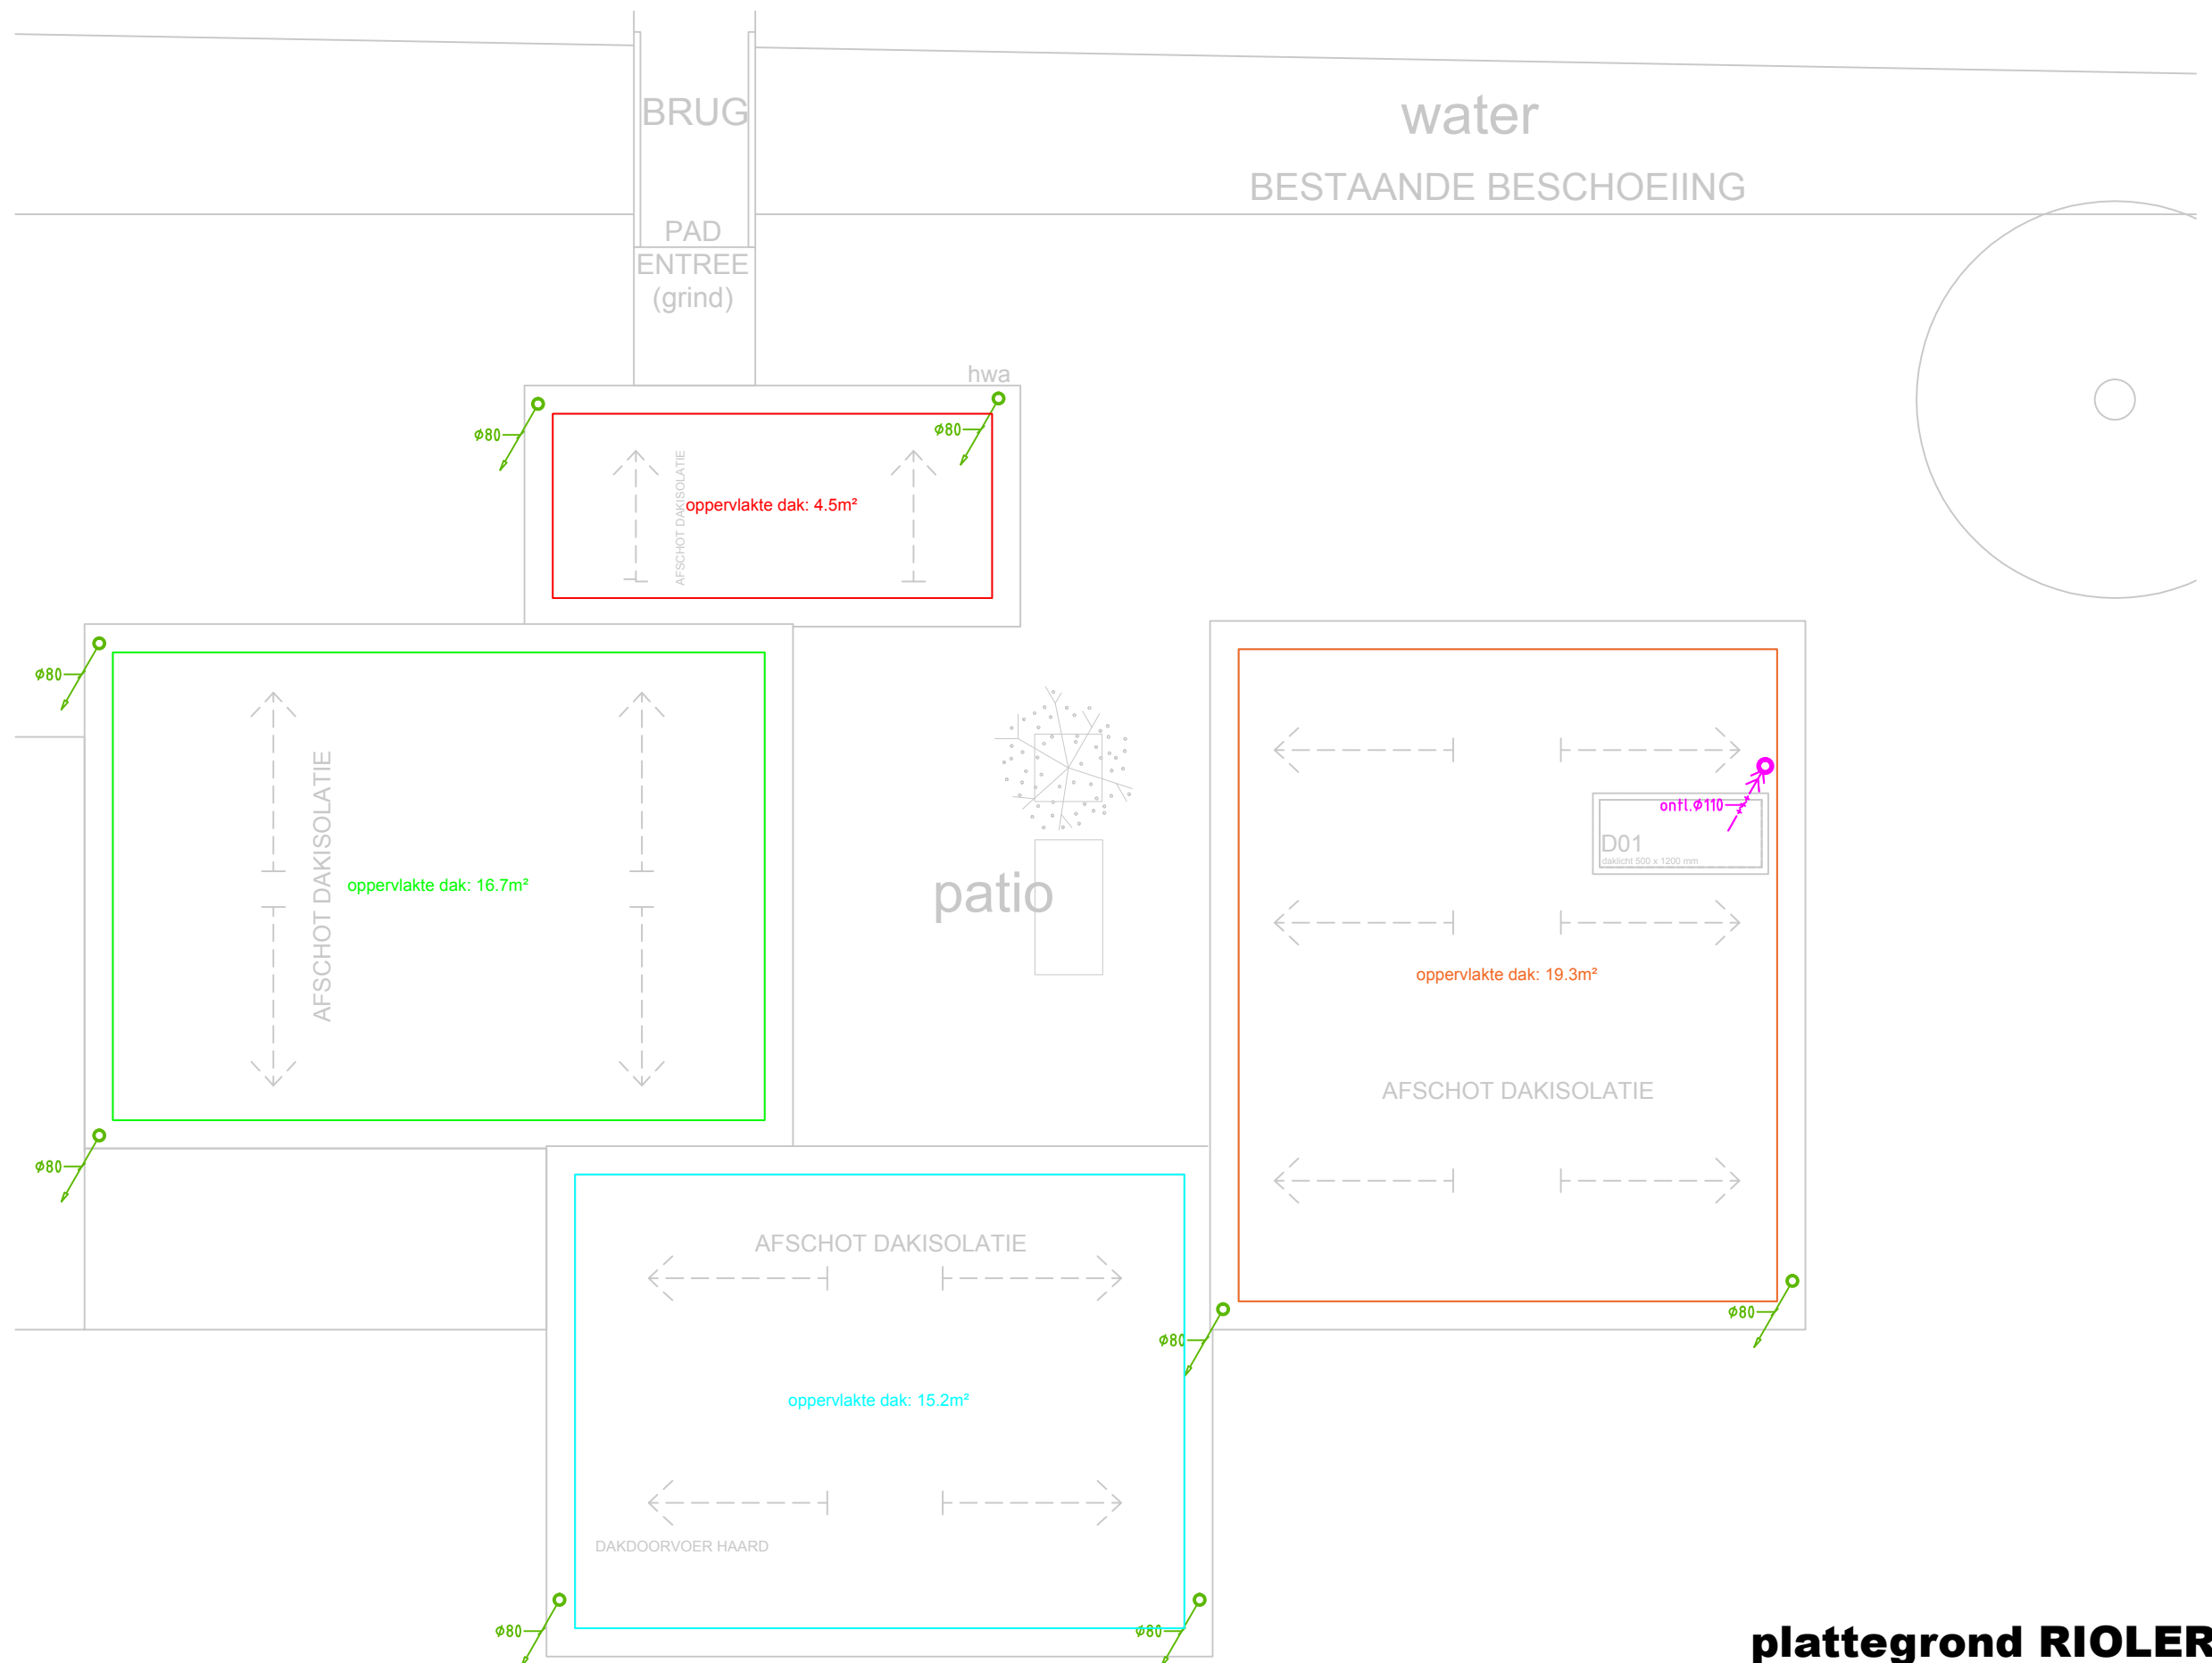

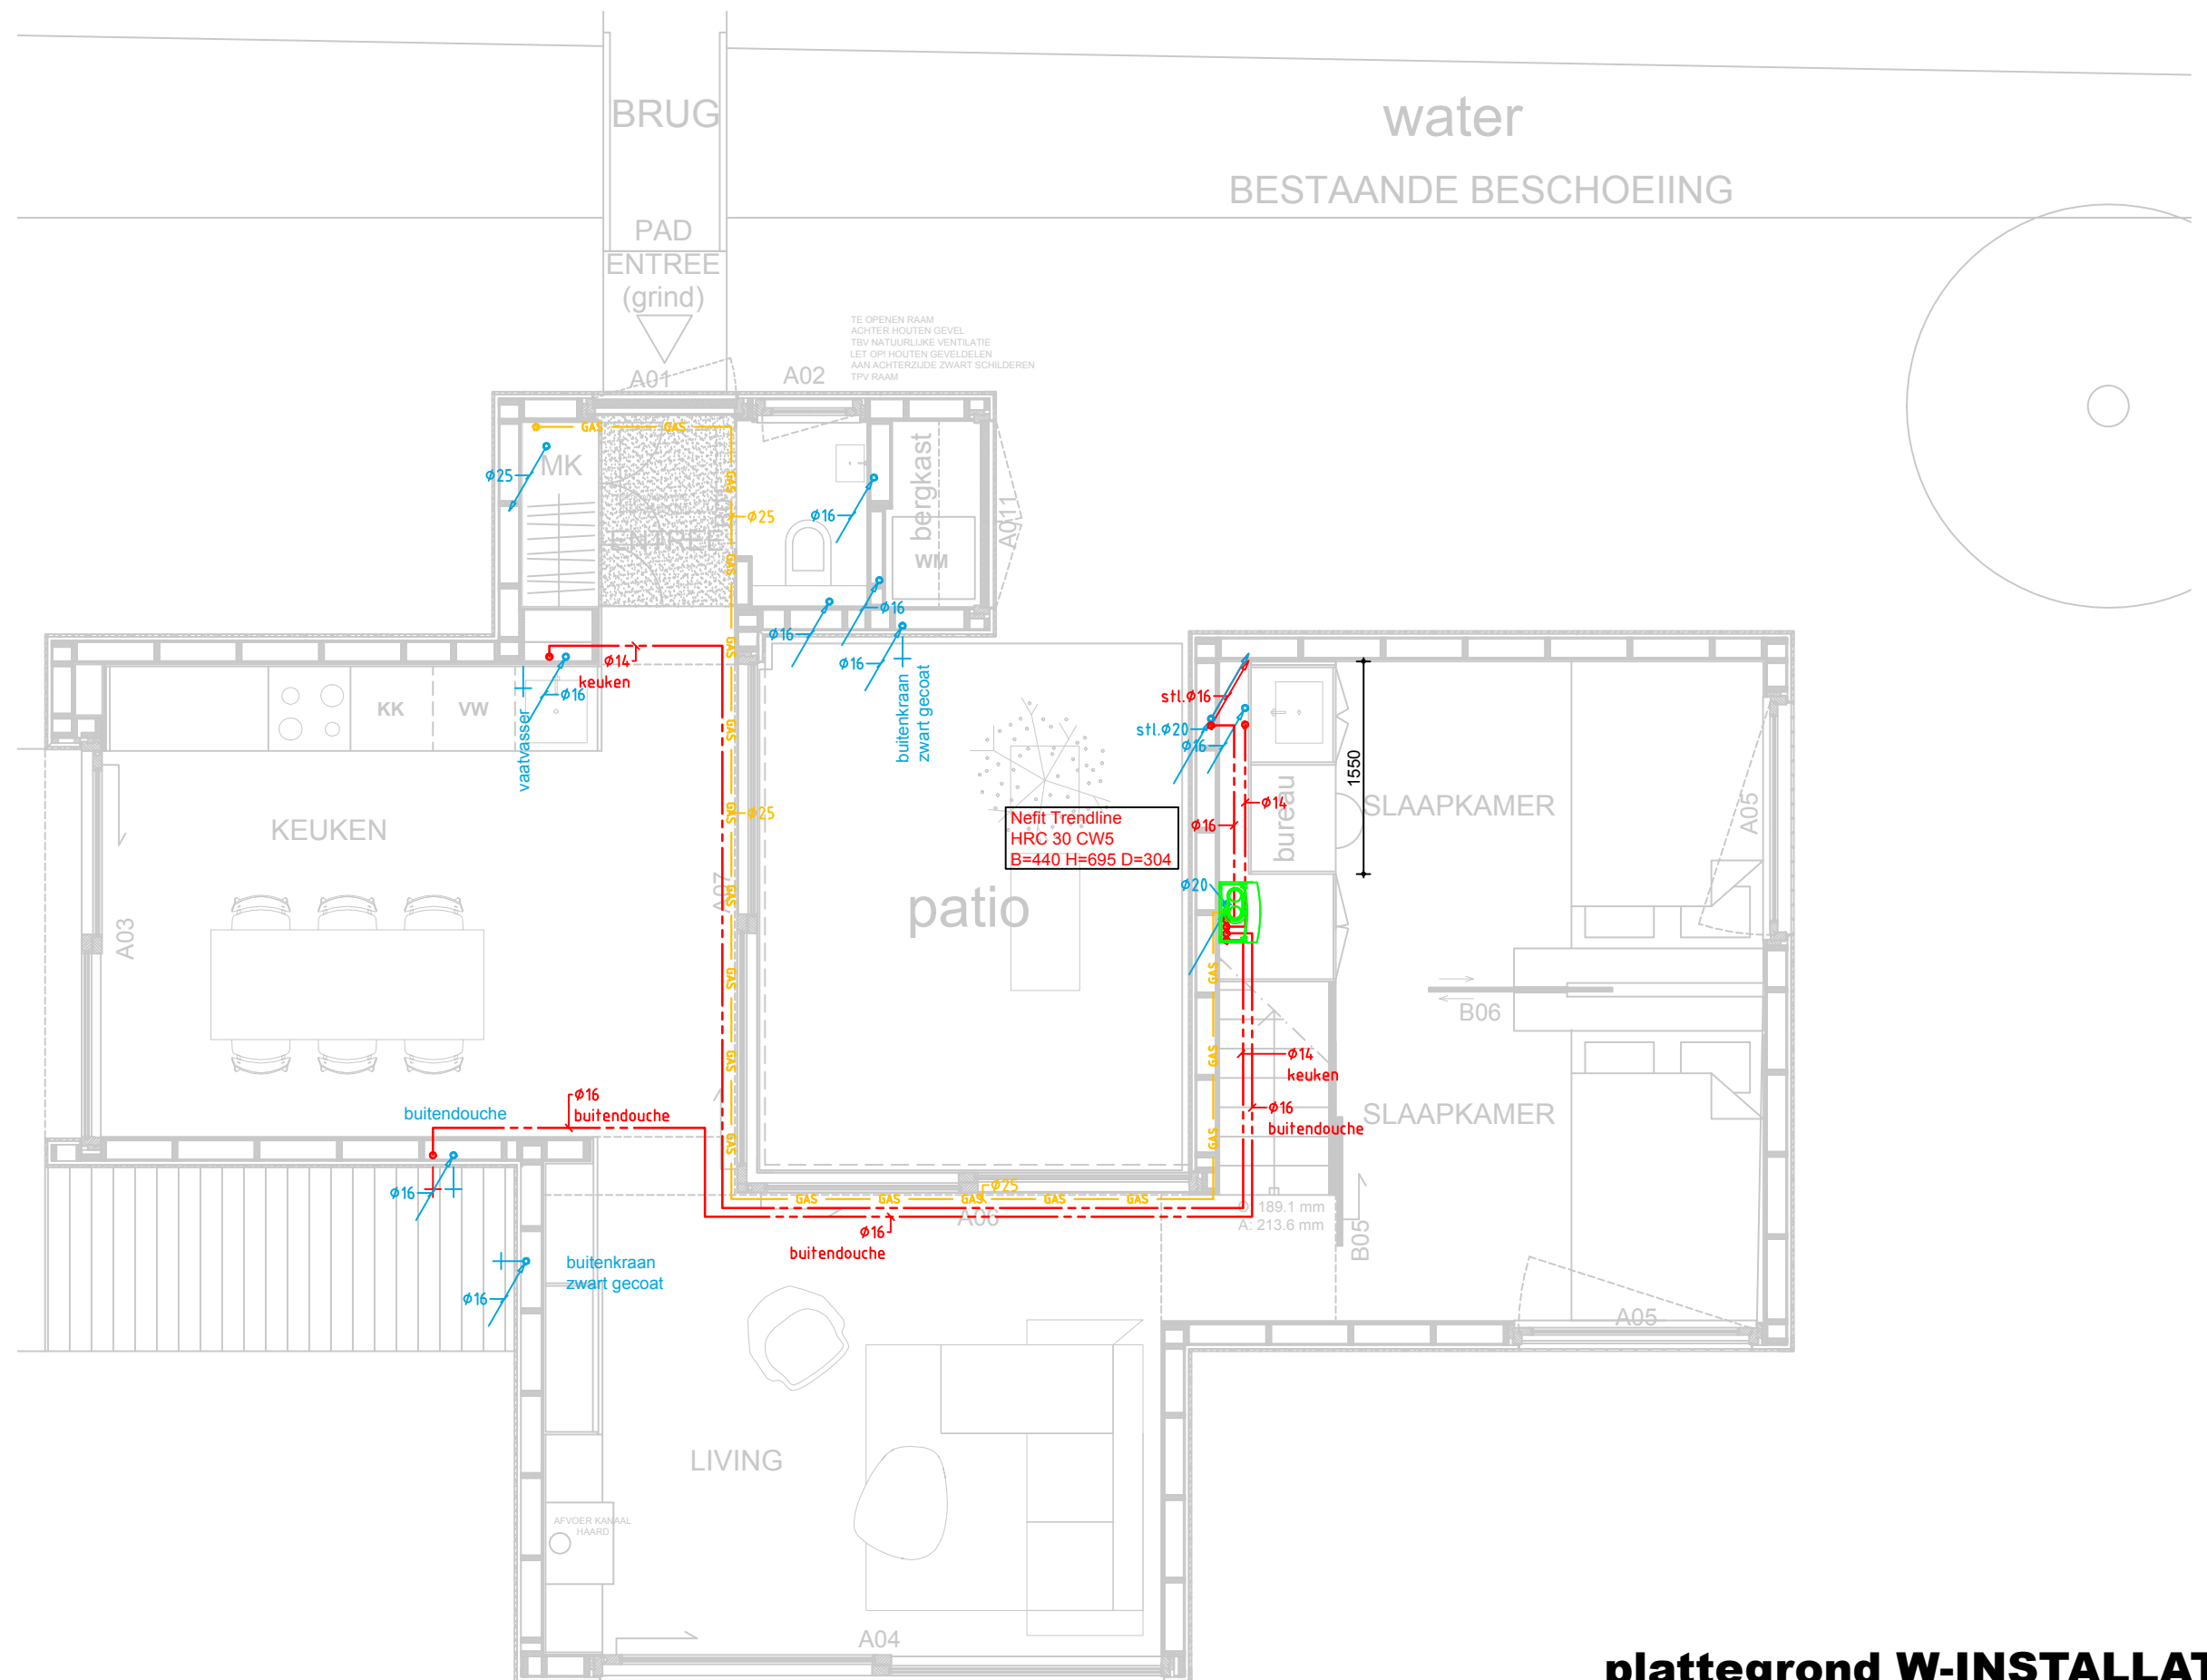


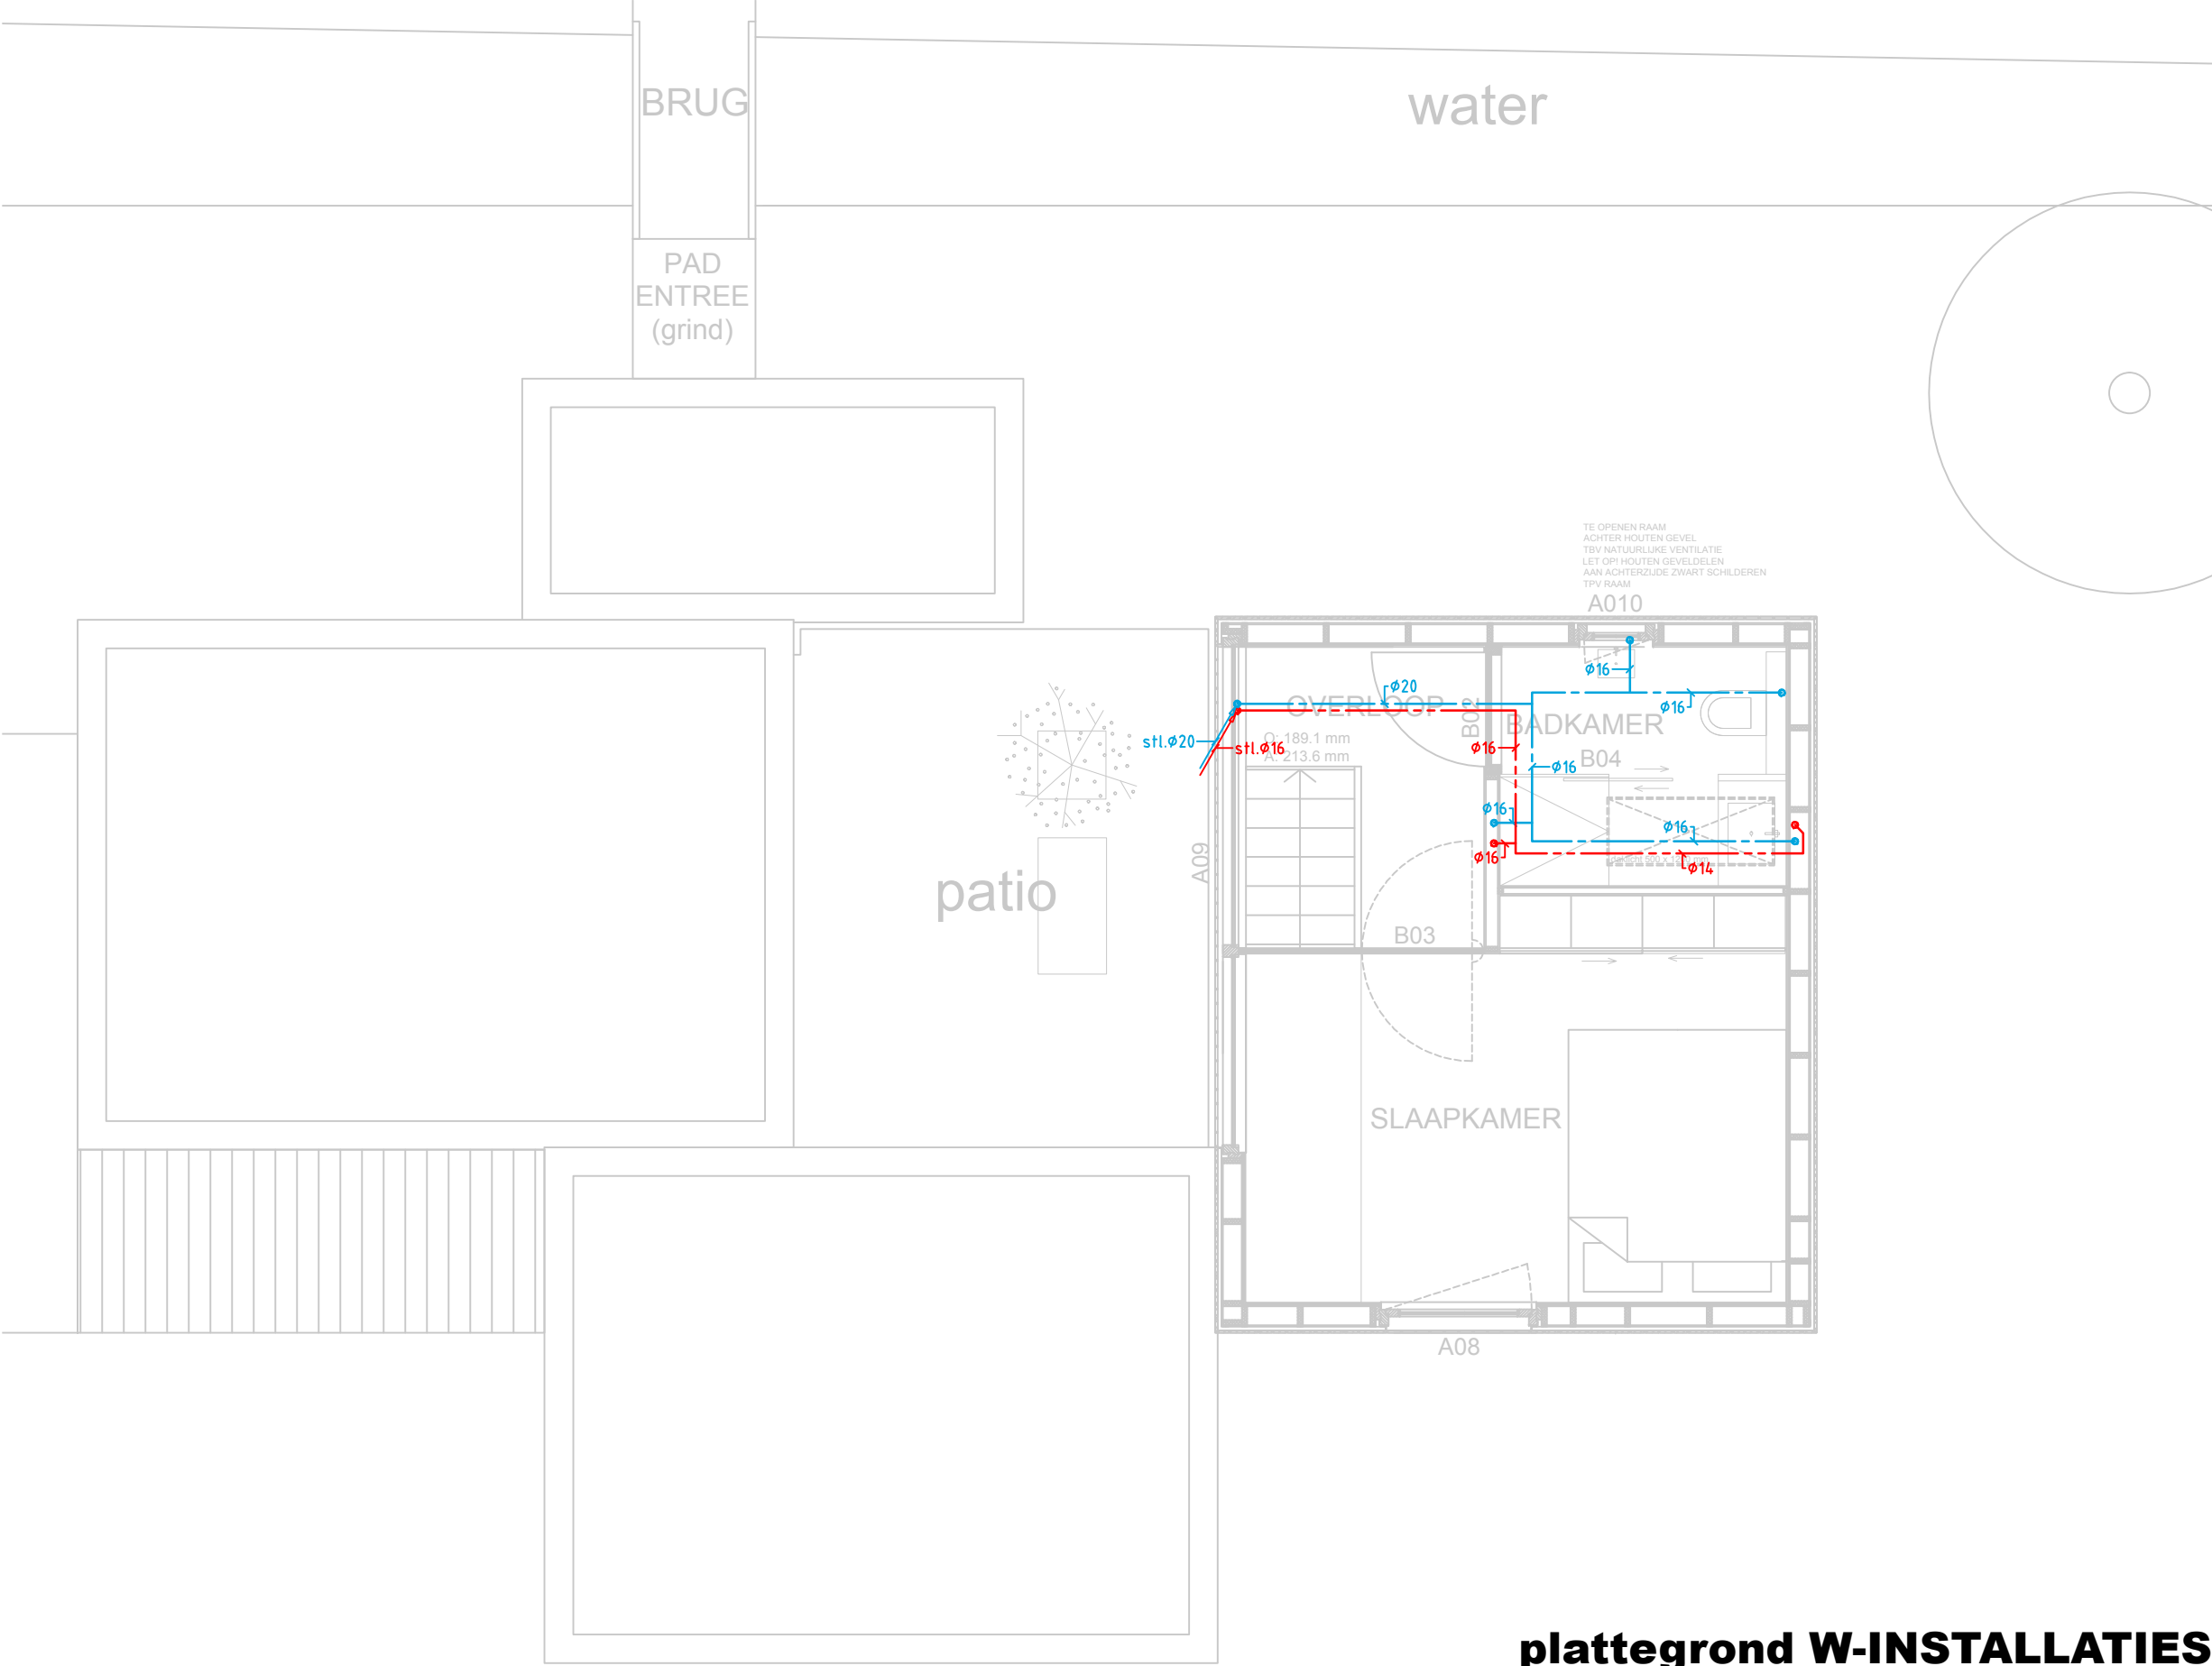

plattegrond W-INSTALLATIES
verdieping
BLAD 13
Examenadviesburo 2112.8428

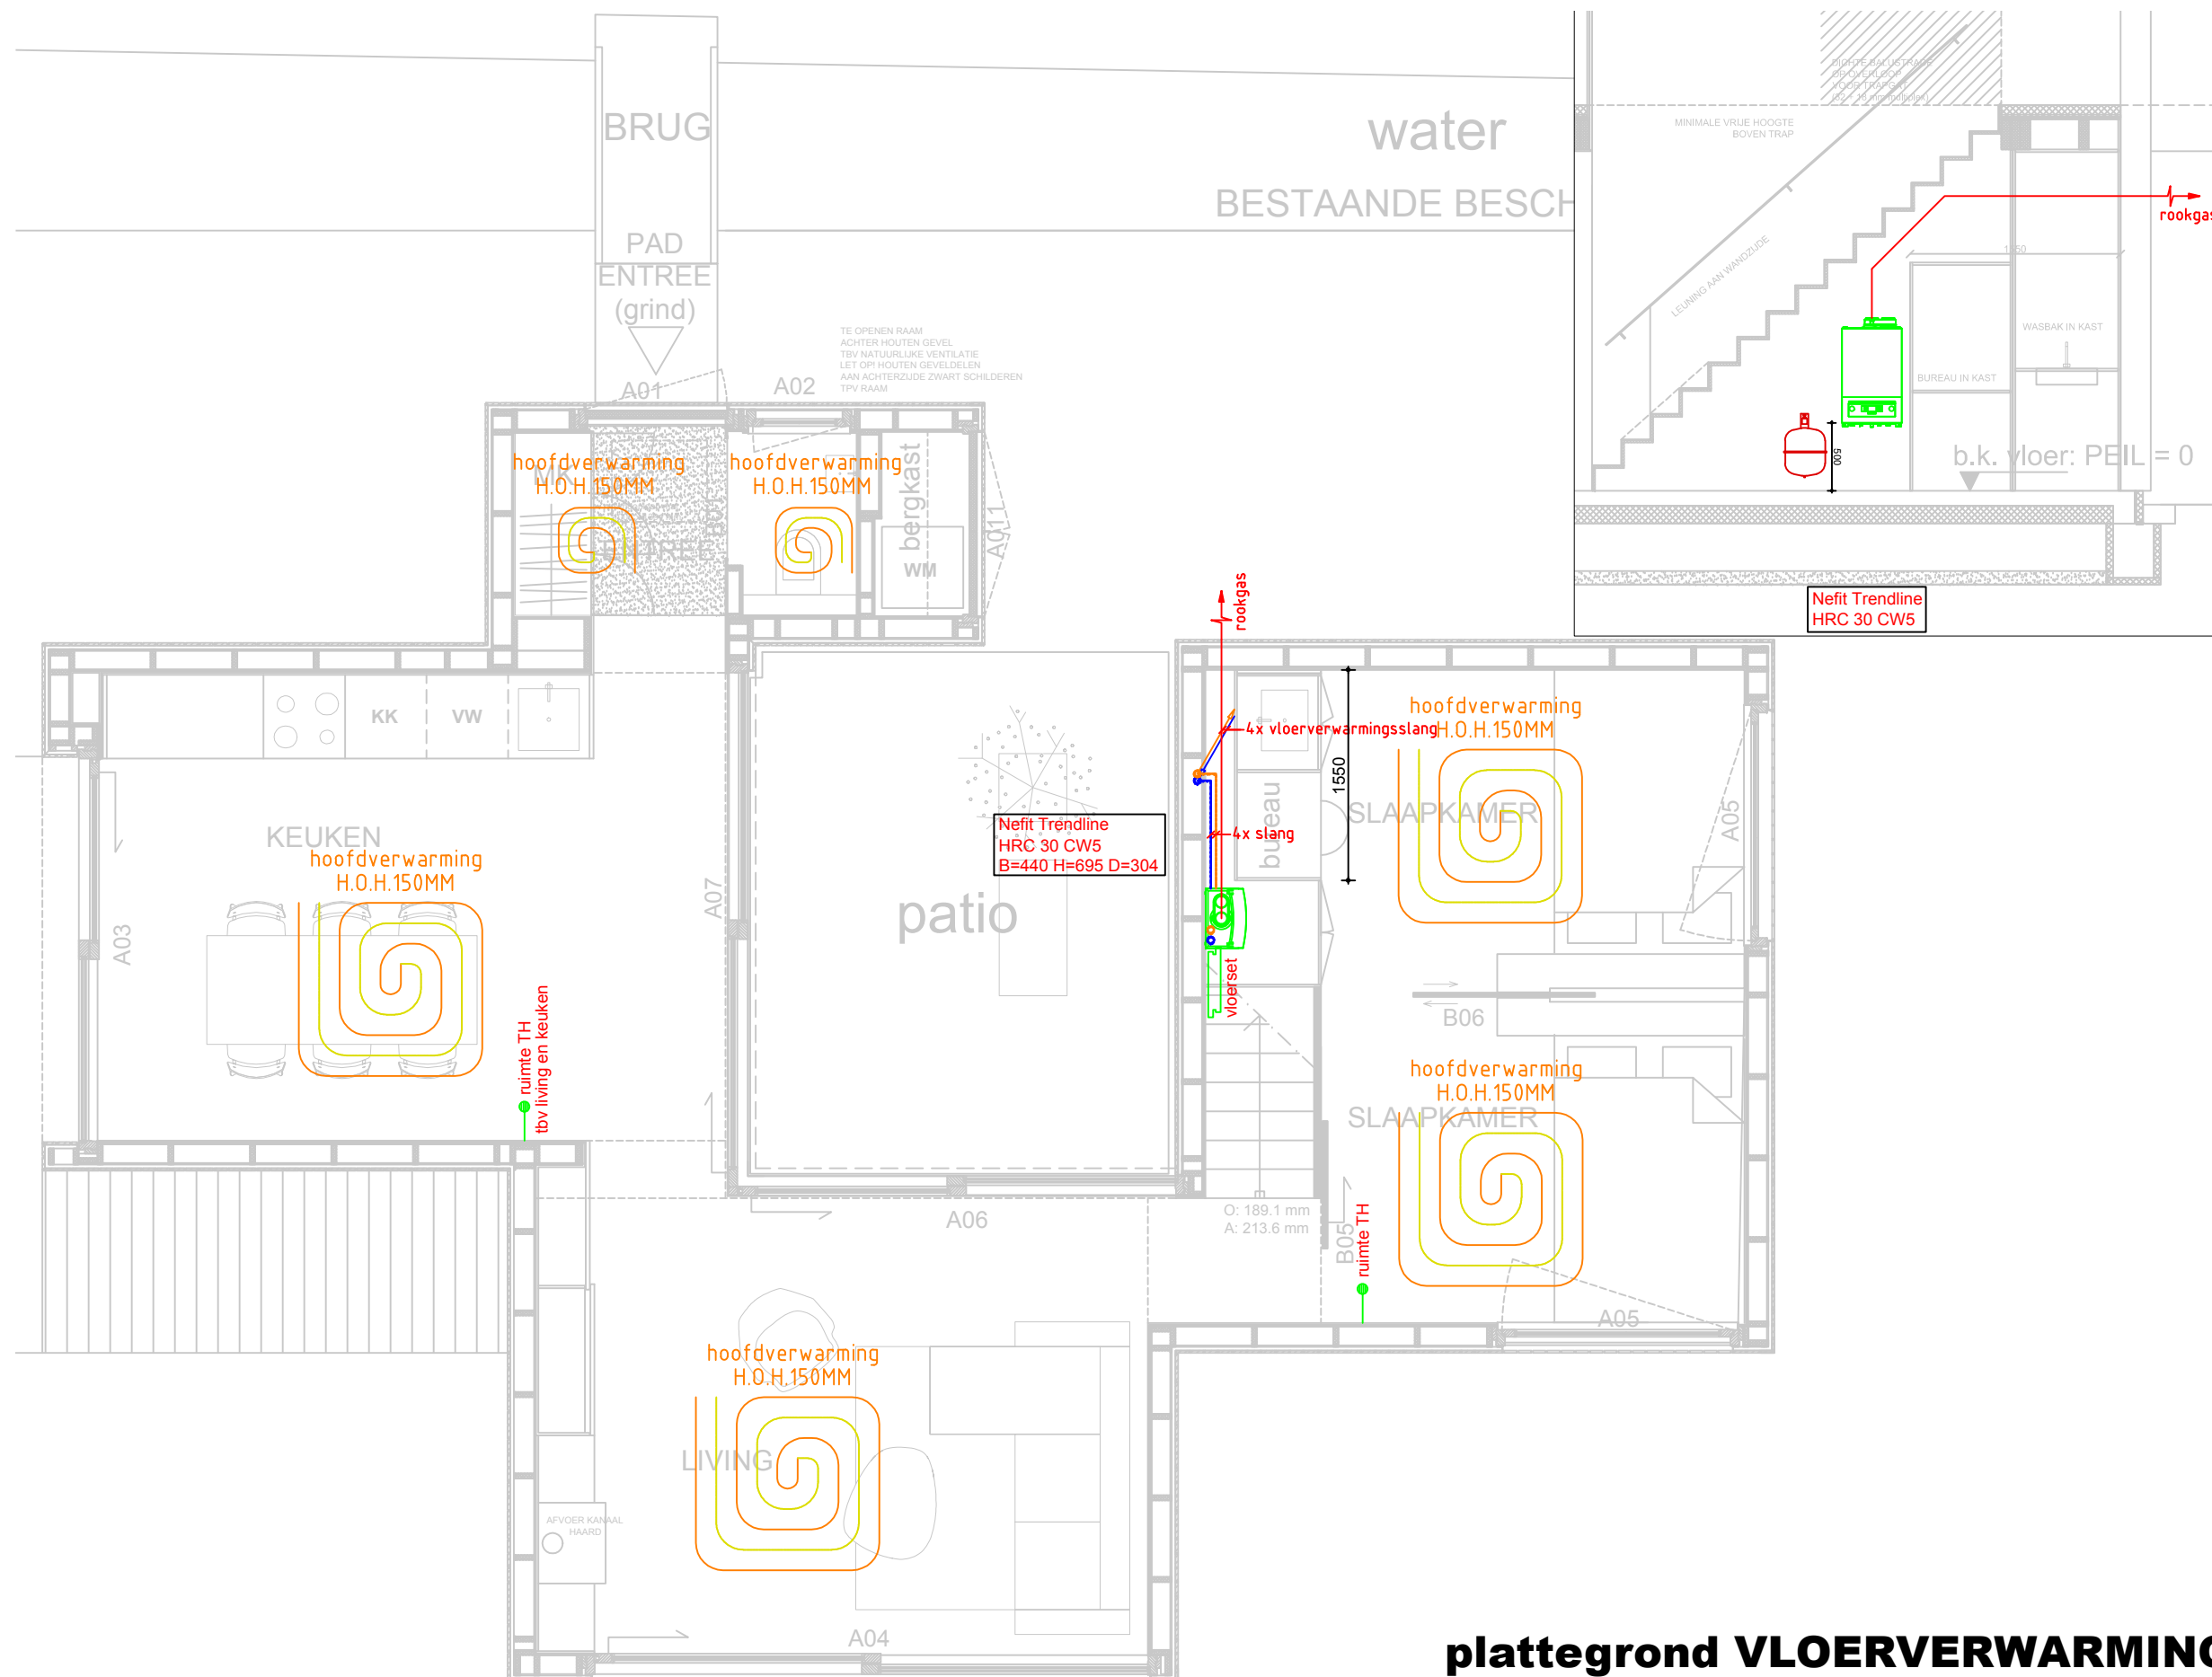


plattegrond VLOERVERWARMING
begane grond
BLAD 14
Examenadviesburo 2112.8428

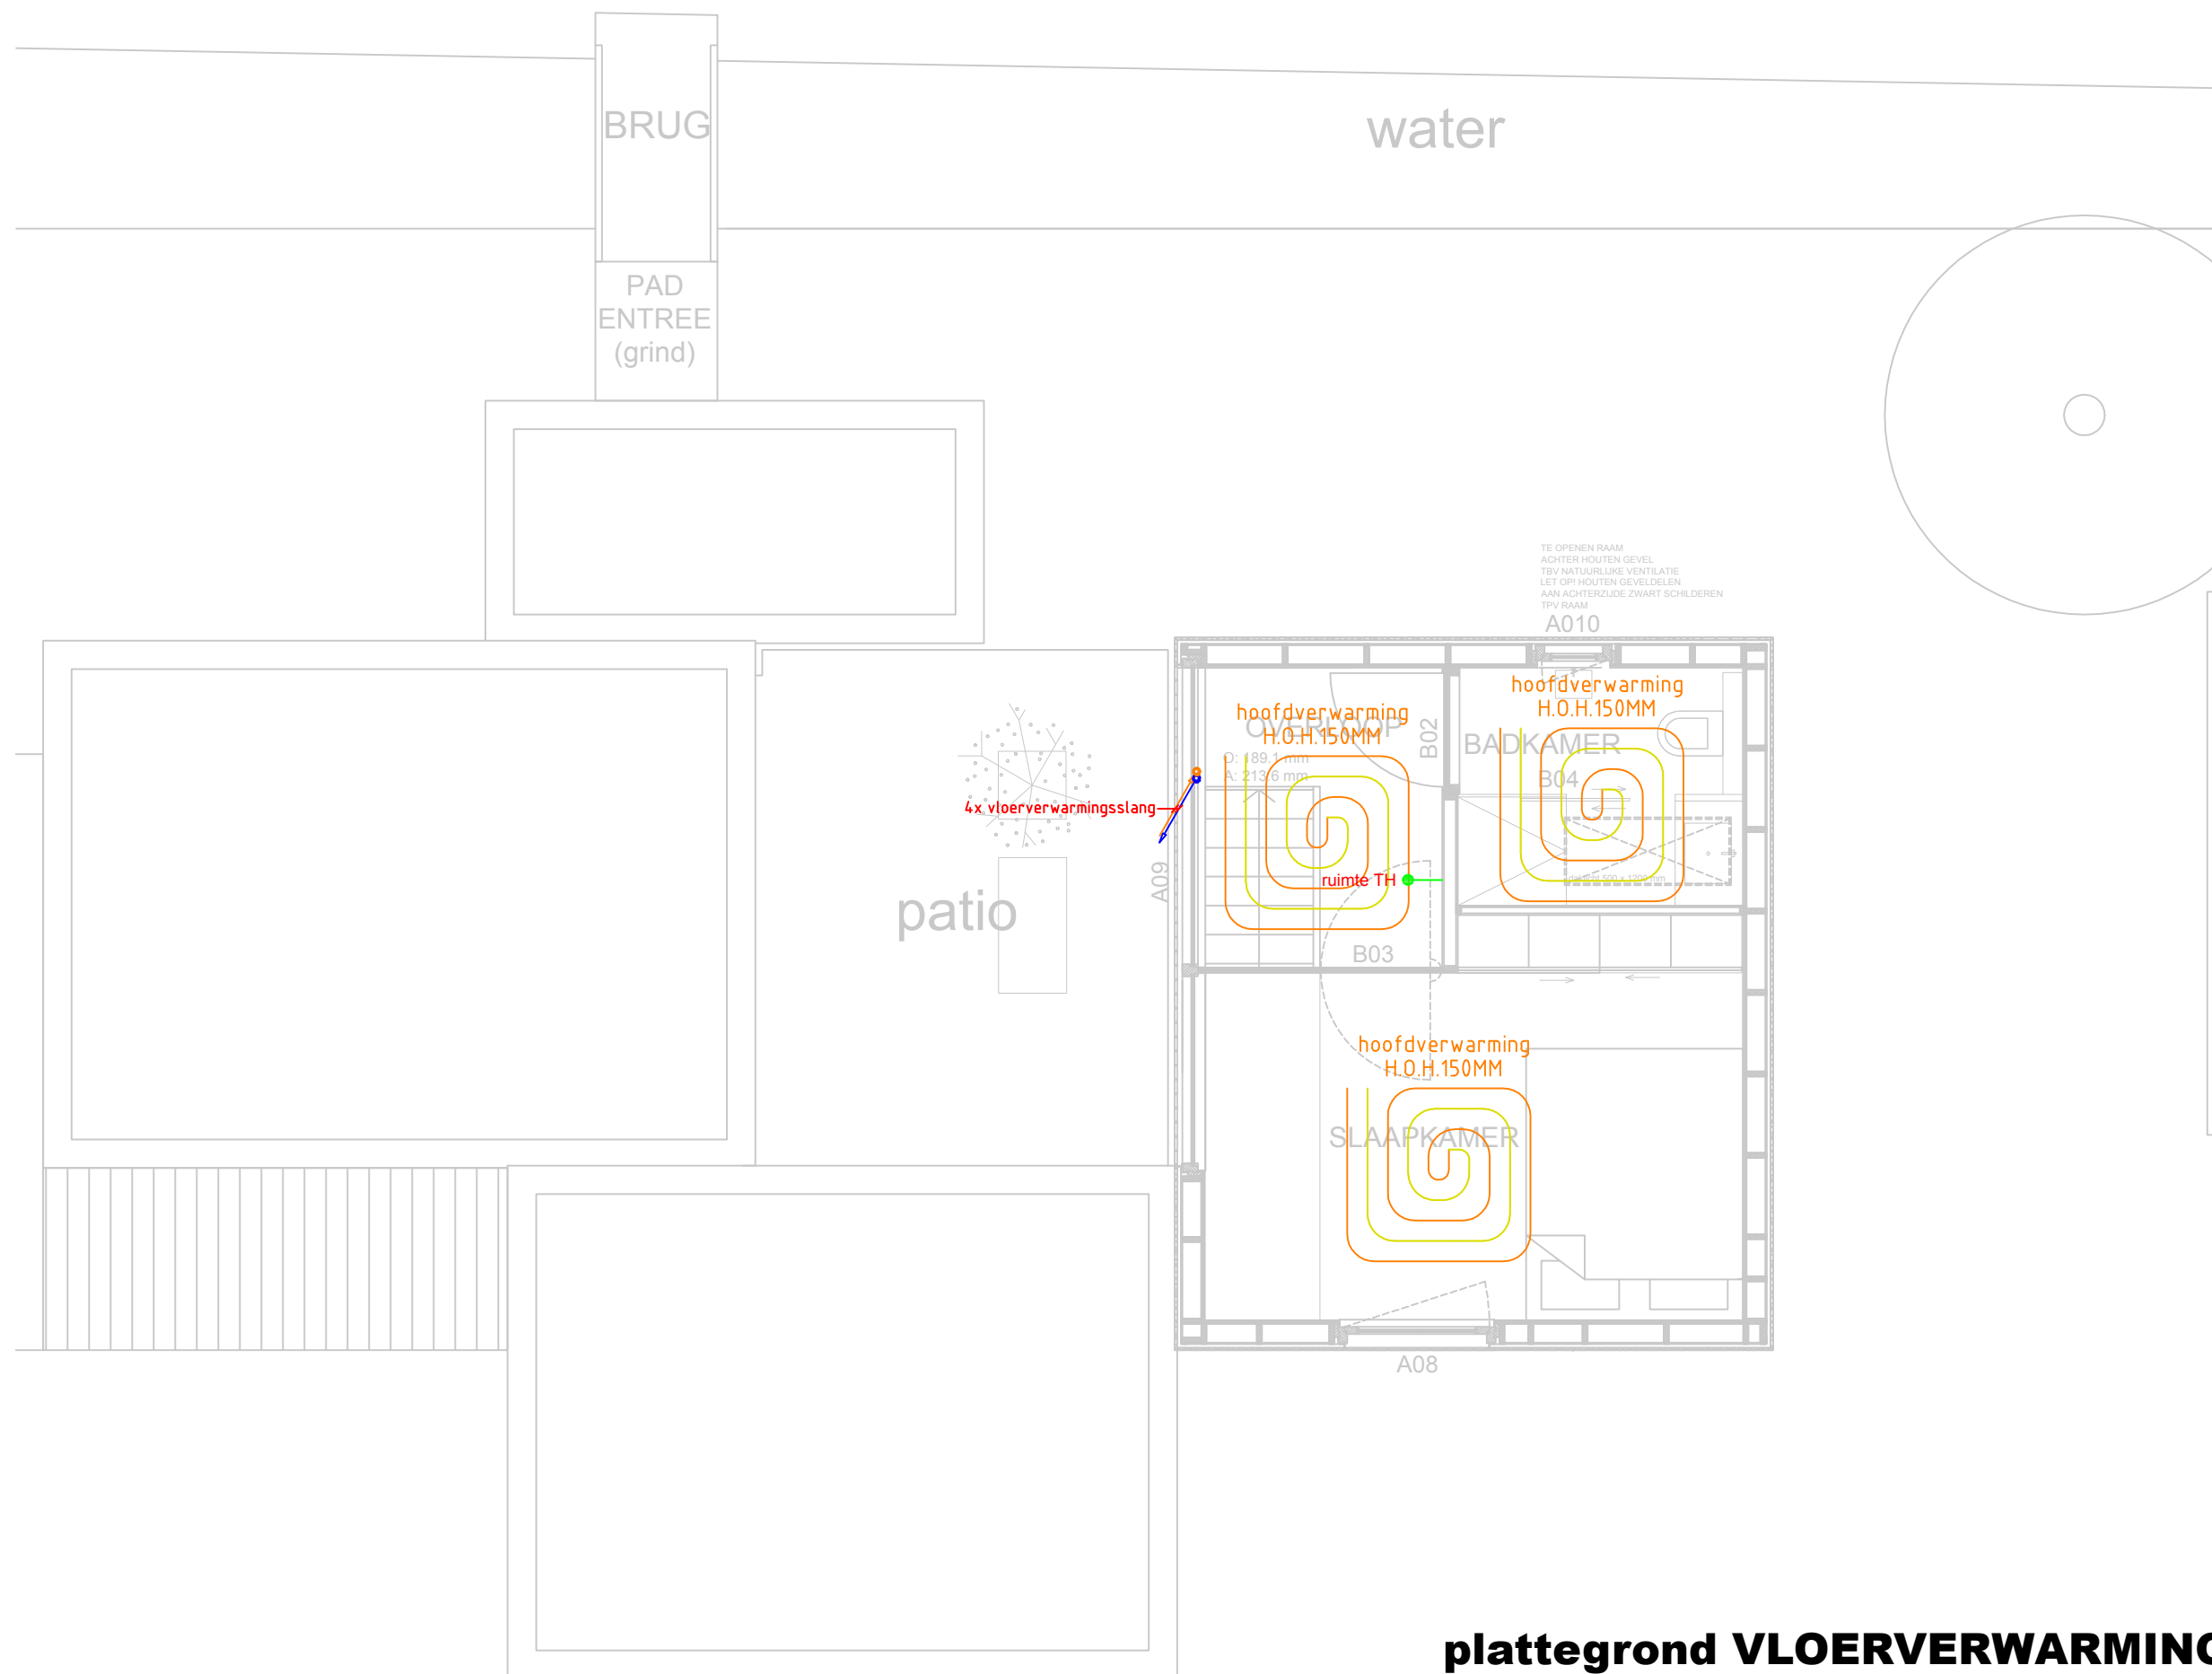




doorsnede D 1.1

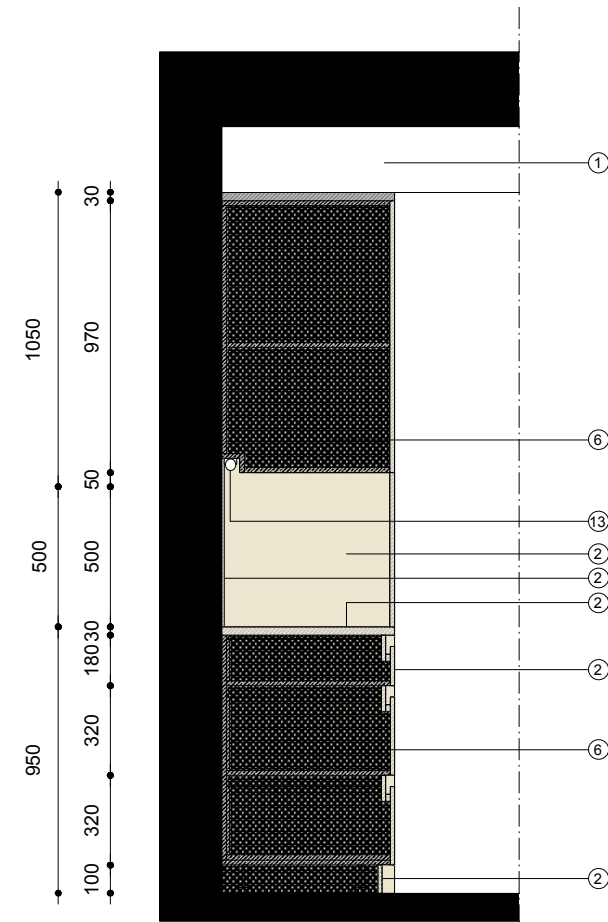

doorsnede D-1.2

300

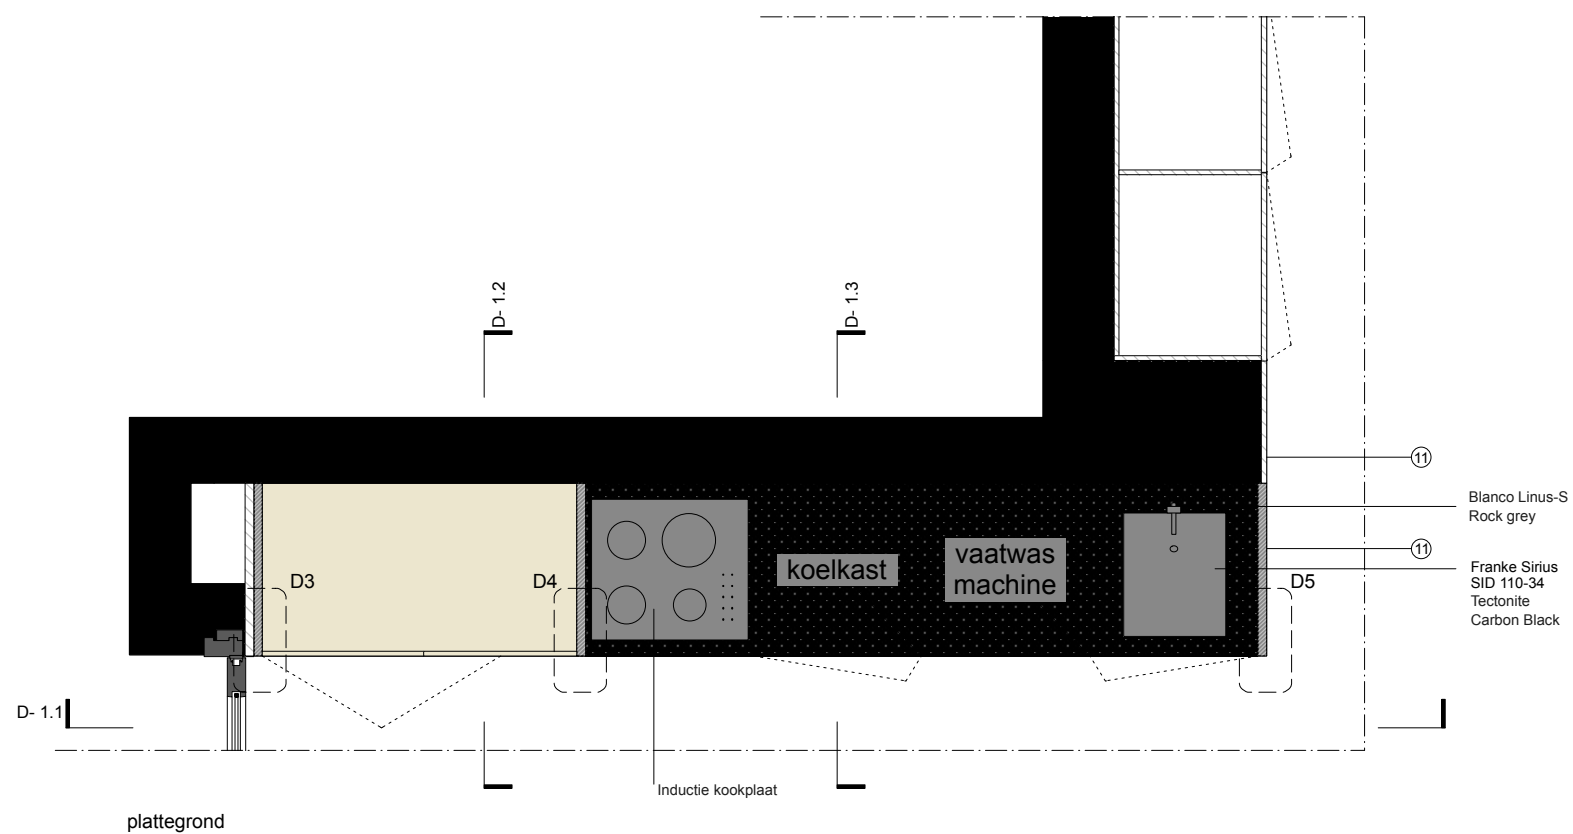

D- 1.1

plattegrond


Inductie kookplaat

koelkast

vaatwas machine


Blanco Linus-S
Rock grey

Franke Sirius
SID 110-34
Tectonite
Carbon Black

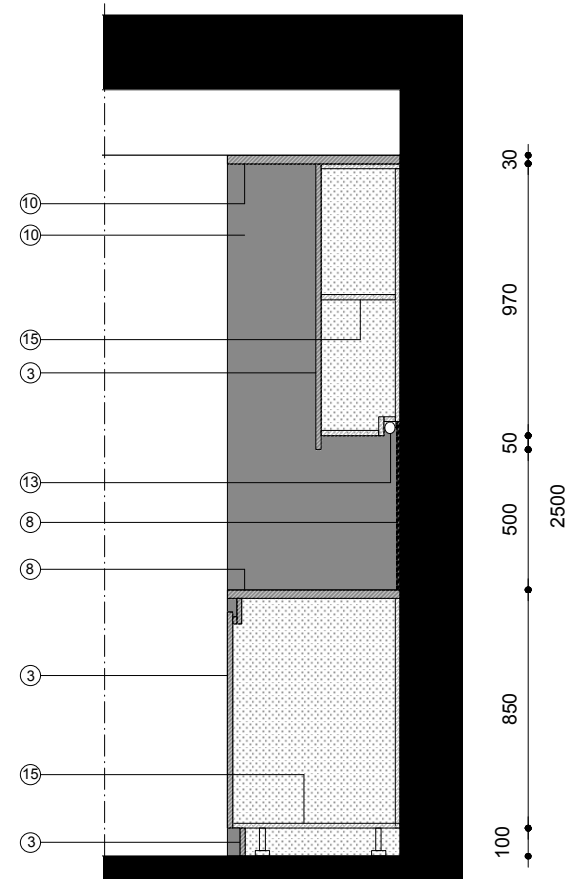

doorsnede D-1.3

uitwerking **KEUKEN**
begane grond
BLAD 16
Examenadviesburo 2112.8428

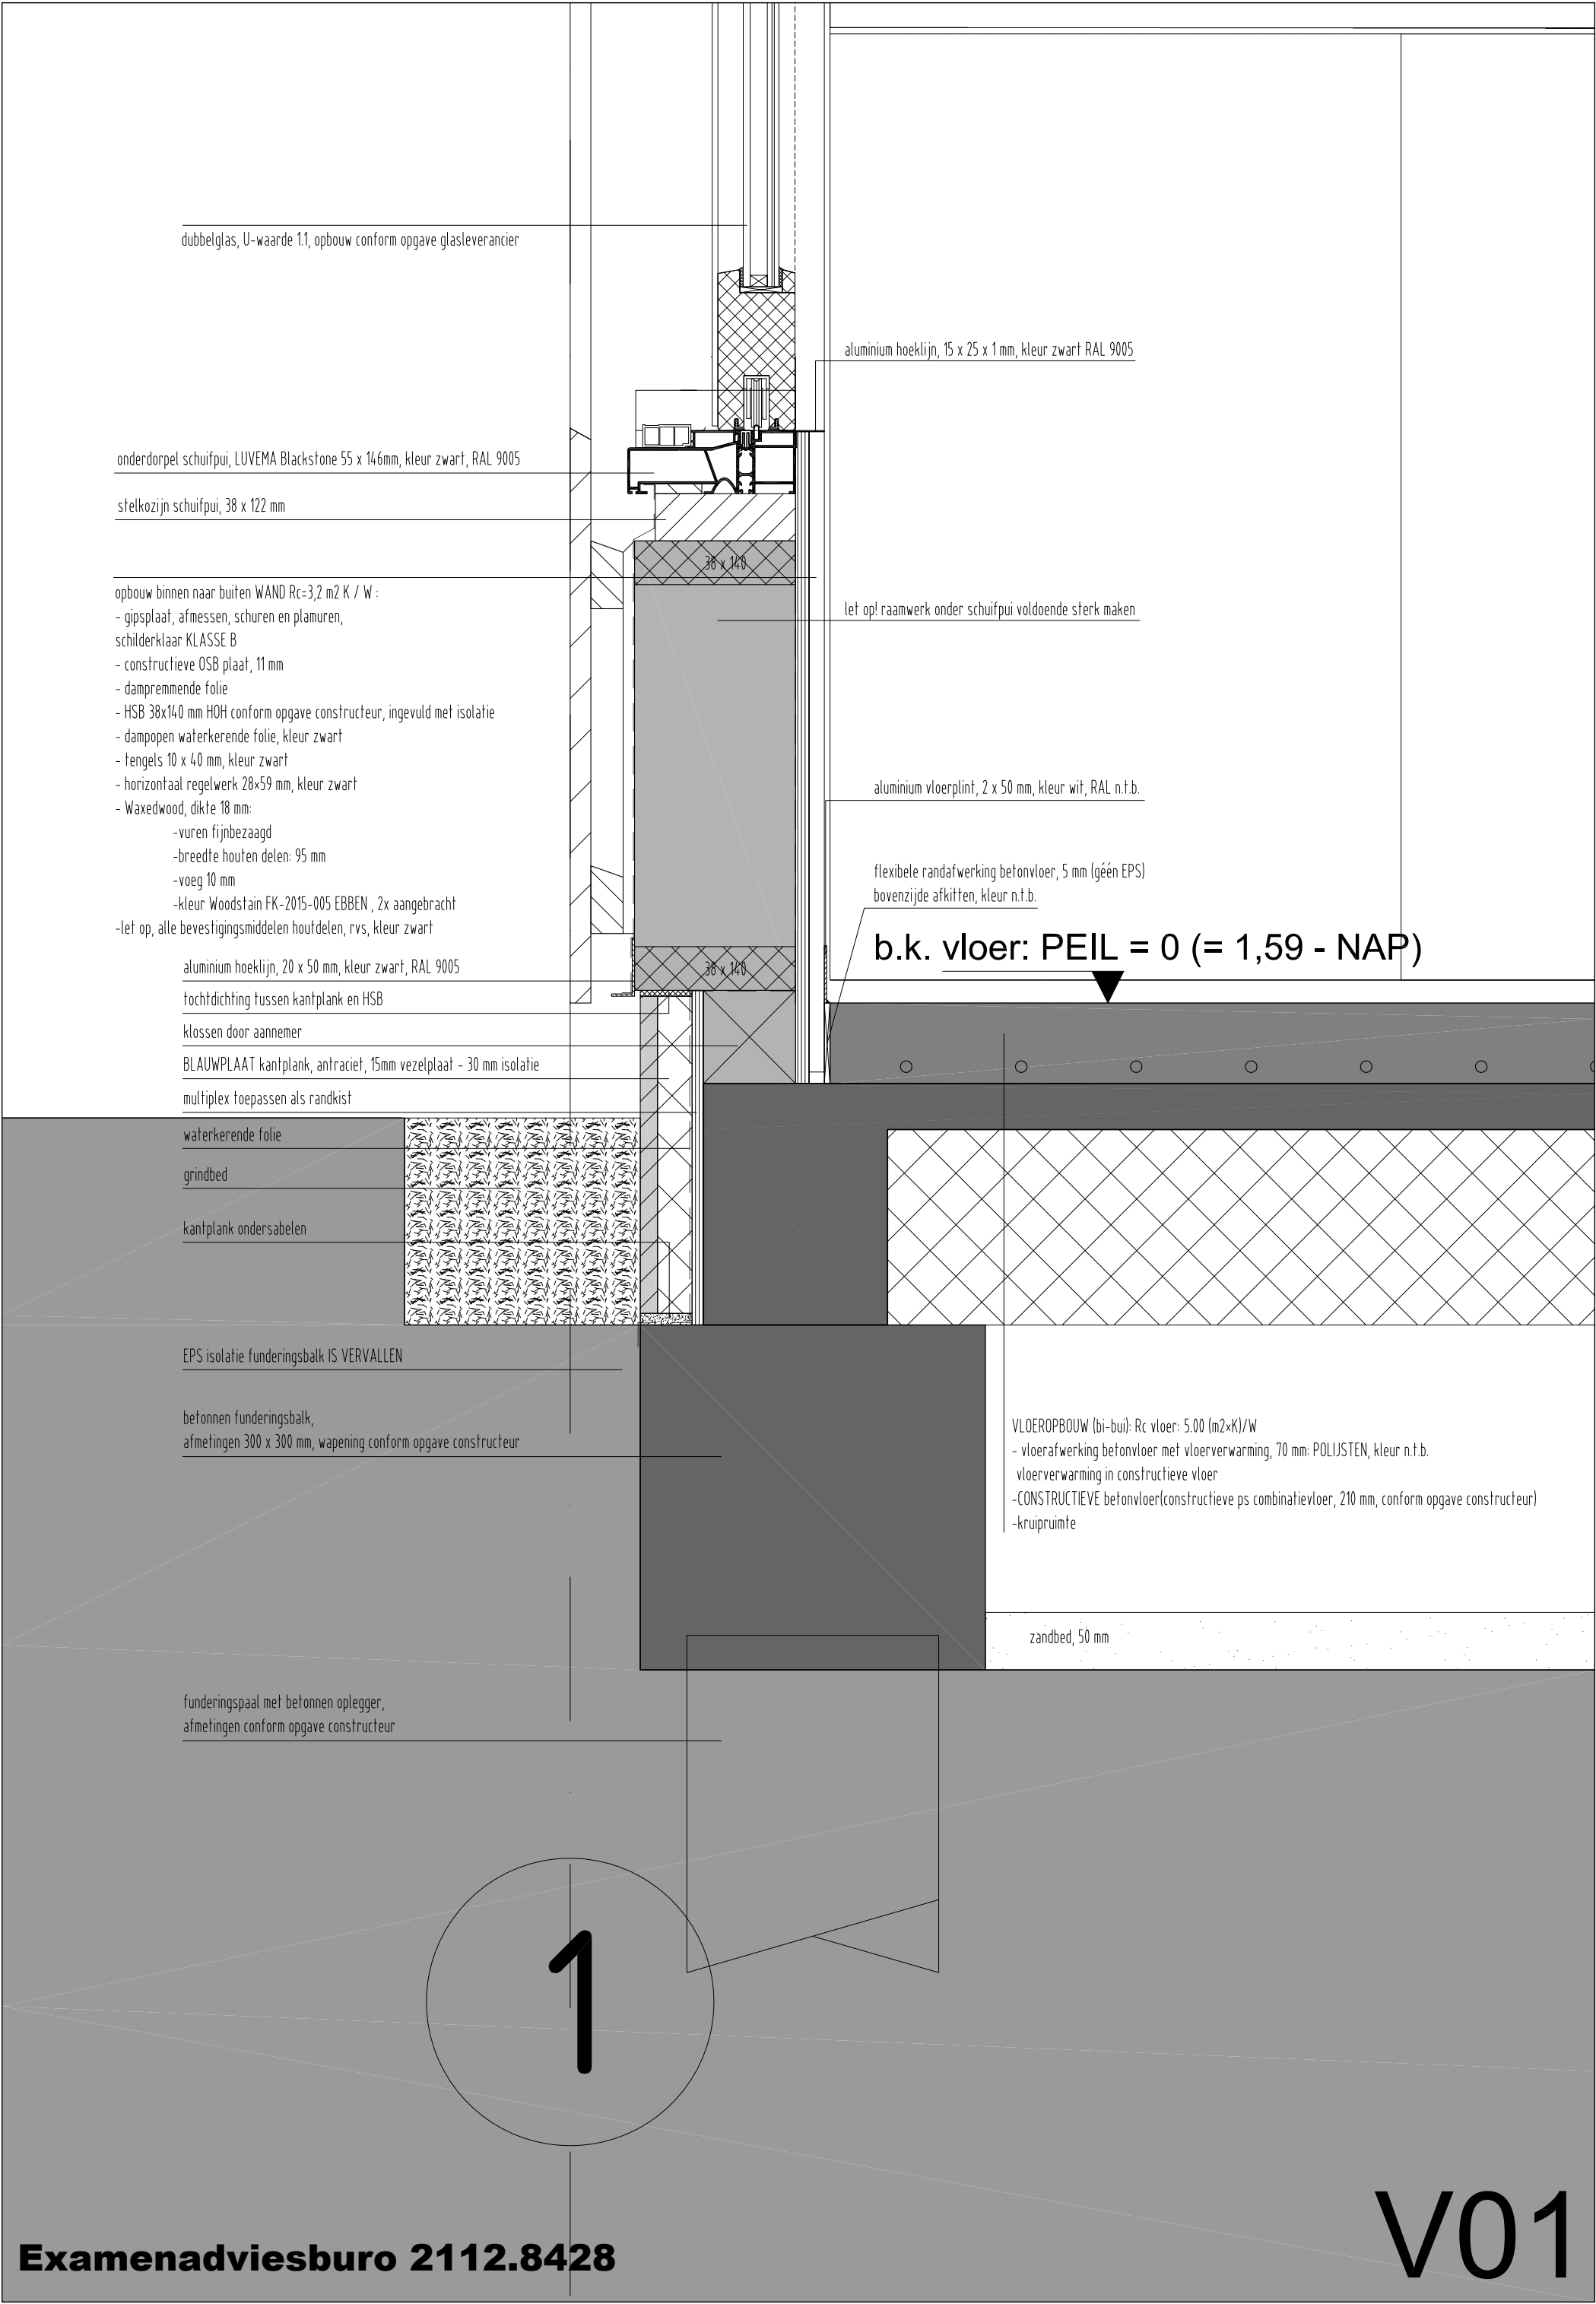

1

- Dakopbouw (binnen-buiten) Rc=6,0 m2 K / W :
- zone vloerbalken, (71 x 196 mm HOH 600, conform opgave constructeur)
 - vuren vloerdelen, 18 mm
 - hoogwaardige isolatieplaat, minimaal 140 mm dik (afschot dak in isolatieplaat)
 - dakbedekking (kleur zwart)
 - mos-sedum op substraatlaag

b.k. dakrand: 3800 + P

- opbouw binnen naar buiten WAND Rc=3,2 m2 K / W :
- gipsplaat, afmetten, schuren en plamuren, schilderklaar KLASSE B
 - constructieve OSB plaat, 11 mm
 - dampremmende folie
 - HSB 38x140 mm HOH conform opgave constructeur, ingevuld met isolatie
 - dampopen waterkerende folie, kleur zwart
 - fengels 10 x 40 mm, kleur zwart
 - horizontaal regelwerk 28x59 mm, kleur zwart
 - Waxedwood, dikte 18 mm:
 - vuren fijnbezaagd
 - breedte houten delen: 95 mm
 - voeg 10 mm
 - kleur Woodstain FK-2015-005 EBBEN , 2x aangebracht
 - let op, alle bevestigingsmiddelen houtdelen, rvs, kleur zwart

o.k. plafond: 3533 + P

2 x 71x246 mm, 2 mm geschaafd, constructieve balk boven kozijn

bovendorpel schuifpui, hout, 67 x 139 mm, kleur zwart, RAL 9005

o.k. geveldelen: 2500 + P

aluminium hoeklijn, 20 x 50 mm, kleur zwart, RAL 9005

dubbelglas, U-waarde 1.1, opbouw conform opgave glasleverancier

stelkozijn schuifpui, 38 x 74 mm
aluminium hoeklijn, 15 x 25 x 1 mm, kleur zwart RAL 9005

- Dakopbouw (binnen-buiten) Rc=6,0 m2 K / W :
- zone vloerbalken, (71 x 196 mm HOH 600, conform opgave constructeur)
 - vuren vloerdelen, 18 mm
 - hoogwaardige isolatieplaat, minimaal 140 mm dik (afschot dak in isolatieplaat)
 - dakbedekking (kleur zwart)
 - mos-sedum op substraatlaag

multiplex WPB plaat, 25 mm
dakbedekking, kleur zwart
aluminium daktrim, kleur zwart, RAL 9005

b.k. dakrand: 3800 + P

o.k. plafond: 3533 + P

- opbouw binnen naar buiten WAND Rc=3,2 m2 K / W :
- gipsplaat, afmessen, schuren en plamuren, schilderklaar KLASSE B
 - constructieve OSB plaat, 11 mm
 - dampremmende folie
 - HSB 38x140 mm HOH conform opgave constructeur, ingevuld met isolatie
 - dampopen waterkerende folie, kleur zwart
 - tengels 10 x 40 mm, kleur zwart
 - horizontaal regelwerk 28x59 mm, kleur zwart
 - Waxedwood, dikte 18 mm:
 - vuren fijnbezaagd
 - breedte houten delen: 95 mm
 - voeg 10 mm
 - kleur 'Woodstain FK-2015-005 EBBEN', 2x aangebracht
 - let op, alle bevestigingsmiddelen houtdelen, rvs, kleur zwart


2 x 71x246 mm, 2 mm geschaafd, constructieve balk boven kozijn


stelkozijn schuifpui, 38 x 74 mm
bovendorpel schuifpui, hout, 67 x 139 mm, kleur zwart, RAL 9005
aluminium hoeklijn, 15 x 25 x 1 mm, kleur zwart RAL 9005

aluminium hoeklijn, 20 x 50 mm, kleur zwart, RAL 9005

o.k. geveldelen: 2500 + P

dubbelglas, U-waarde 1,1, opbouw conform opgave glasleverancier

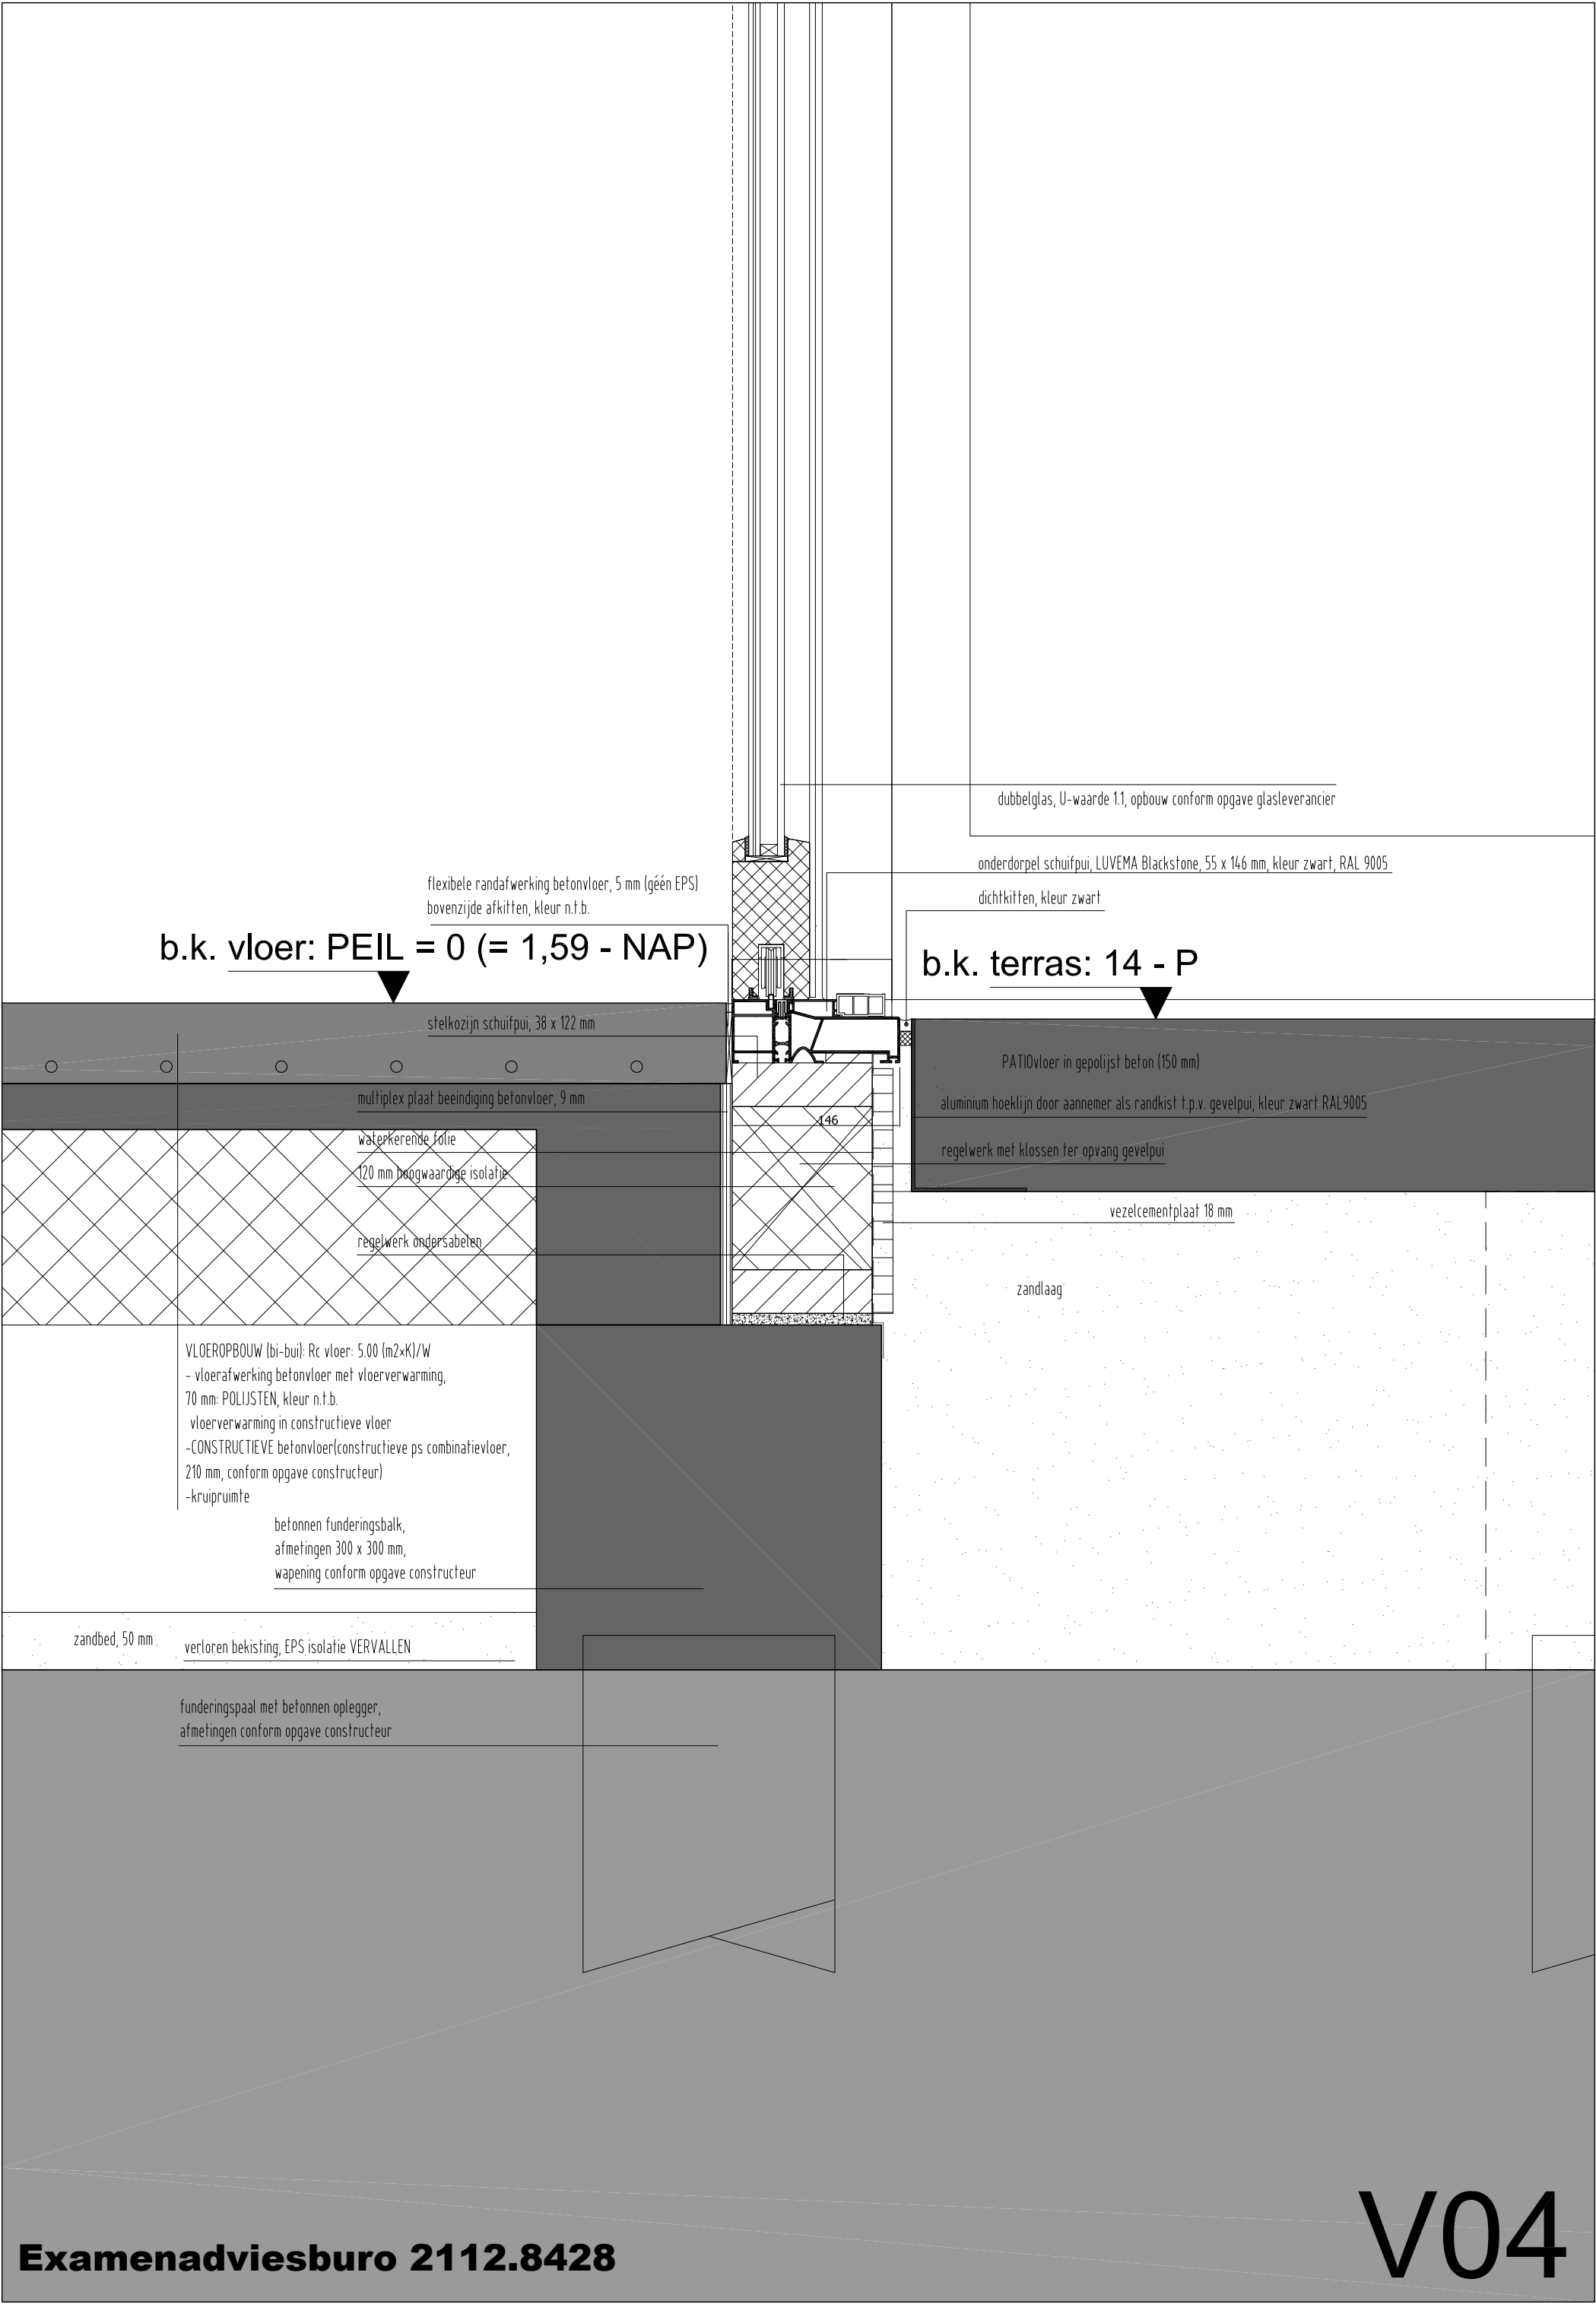

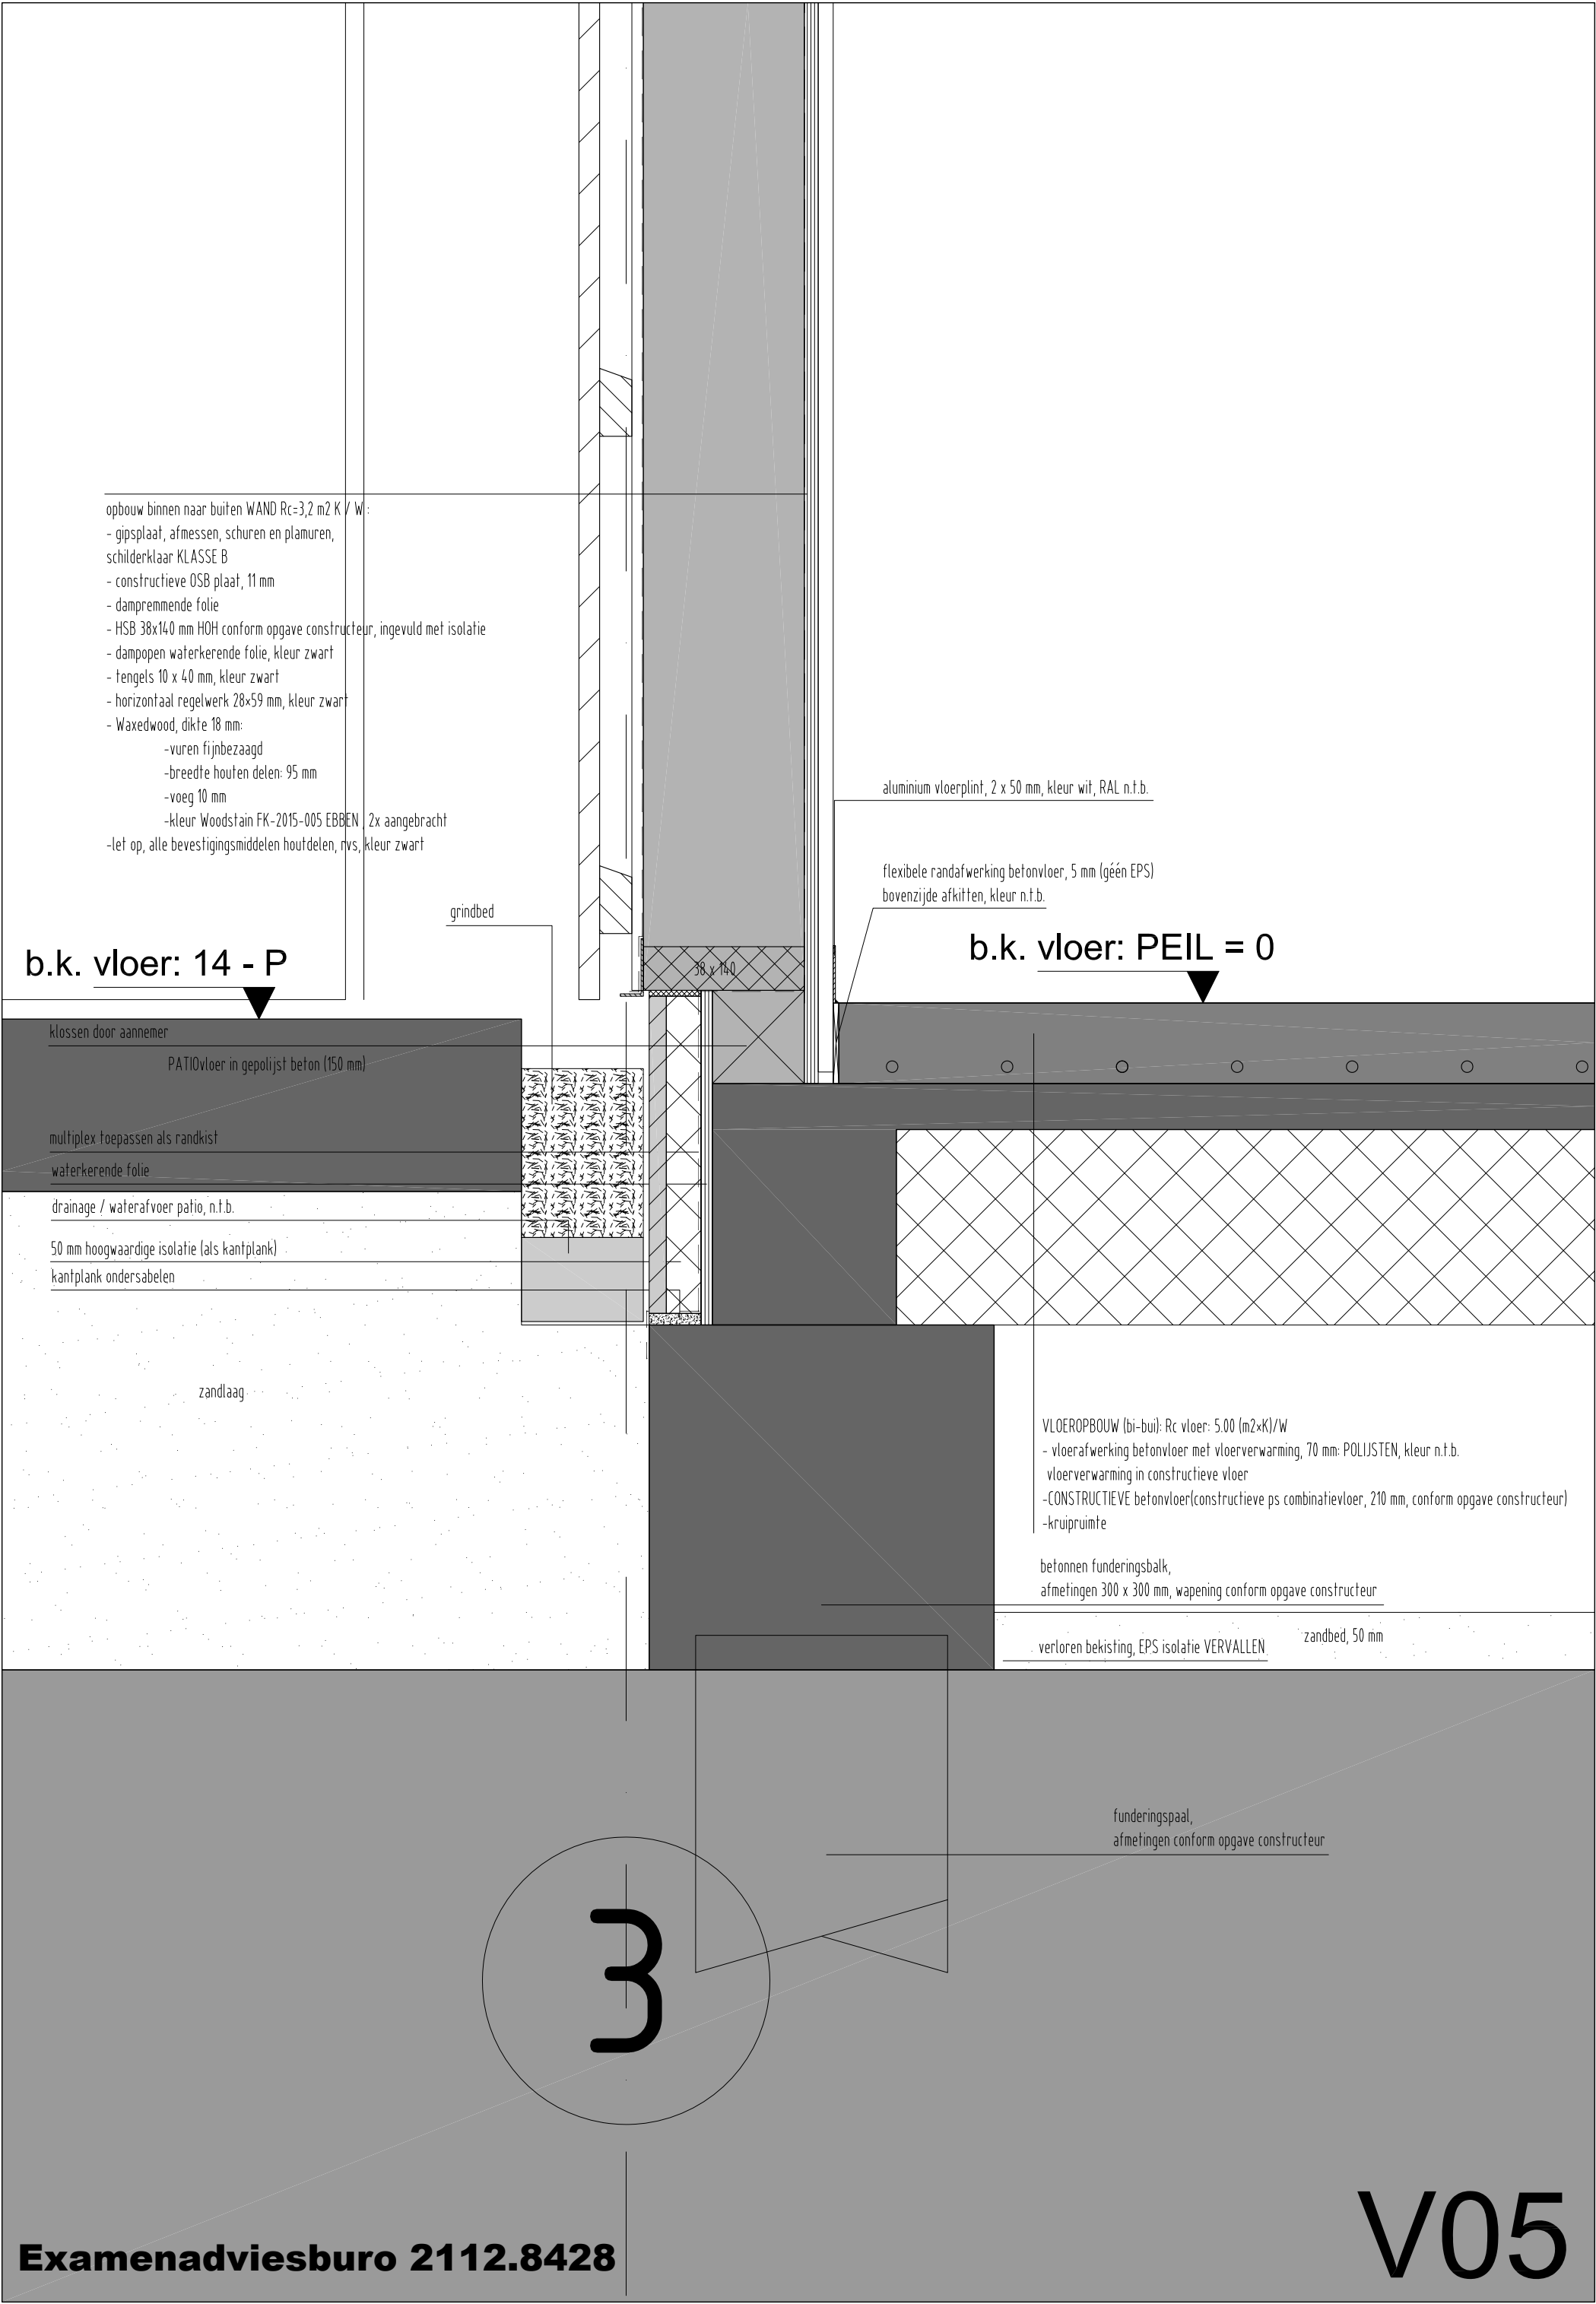

opbouw binnen naar buiten WAND Rc=3,2 m2 K / W:

- gipsplaat, afmessen, schuren en plamuren, schilderklaar KLASSE B
- constructieve OSB plaat, 11 mm
- dampremmende folie
- HSB 38x140 mm HOH conform opgave constructeur, ingevuld met isolatie
- dampopen waterkerende folie, kleur zwart
- tengels 10 x 40 mm, kleur zwart
- horizontaal regelwerk 28x59 mm, kleur zwart
- Waxewood, dikte 18 mm:
 - vuren fijnbezaagd
 - breedte houten delen: 95 mm
 - voeg 10 mm
 - kleur Woodstain FK-2015-005 EBBEN, 2x aangebracht
- let op, alle bevestigingsmiddelen houtdelen, nvs, kleur zwart

aluminium vloerplint, 2 x 50 mm, kleur wit, RAL n.t.b.

flexibele randafwerking betonvloer, 5 mm (géén EPS)
bovenzijde afkitten, kleur n.t.b.

b.k. vloer: 14 - P

b.k. vloer: PEIL = 0

klossen door aannemer

PATIOvloer in gepolijst beton (150 mm)

multiplex toepassen als randkist

waterkerende folie

drainage / waterafvoer patio, n.t.b.

50 mm hoogwaardige isolatie (als kantplank)

kantplank ondersabelen

zandlaag

VLOEROPBOUW (bi-bui): Rc vloer: 5.00 (m2xK)/W

- vloerafwerking betonvloer met vloerverwarming, 70 mm: POLIJSTEN, kleur n.t.b.
- vloerverwarming in constructieve vloer
- CONSTRUCTIEVE betonvloer (constructieve ps combinatievloer, 210 mm, conform opgave constructeur)
- kruipruimte

betonnen funderingsbalk,
afmetingen 300 x 300 mm, wapening conform opgave constructeur

verloren bekisting, EPS isolatie VERVALLEN

zandbed, 50 mm

funderingspaal,
afmetingen conform opgave constructeur

3

D

- opbouw binnen naar buiten WAND Rc=3,2 m2 K / W :
- gipsplaat, afmetten, schuren en plamuren, schilderklaar KLASSE B
 - constructieve OSB plaat, 11 mm
 - dampremmende folie
 - HSB 38x140 mm HOH conform opgave constructeur, ingevuld met isolatie
 - dampopen waterkerende folie, kleur zwart
 - tengels 10 x 40 mm, kleur zwart
 - horizontaal regelwerk 28x59 mm, kleur zwart
 - Waxedwood, dikte 18 mm:
 - vuren fijnbezaagd
 - breedte houten delen n.t.b.
 - voeg 10 mm
 - kleur Woodstain FK-2015-005 EBBEN , 2x aangebracht
 - let op, alle bevestigingsmiddelen houtdelen, rvs, kleur zwart

ventilatieopening minimaal 17 mm

stelkozijn, 38 x 100 mm

waterkerende folie, kleur zwart

bovendorpel kozijn, hout, 67 x 114 mm, kleur zwart, RAL 9005

o.k. gevelafwerking: 2257 + P

aluminium hoeklijn, 20 x 50 mm, kleur zwart, RAL 9005

dubbelglas, U-waarde 1.1, opbouw conform opgave glasleverancier

VLOEROPBOUW

- zwaluwstaart vloer met betonvloer (gepolijst), 85 mm
- vloerverwarming in deze vloerzone
- vuren vloerdelen, 18 mm
- zone vloerbalken, 71 x 221 mm HOH 600, conform opgave constructeur

b.k. vloer: 2837 + P

o.k. plafond: 2734 + P

2 x 71x221 mm, 2 mm geschaafd, constructieve balk boven kozijn

- gipsplaat, afmetten, schuren en plamuren, schilderklaar KLASSE B
- constructieve OSB plaat, 11 mm


aluminium hoeklijn, 15 x 15 x 2 mm, kleur zwart RAL 9005


- ventilatierooster DUCOTOP 50 ZR, kleur zwart, RAL n.t.b.

aluminium strip, 50 x 2 mm, kleur zwart RAL 9005

draaikiep deel, hout, kleur zwart, RAL 9005

aluminium strip, 65 x 2 mm, kleur zwart RAL 9005

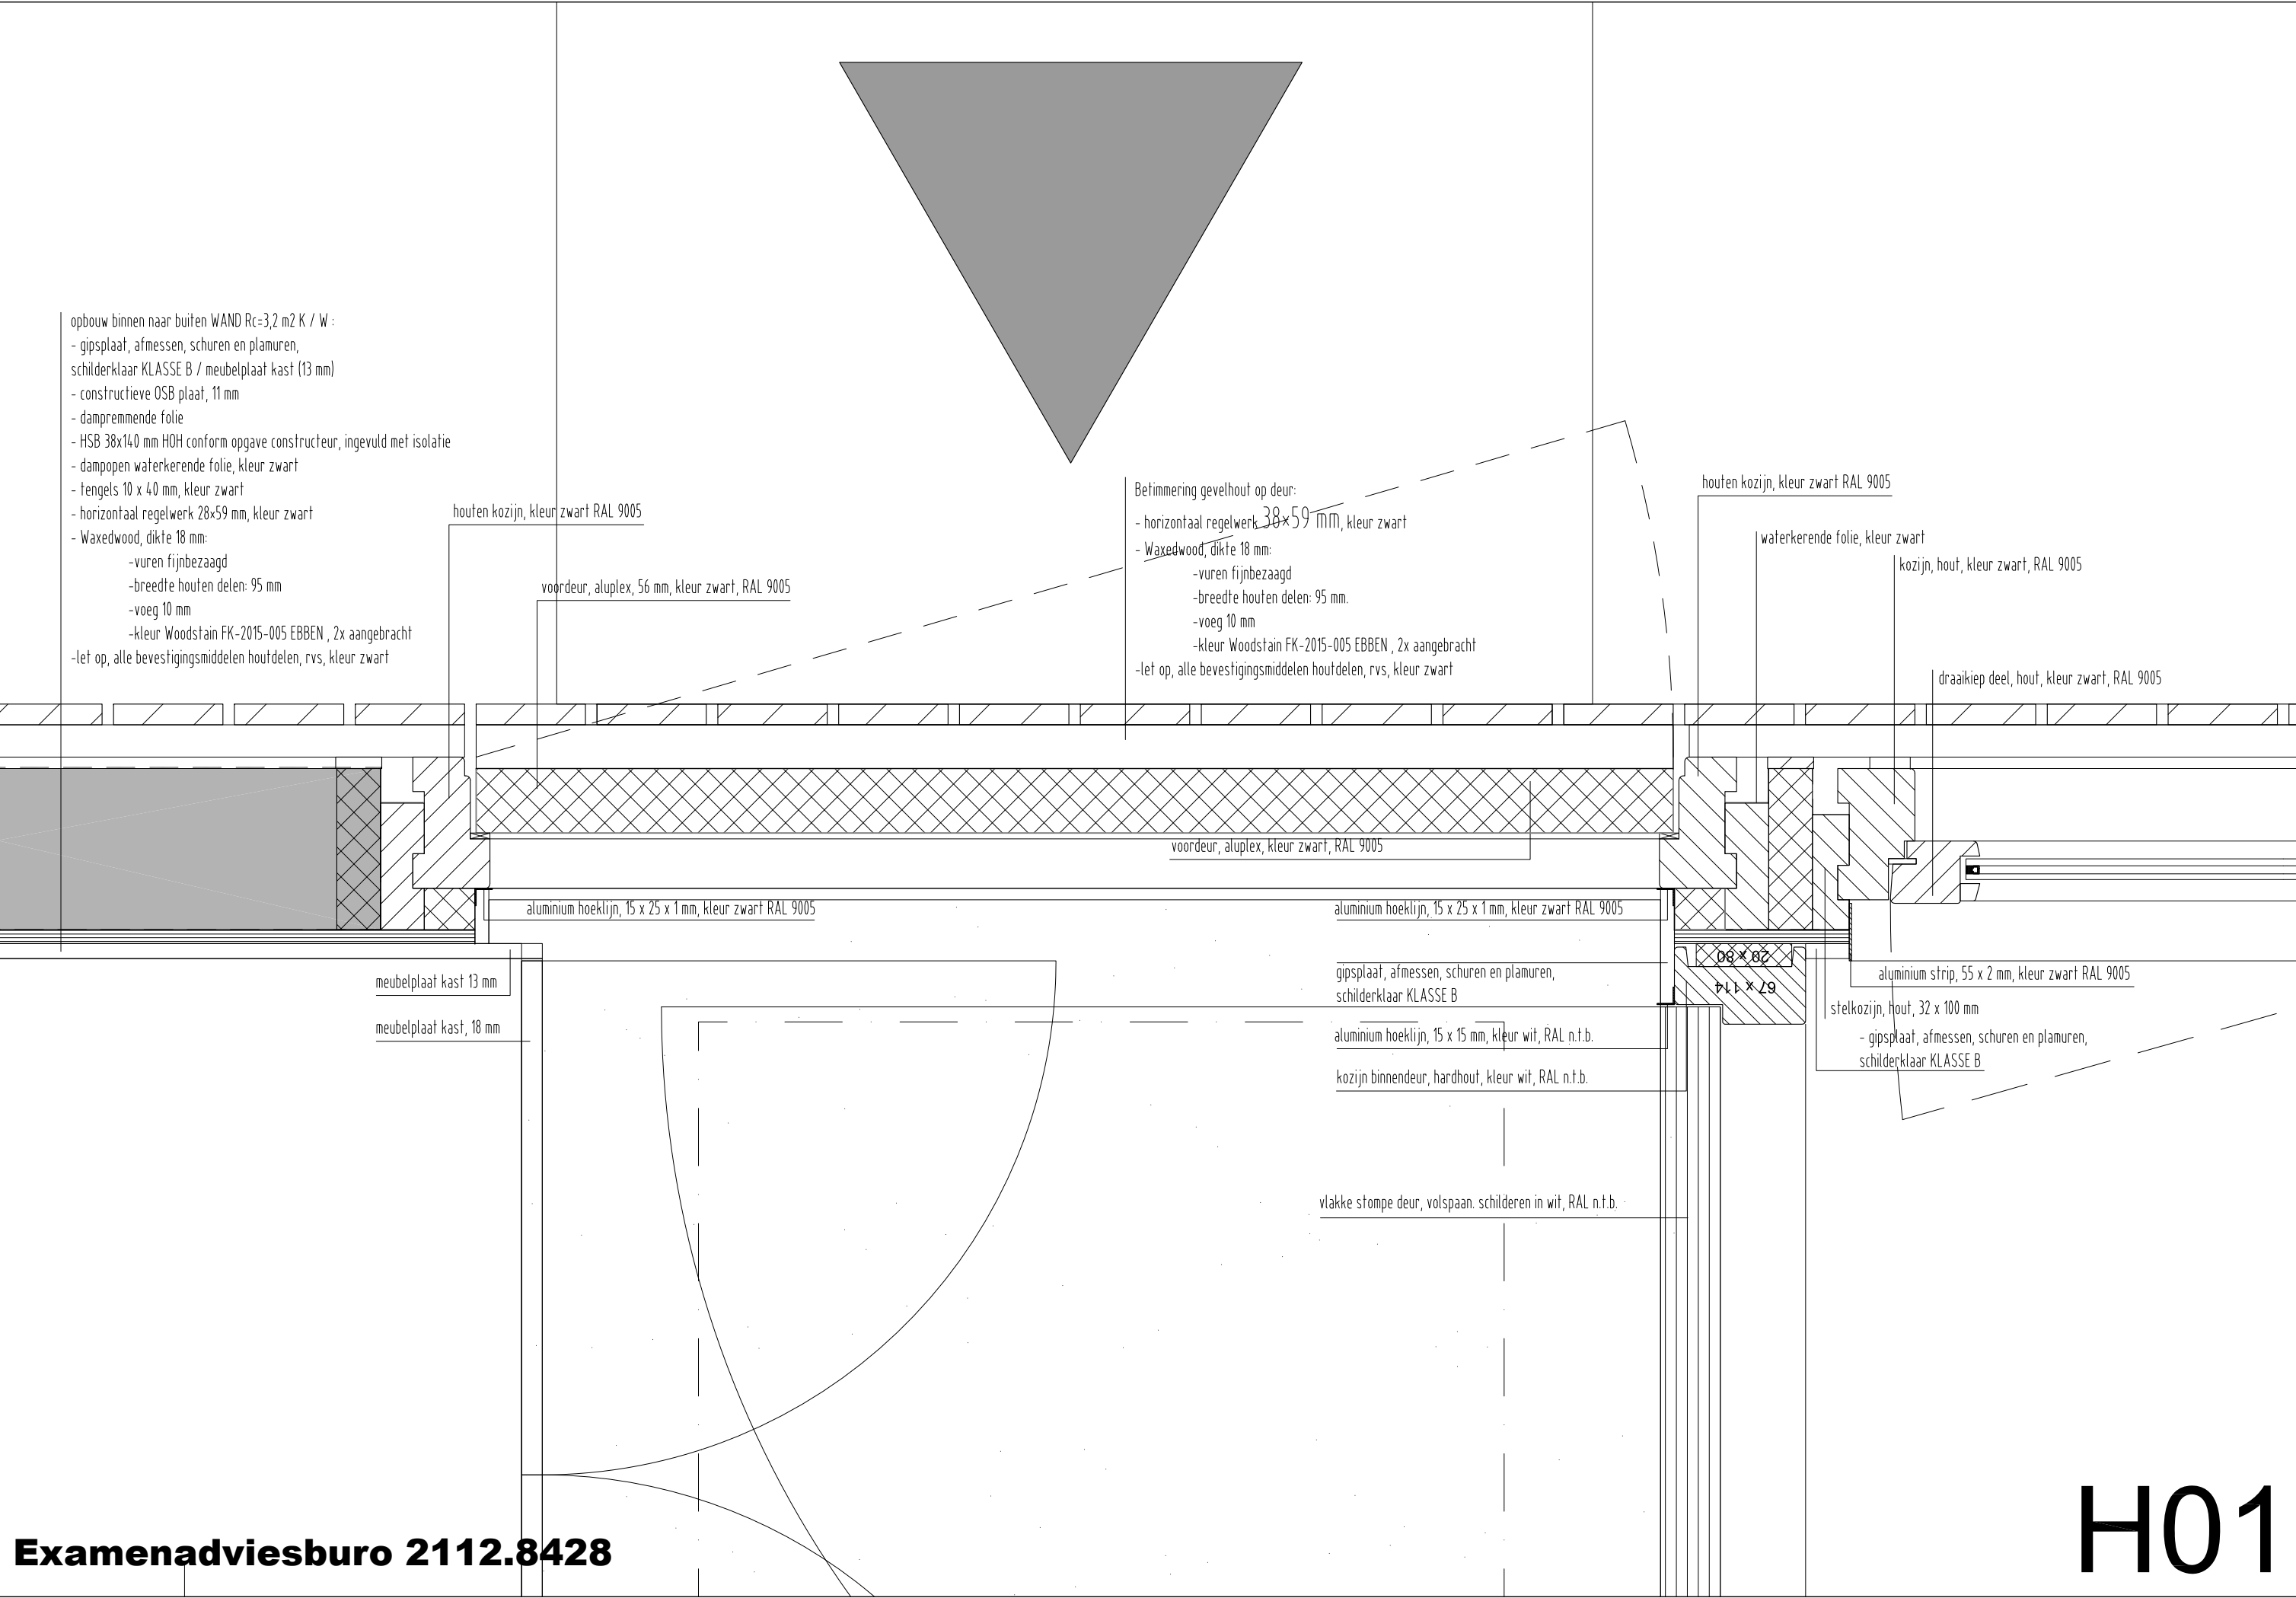

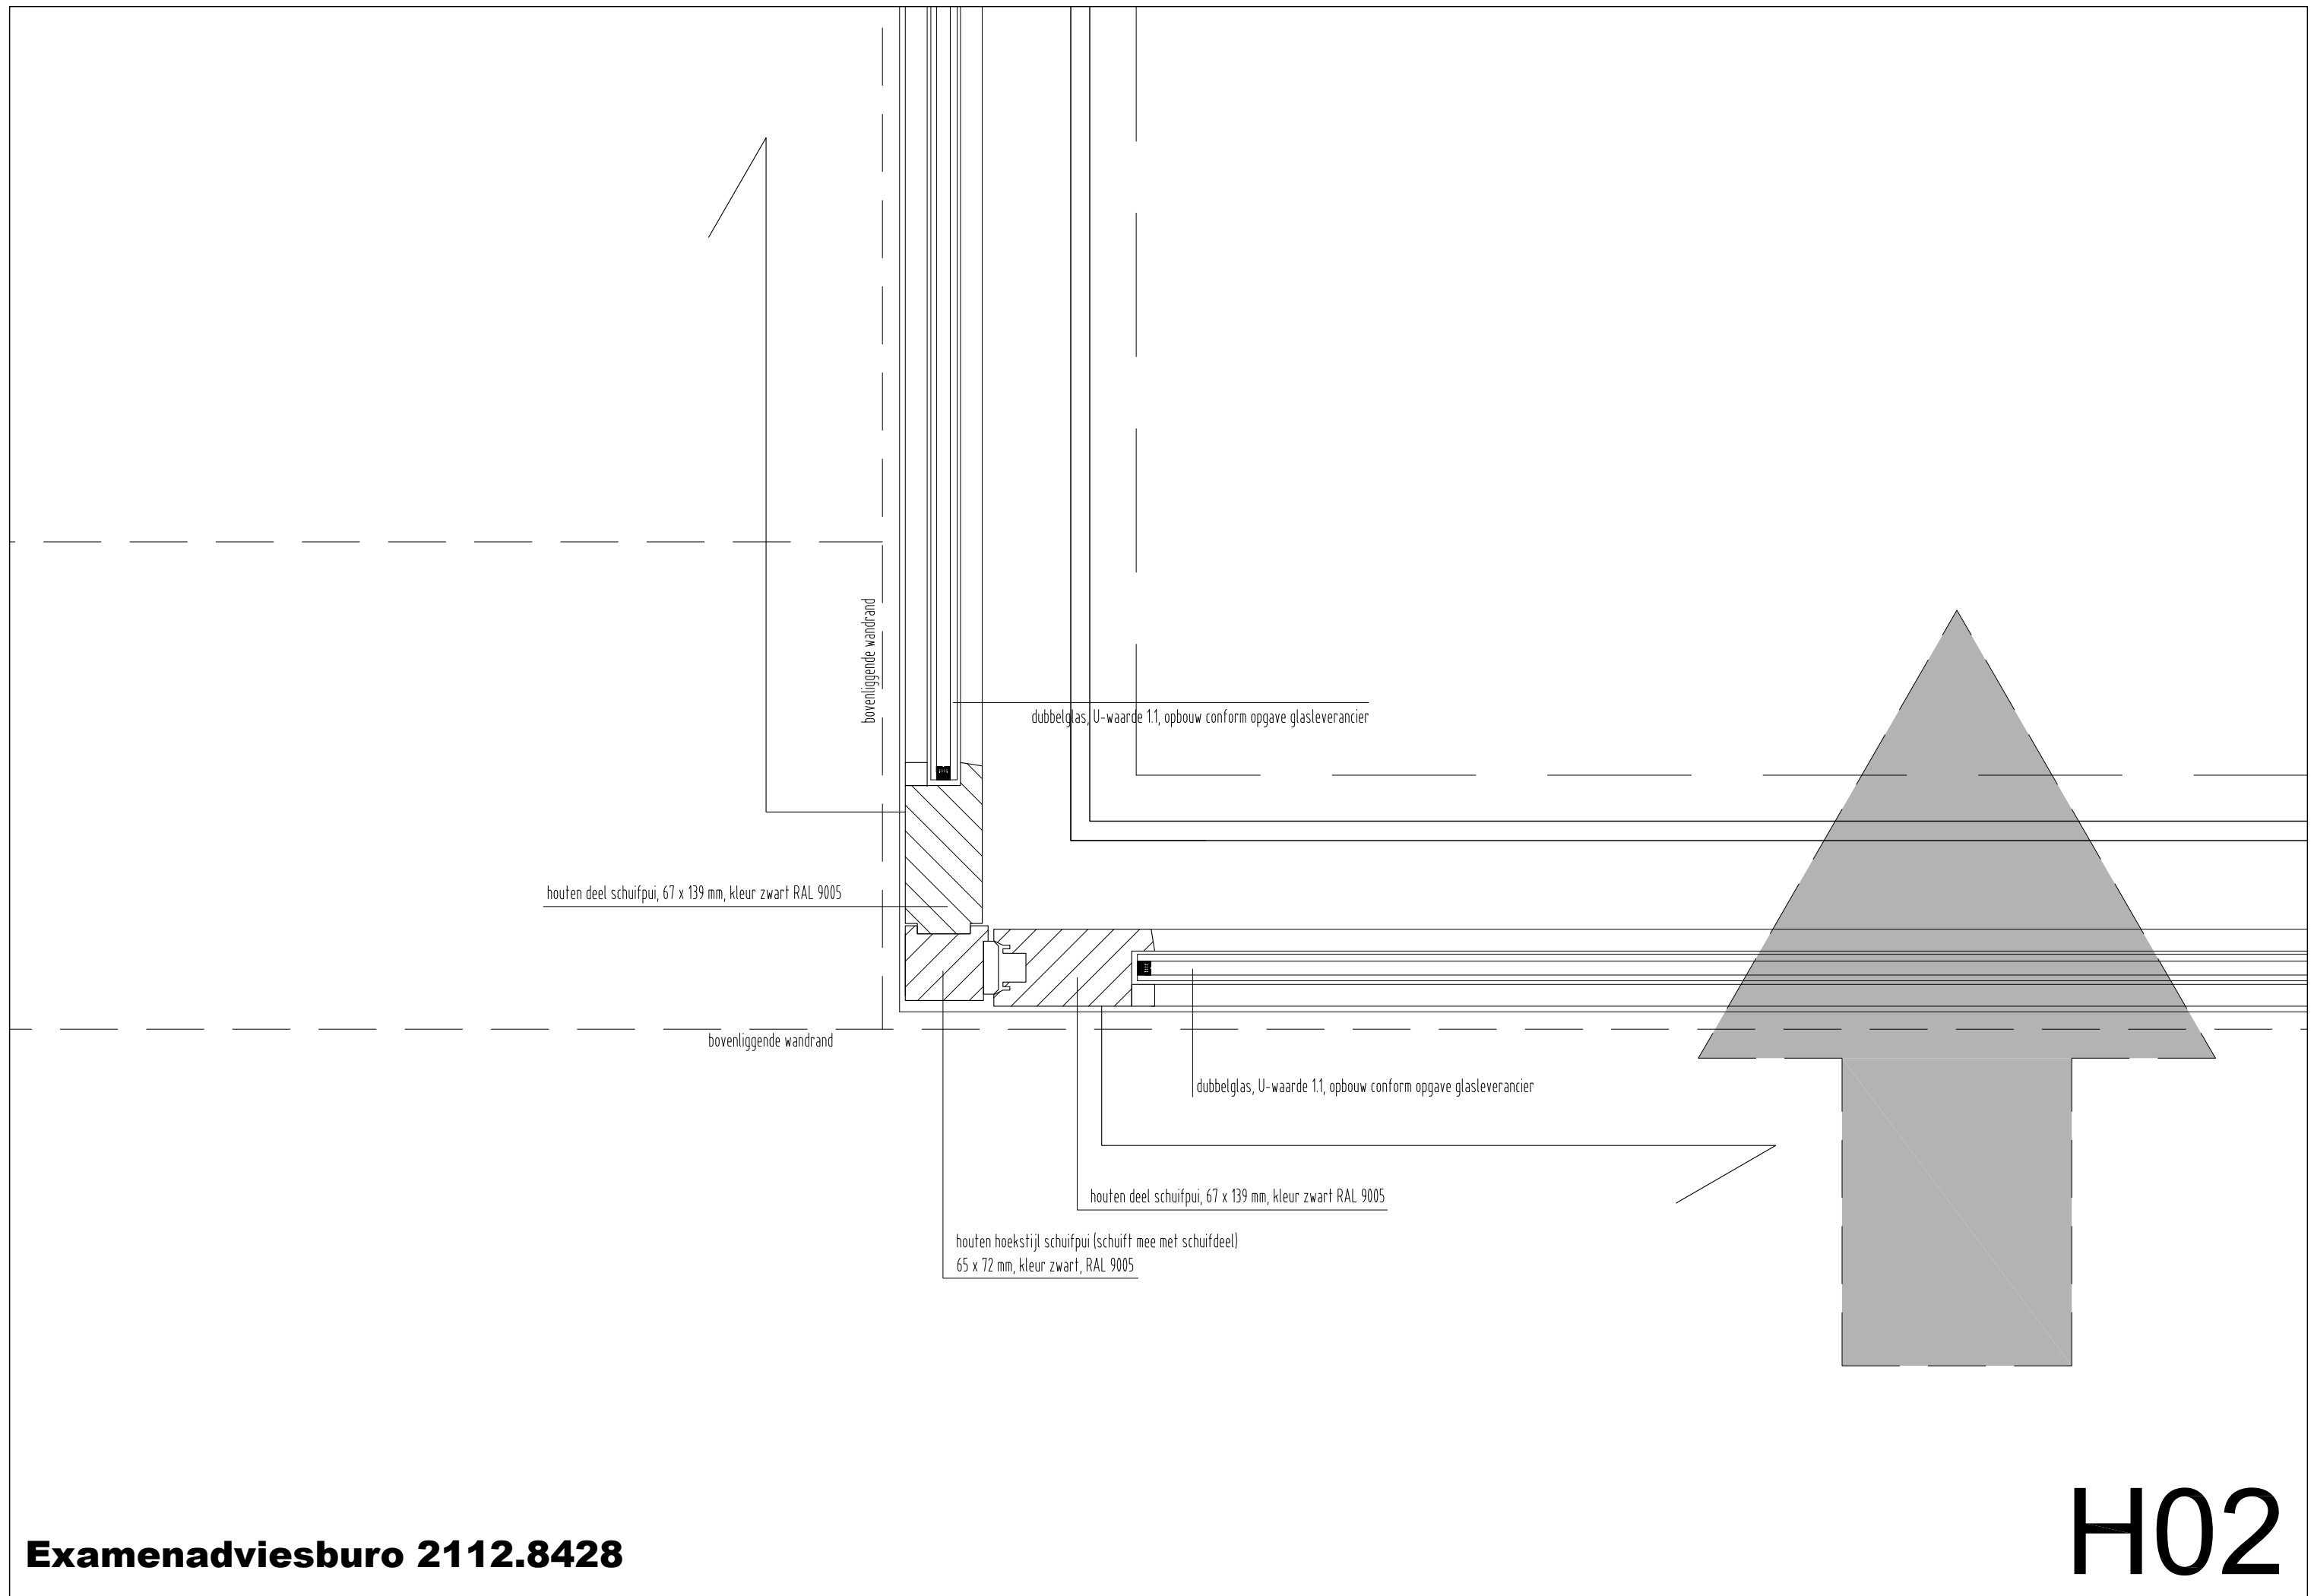


hwa

- opbouw binnen naar buiten WAND $R_c=3,2 \text{ m}^2 \text{ K} / \text{W}$:
- gipsplaat, afmetten, schuren en plamuren, schilderklaar KLASSE B
 - constructieve OSB plaat, 11 mm
 - dampremmende folie
 - HSB 38x140 mm HOH conform opgave constructeur, ingevuld met isolatie
 - dampopen waterkerende folie, kleur zwart
 - fengels 10 x 40 mm, kleur zwart
 - horizontaal regelwerk 28x59 mm, kleur zwart
 - Waxedwood, dikte 18 mm:
 - vuren fijnbezaagd
 - breedte houten delen: 95 mm
 - voeg 10 mm
 - kleur Woodstain FK-2015-005 EBBEN , 2x aangebracht
 - let op, alle bevestigingsmiddelen houtdelen, rvs, kleur zwart

2

D

H03

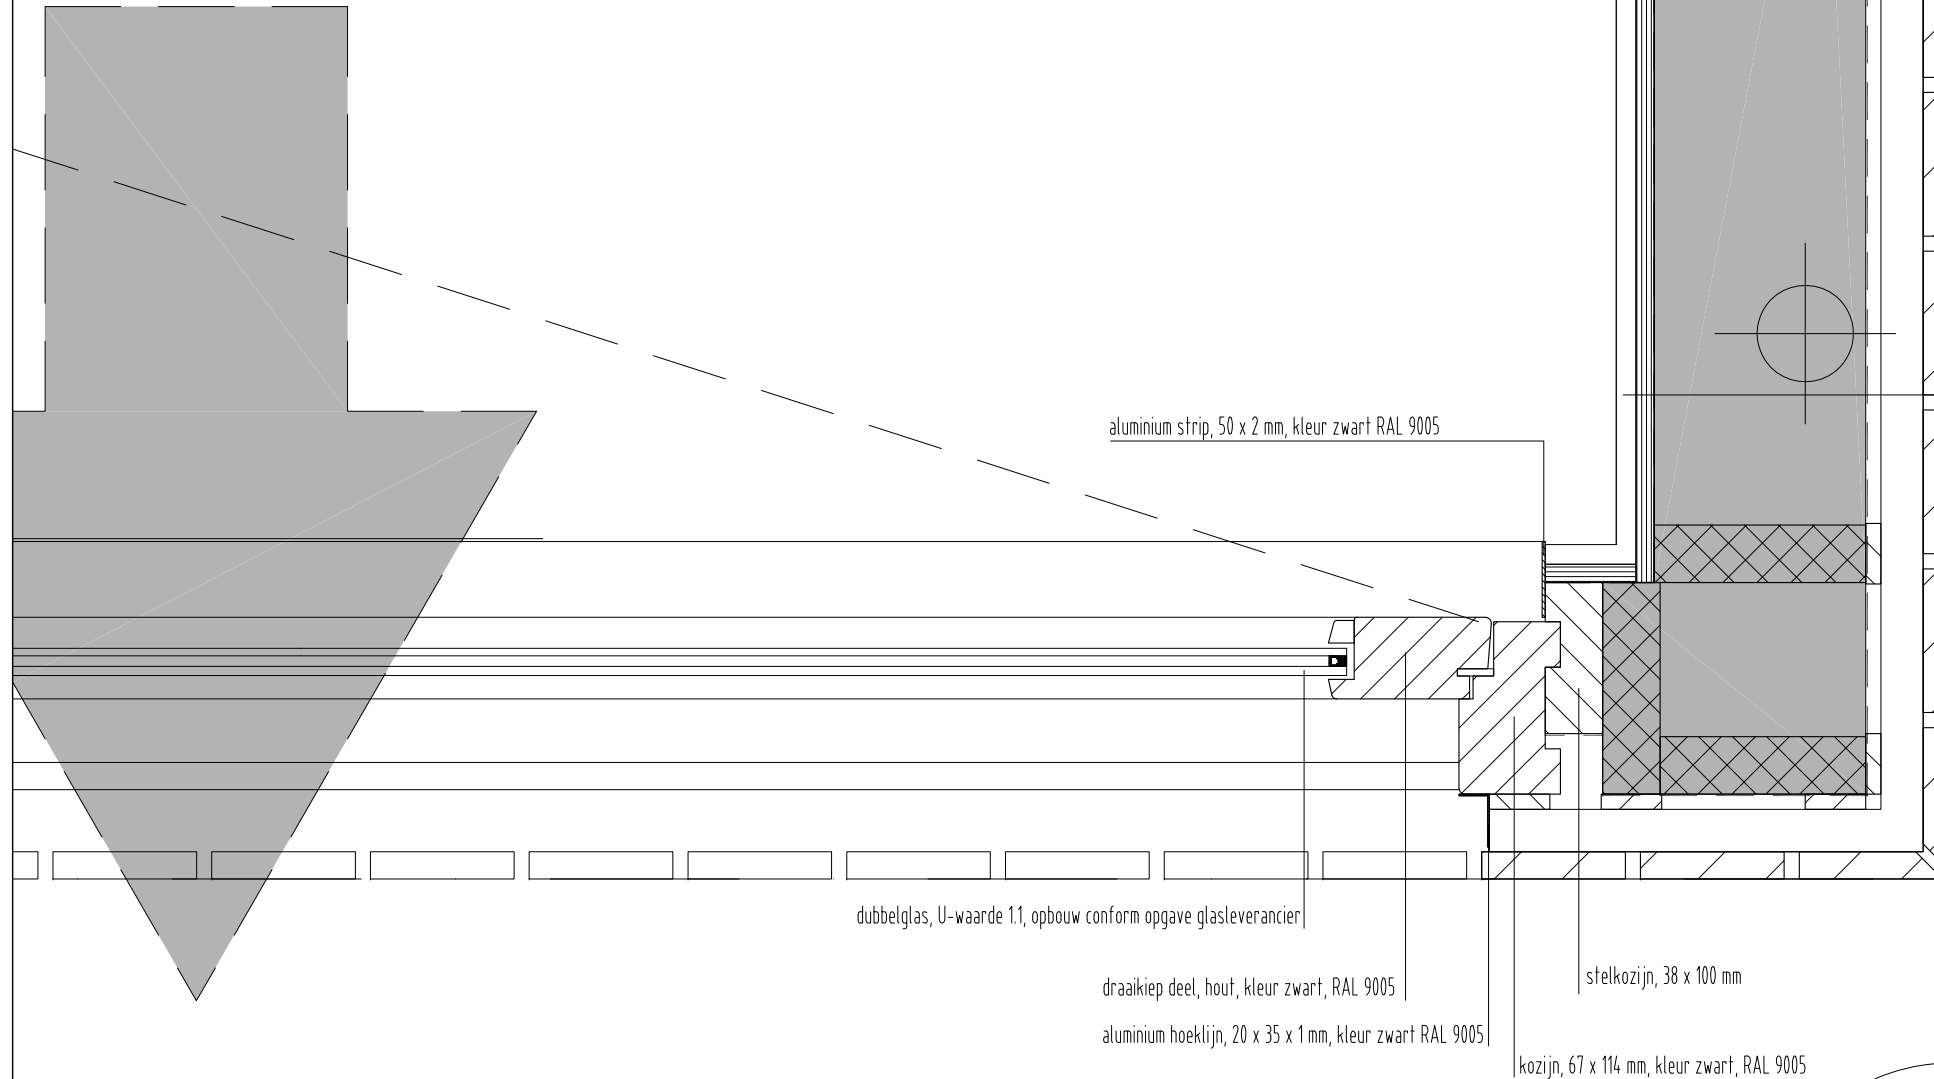

hwa

aluminium hoeklijn, 15 x 15 x 1 mm, kleur wit RAL n.f.b.

opbouw binnen naar buiten WAND Rc=3,2 m2 K / W :

- gipsplaat, afmeten, schuren en plamuren, schilderklaar KLASSE B
- constructieve OSB plaat, 11 mm
- dampremmende folie
- HSB 38x140 mm HOH conform opgave constructeur, ingevuld met isolatie
- dampopen waterkerende folie, kleur zwart
- tengels 10 x 40 mm, kleur zwart
- horizontaal regelwerk 28x59 mm, kleur zwart
- Waxedwood, dikte 18 mm:
 - vuren fijnbezaagd
 - breedte houten delen: 95 mm
 - voeg 10 mm
 - kleur Woodstain FK-2015-005 EBBEN , 2x aangebracht
- let op, alle bevestigingsmiddelen houtdelen, rvs, kleur zwart

stelkozijn schuifpui, 38 x 94 mm

houten kozijn schuifpui, 67 x 139 mm, kleur zwart RAL 9005

dubbelglas, U-waarde 1.1, opbouw conform opgave glasleverancier

aluminium hoeklijn, 20 x 35 x 1 mm, kleur zwart RAL 9005

