




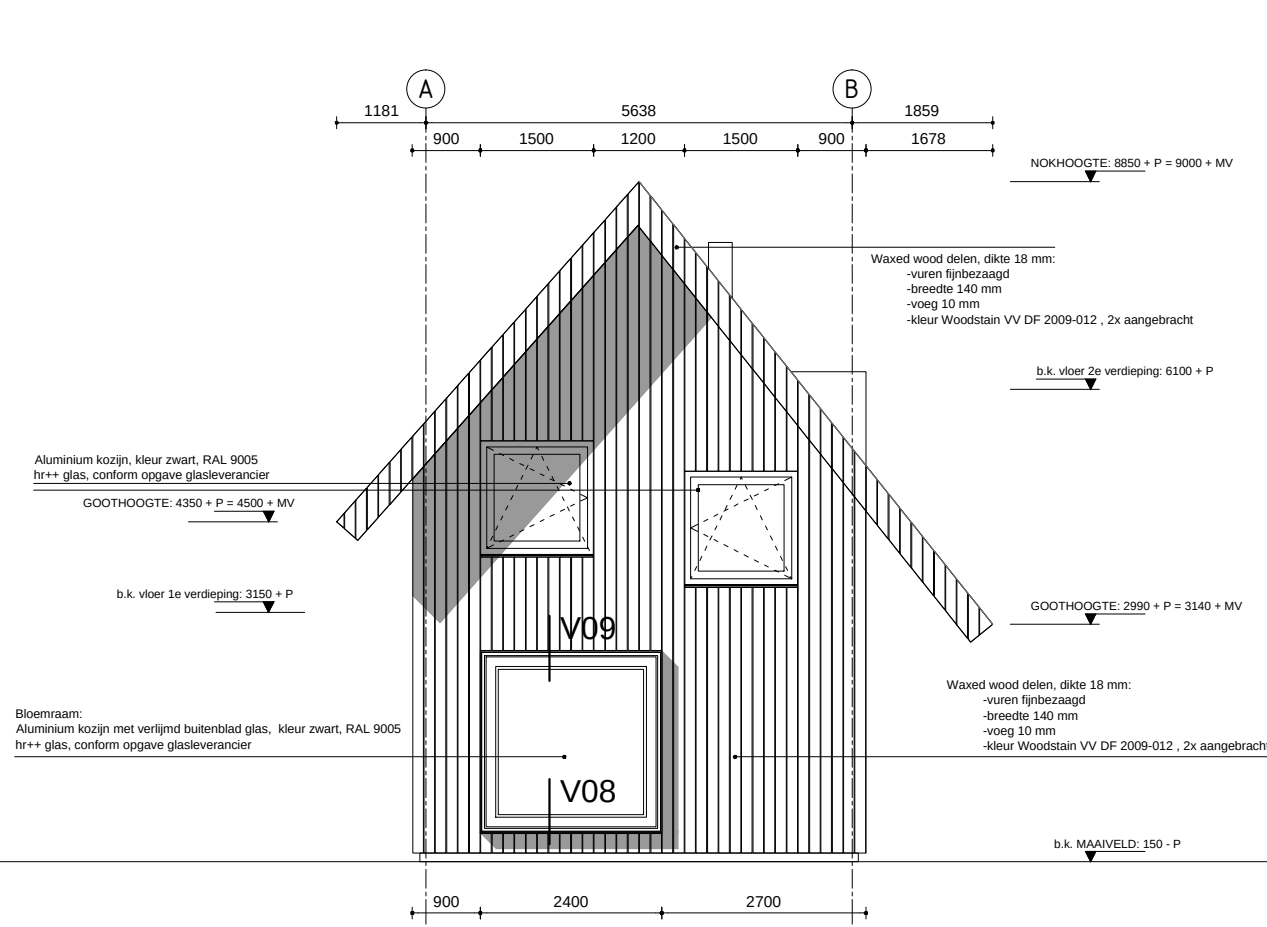


AANZICHT OOSTGEVEL (SCHAAL 1:100)

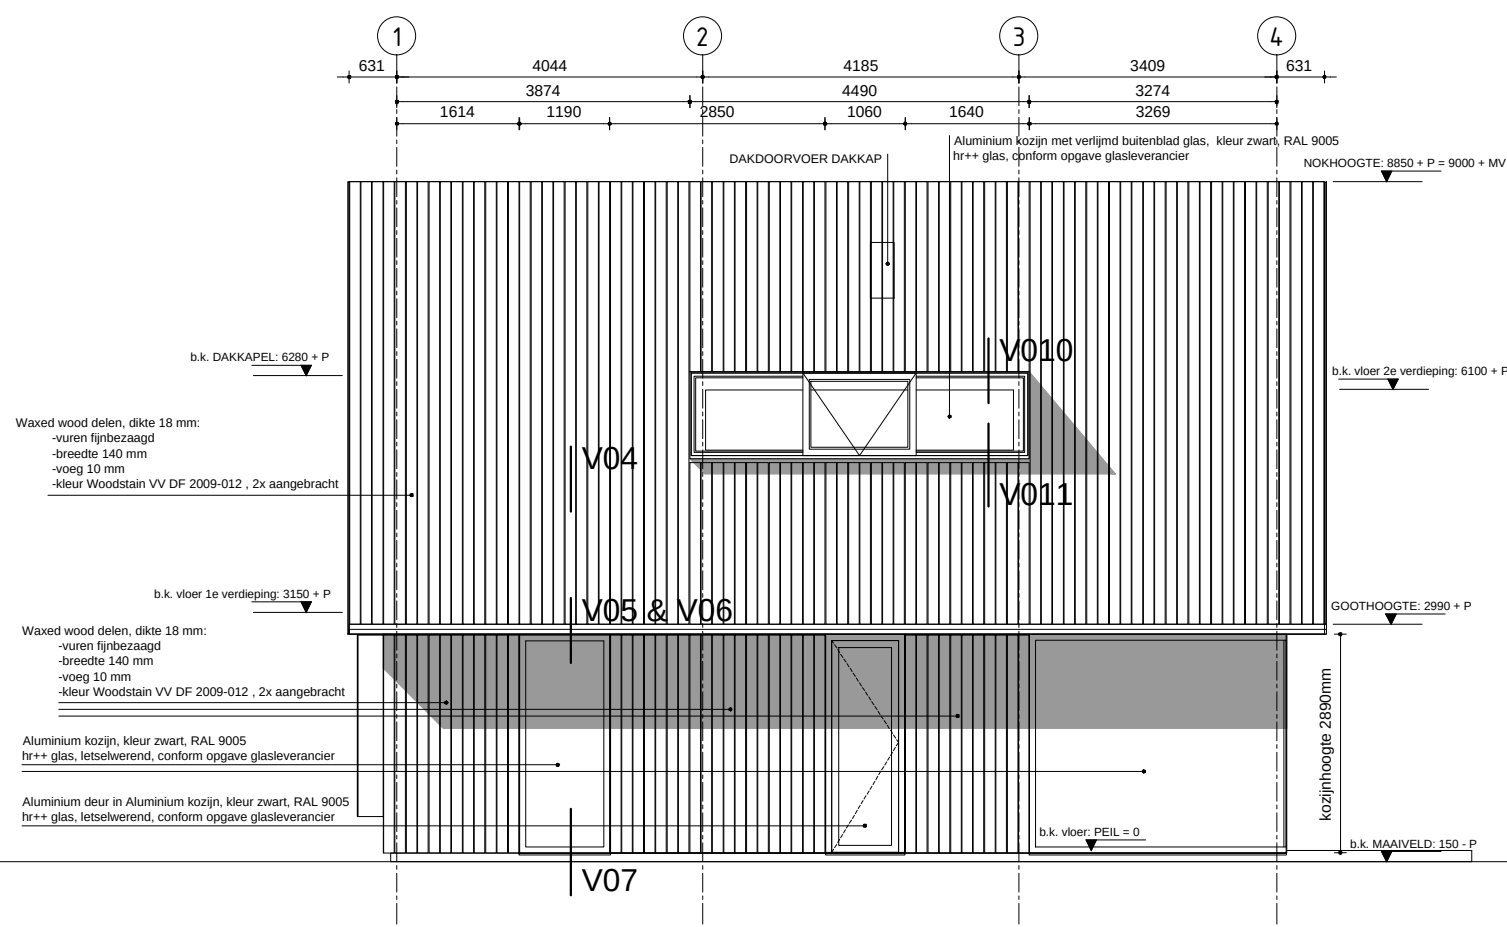


AANZICHT NOORDGEVEL (SCHAAL 1:100)

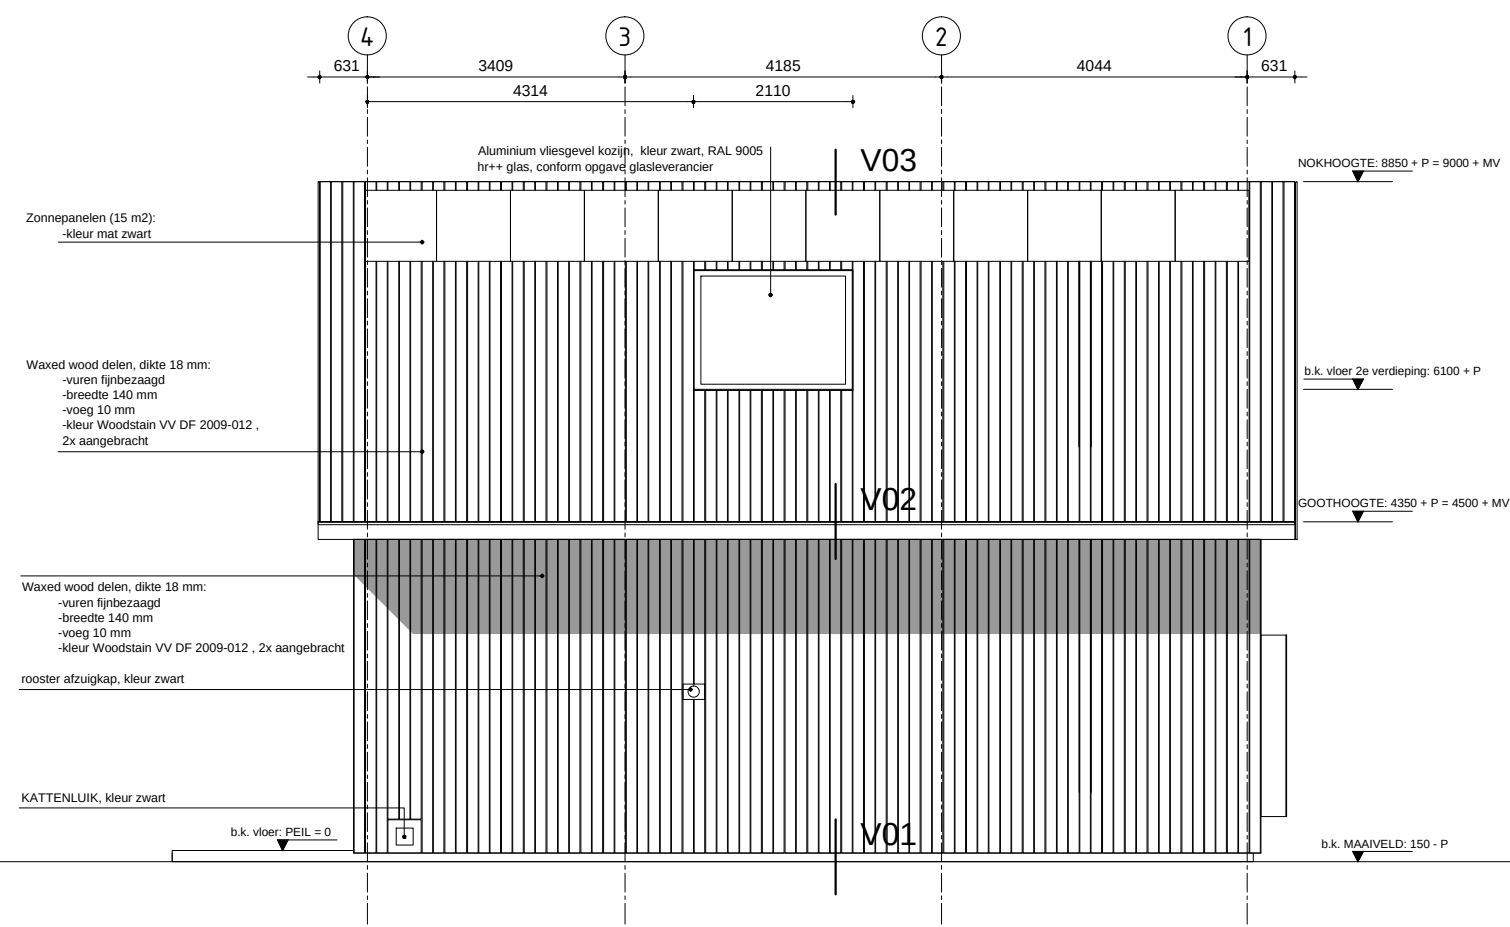


AANZICHT ZUIDGEVEL (SCHAAL 1:100)

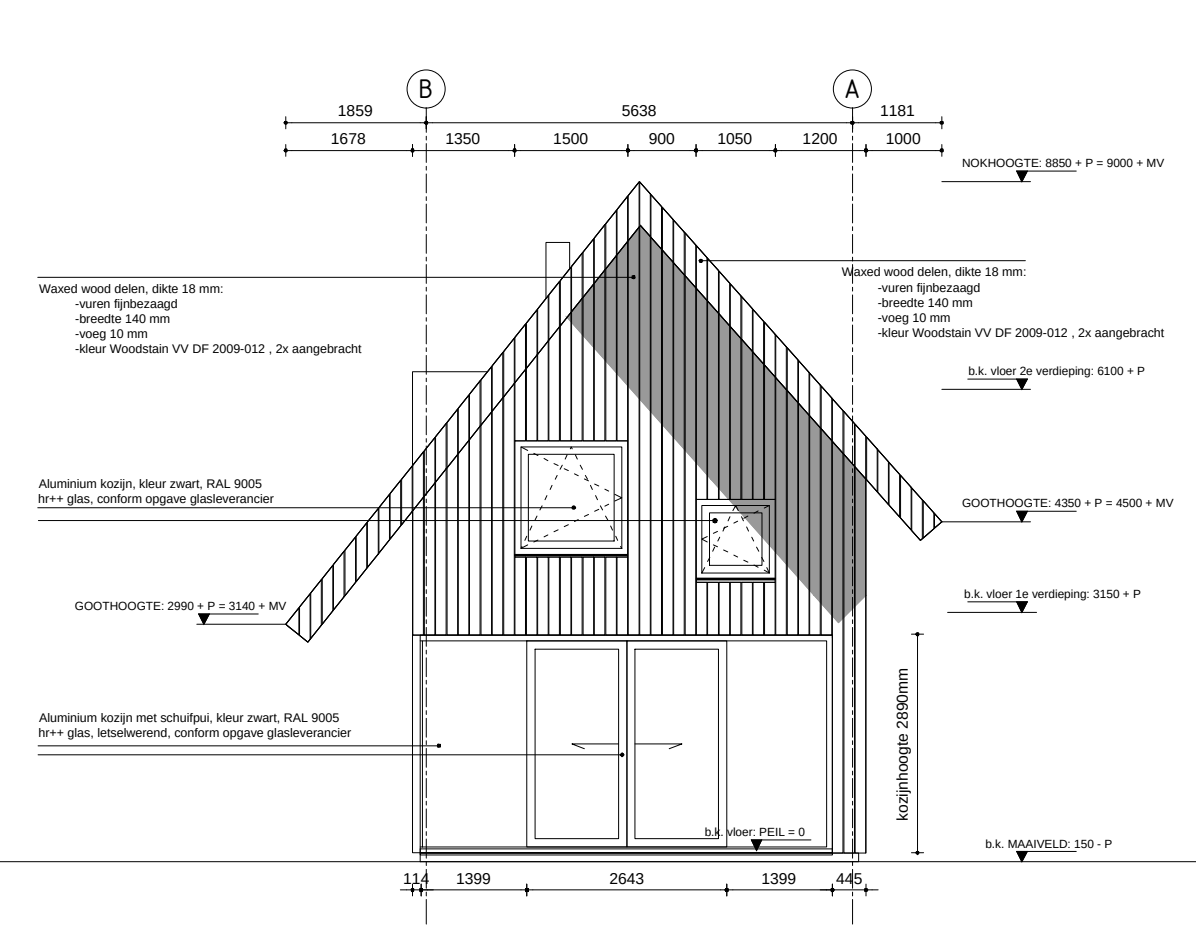


AANZICHT WESTGEVEL (SCHAAL 1:100)

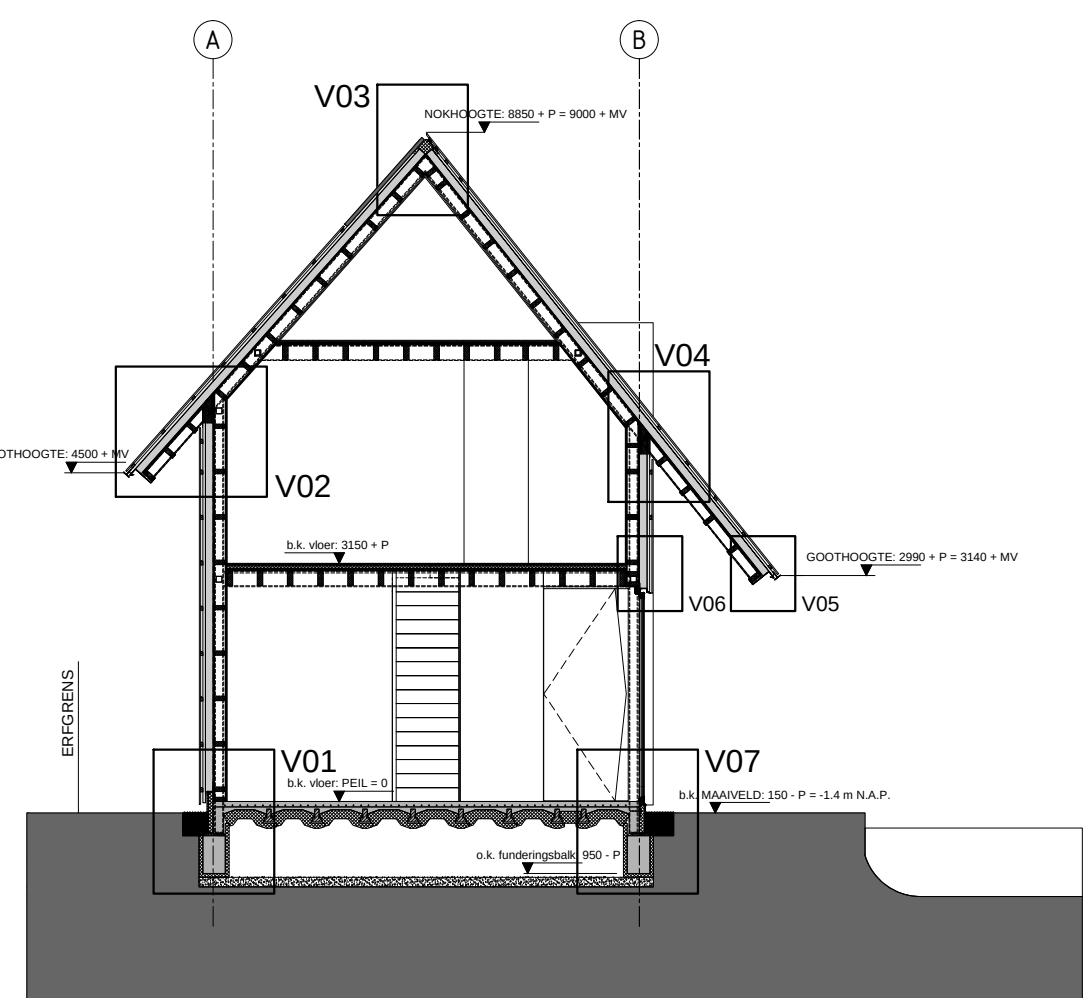


DRSN AA (SCHAAL 1:100)

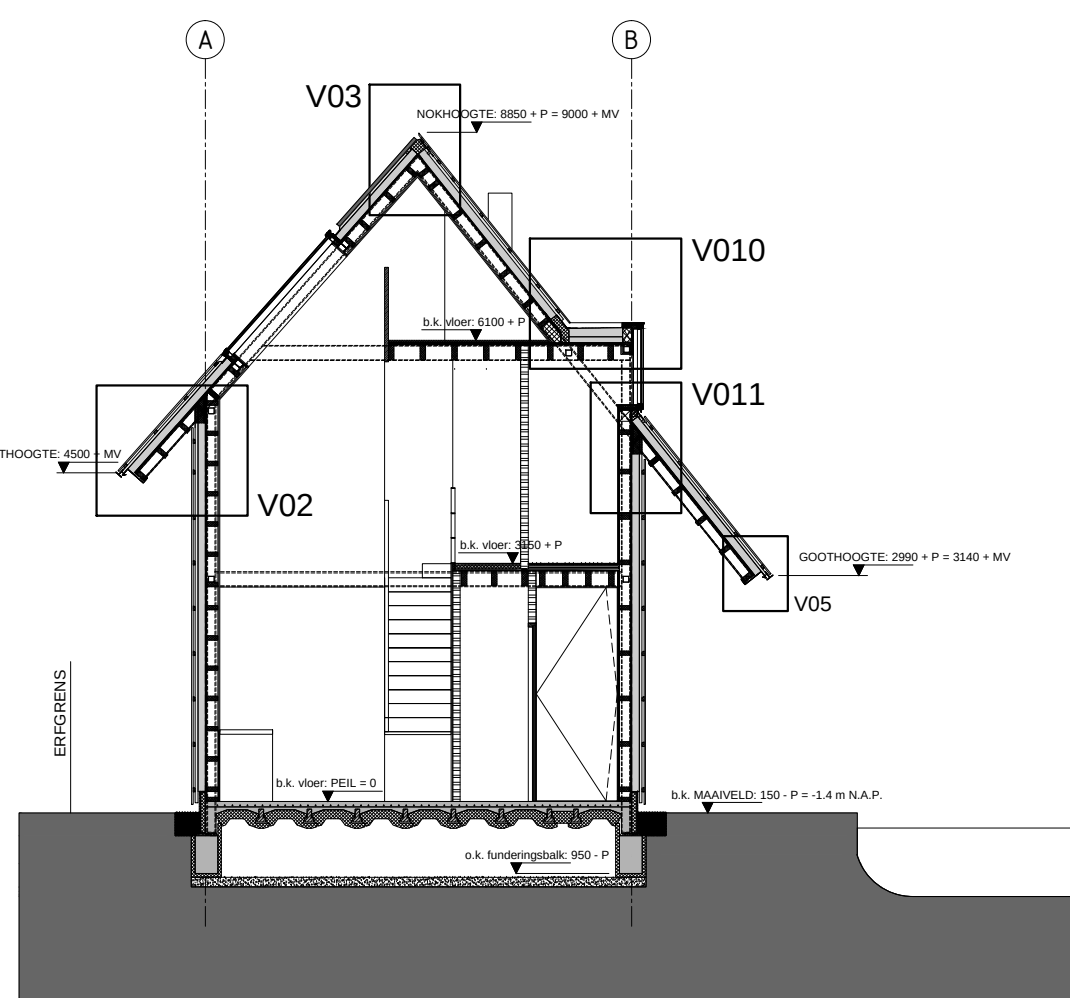


DRSN BB (SCHAAL 1:100)

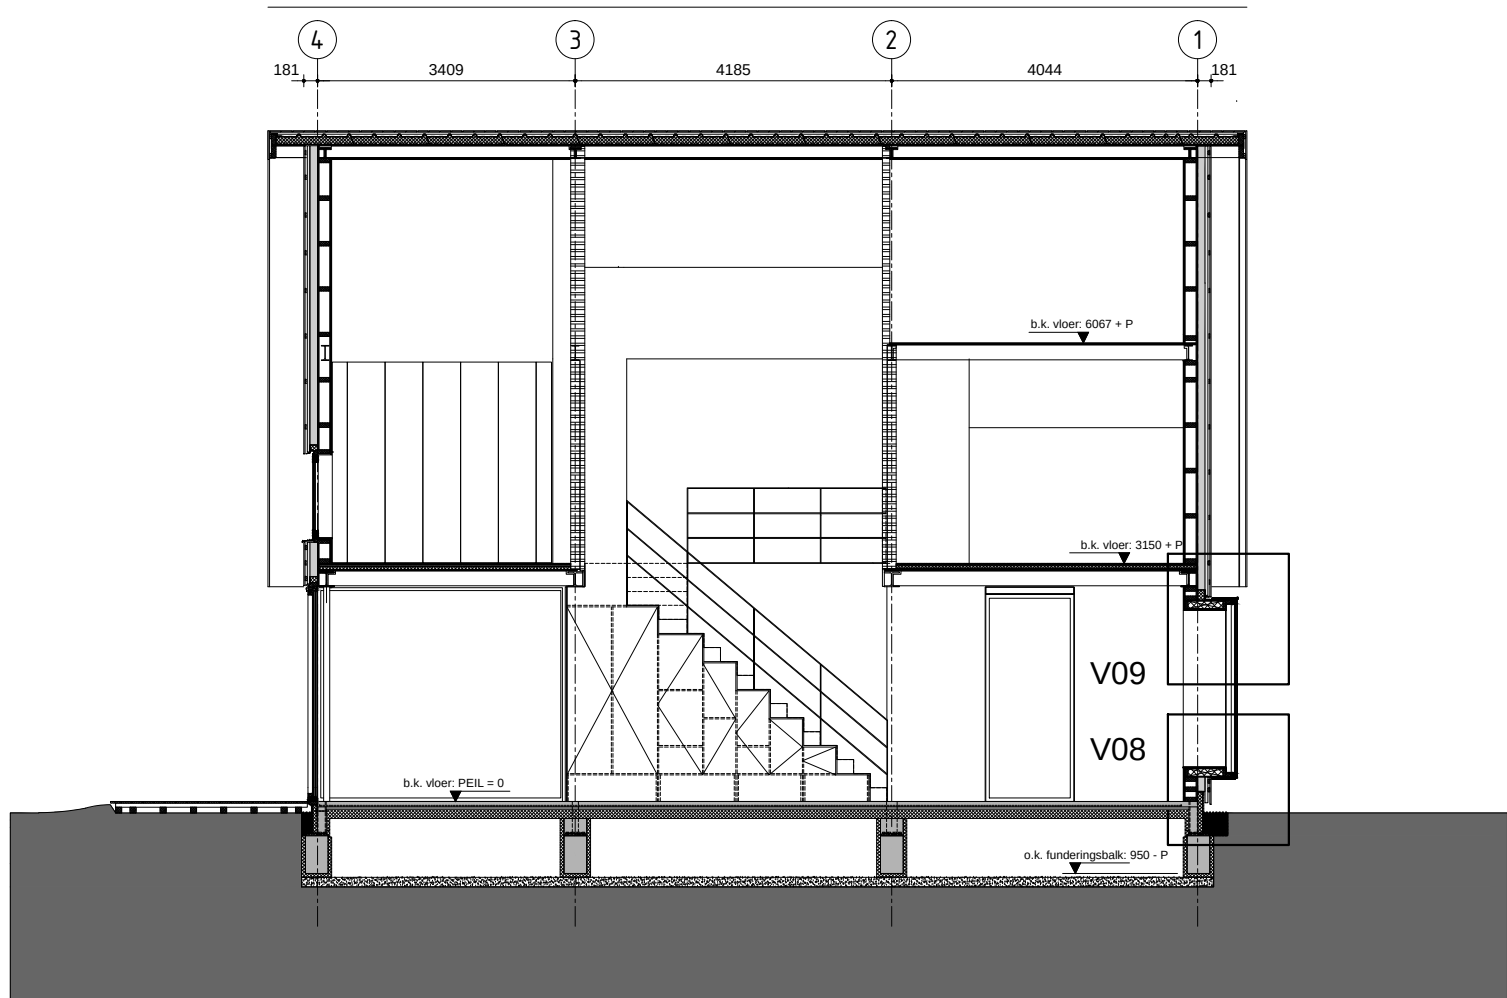


DRSN CC (SCHAAL 1:100)

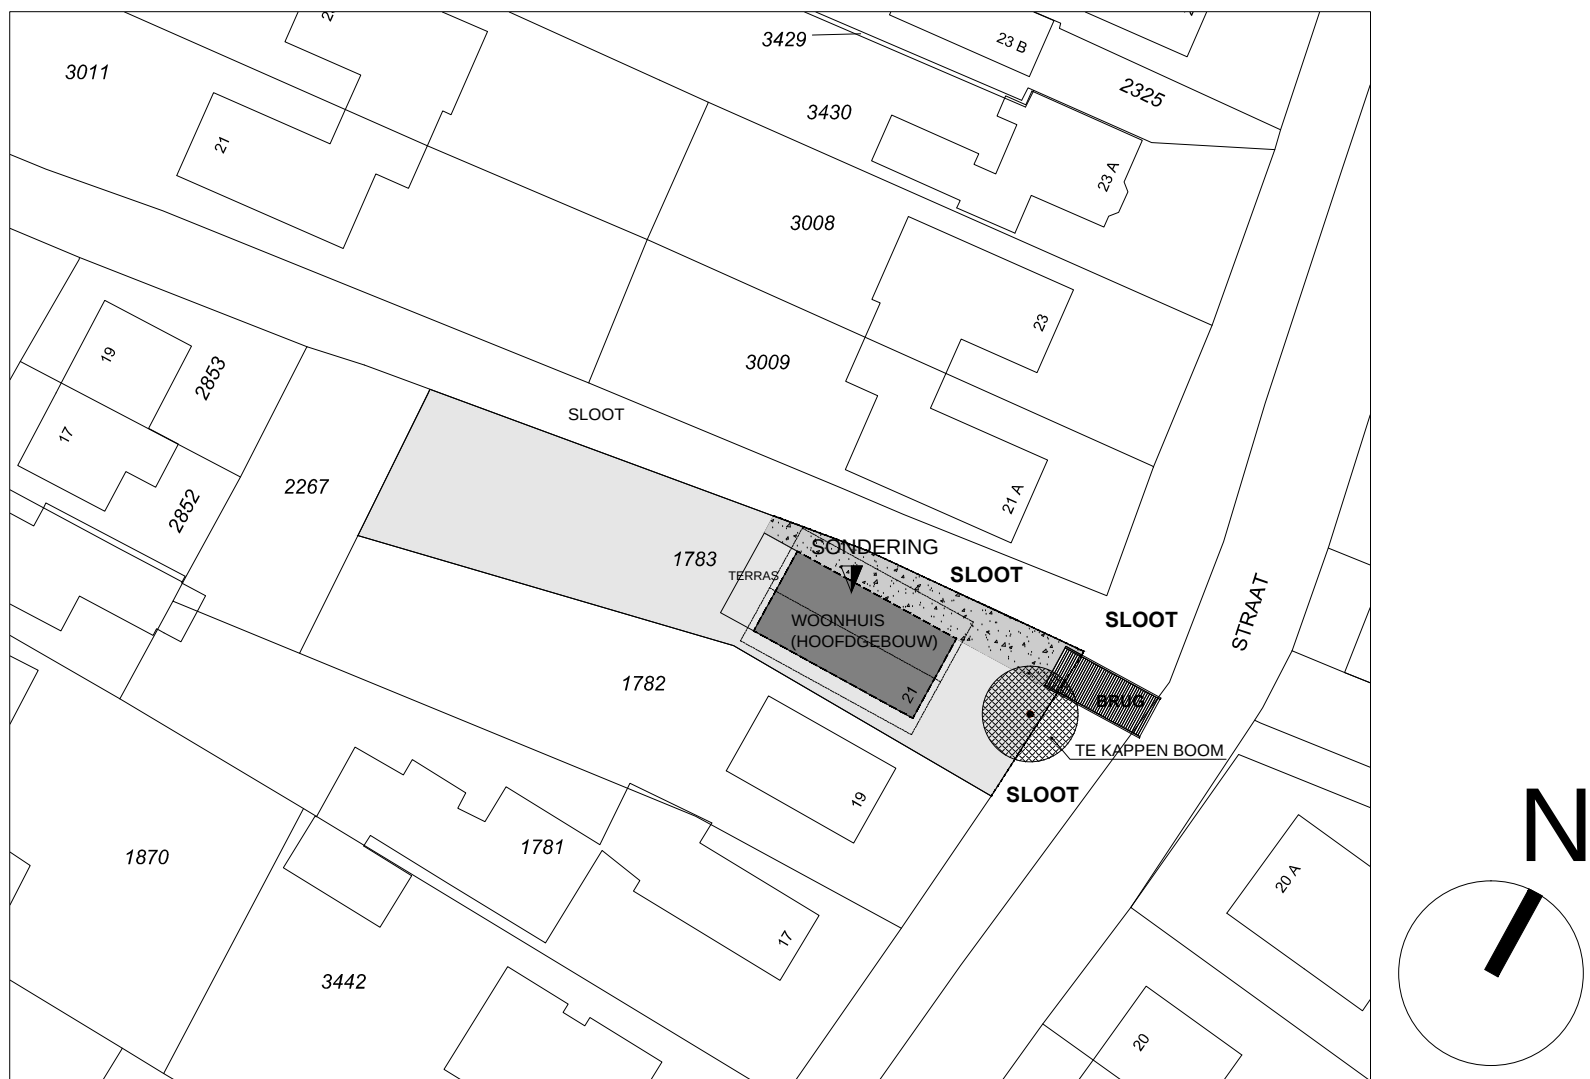


SITUATIE (SCHAAL 1:500)

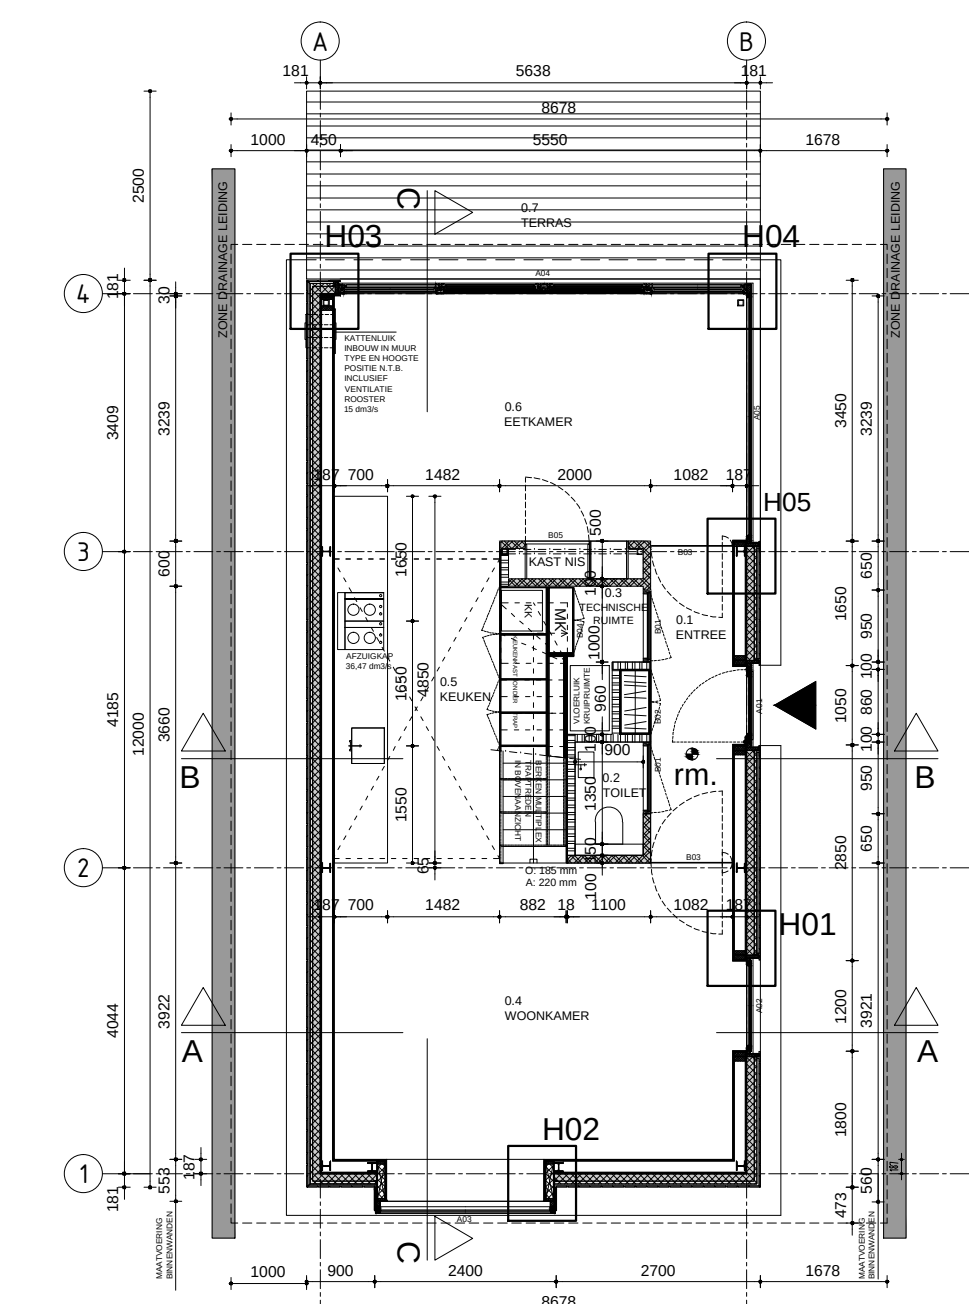


BEGANE GROND (SCHAAL 1:100)

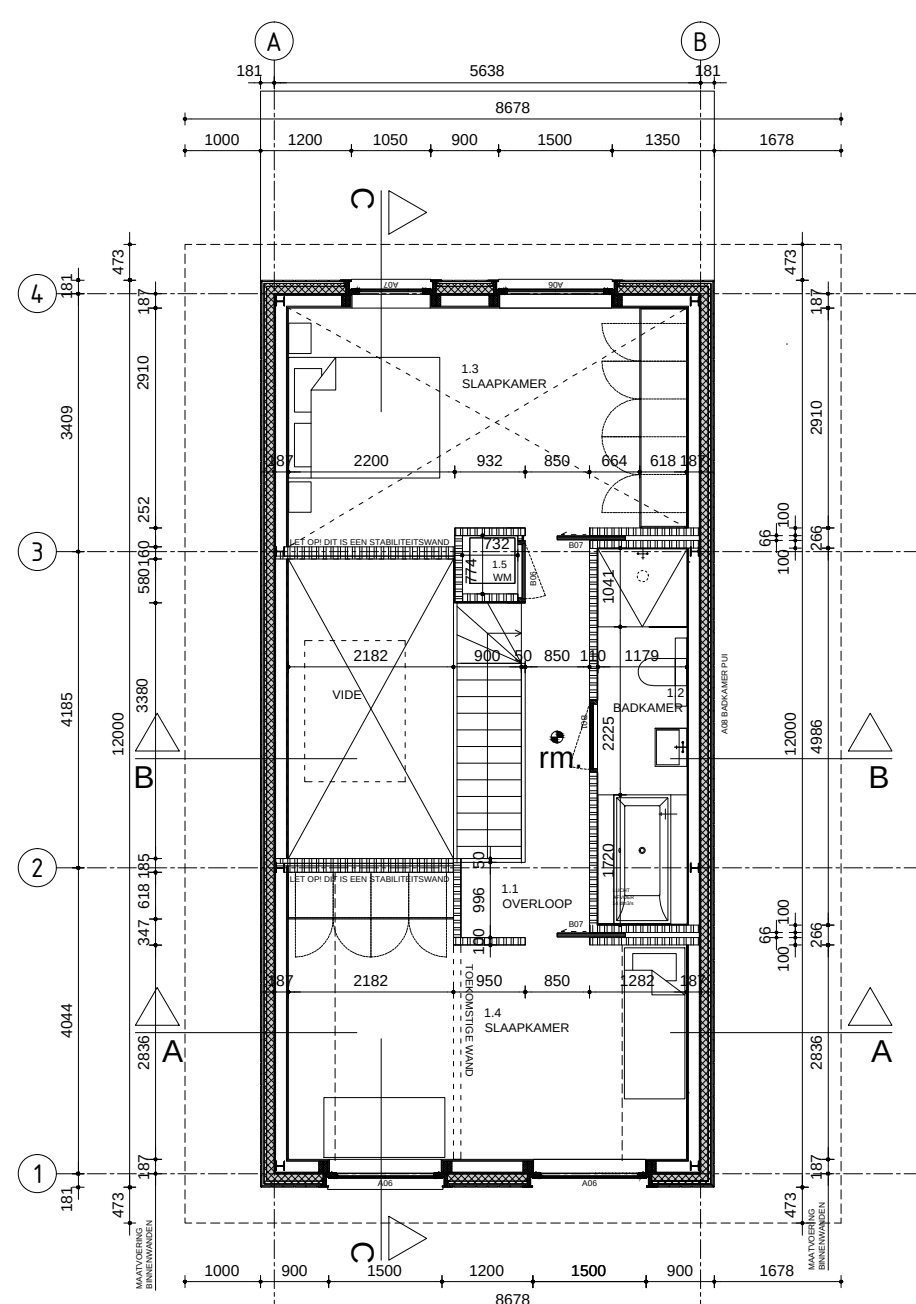


1e VERDIEPING (SCHAAL 1:100)

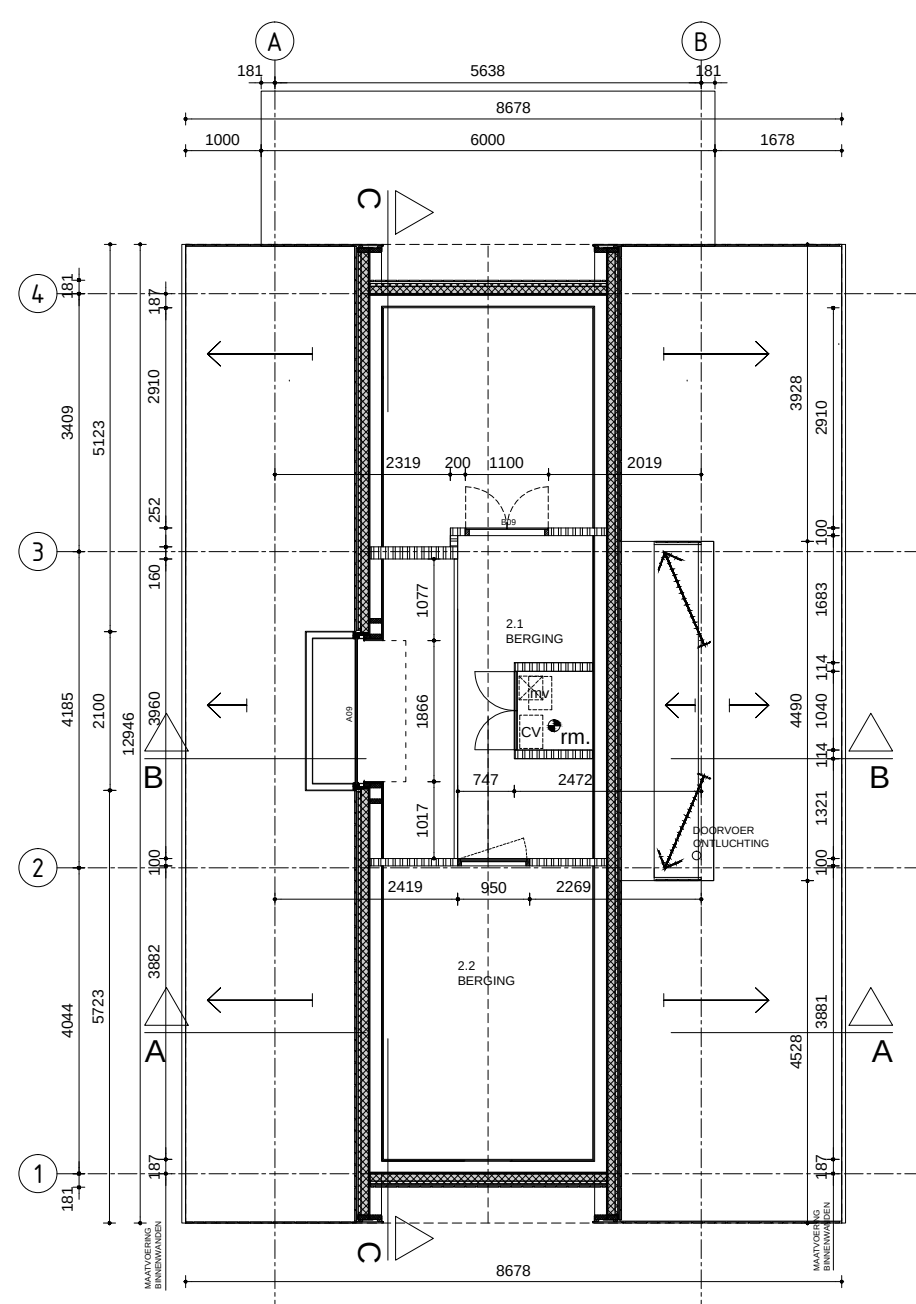

KAPVERDIEPING (SCHAAL 1:100)

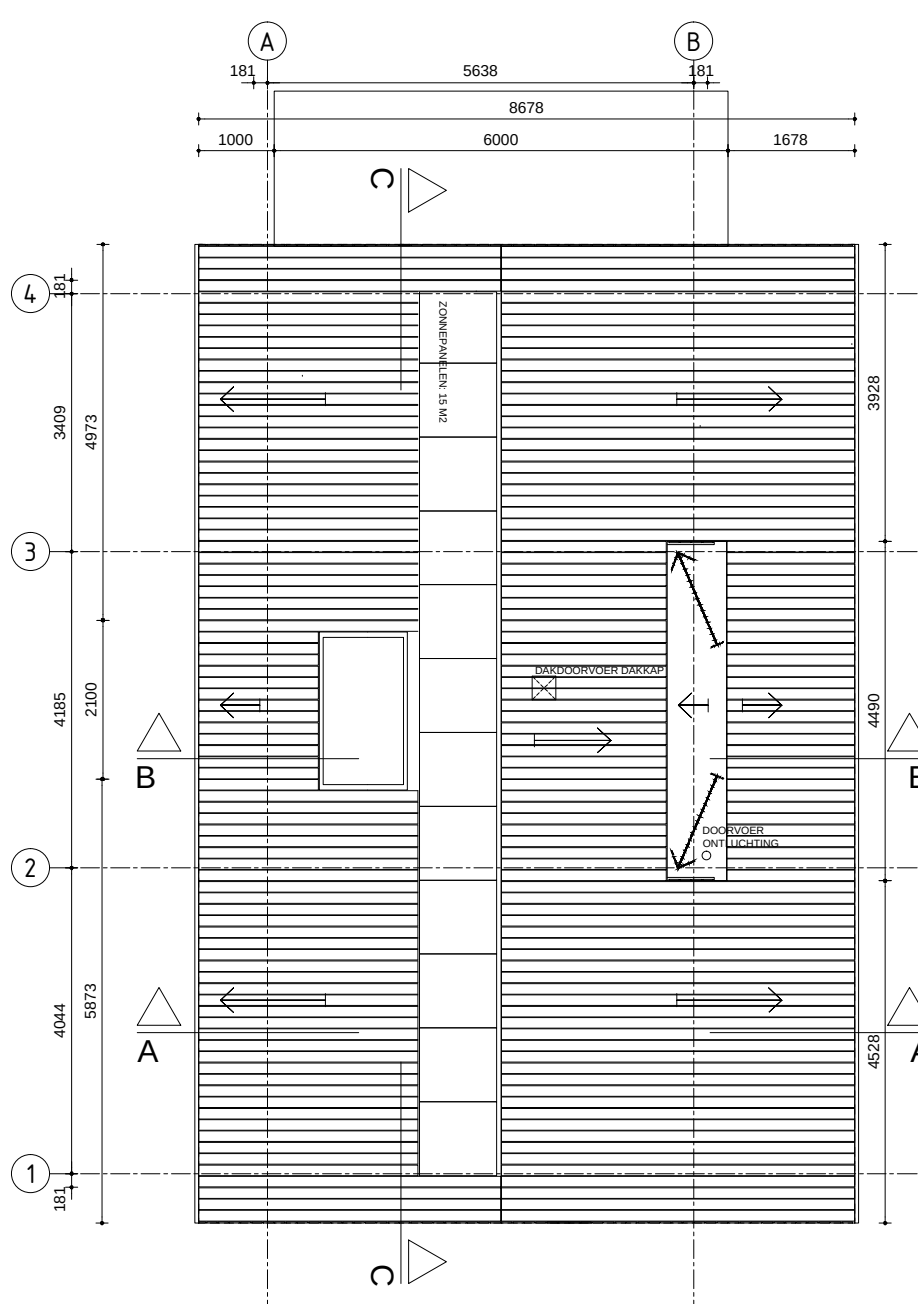

KAPAANZICHT (SCHAAL 1:100)

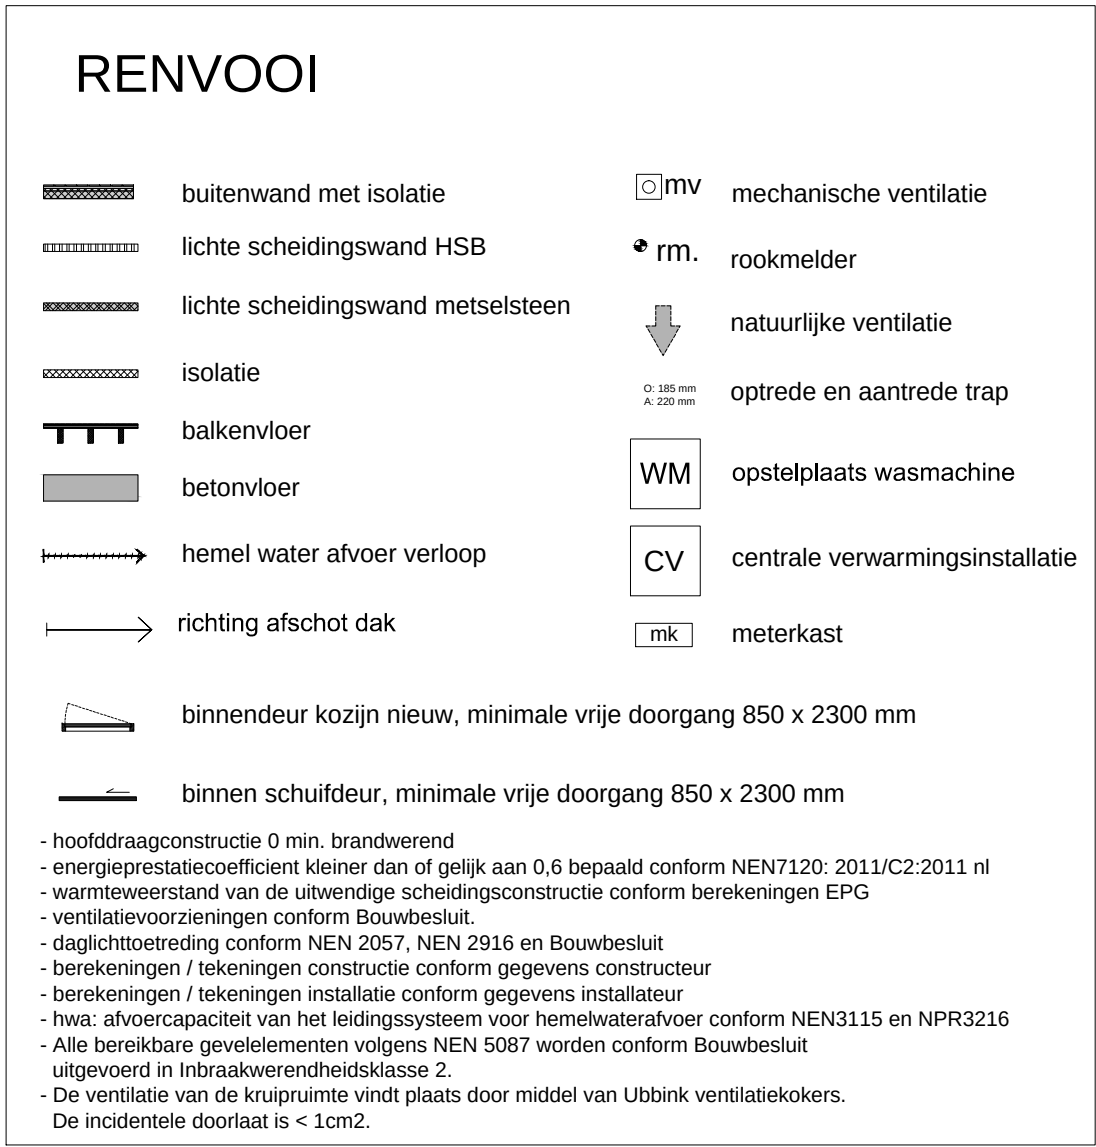

plattegronden, gevels, doorsneden, situatie
schaal 1:100/500

BLAD 1
Examenadviesburo 2016-I